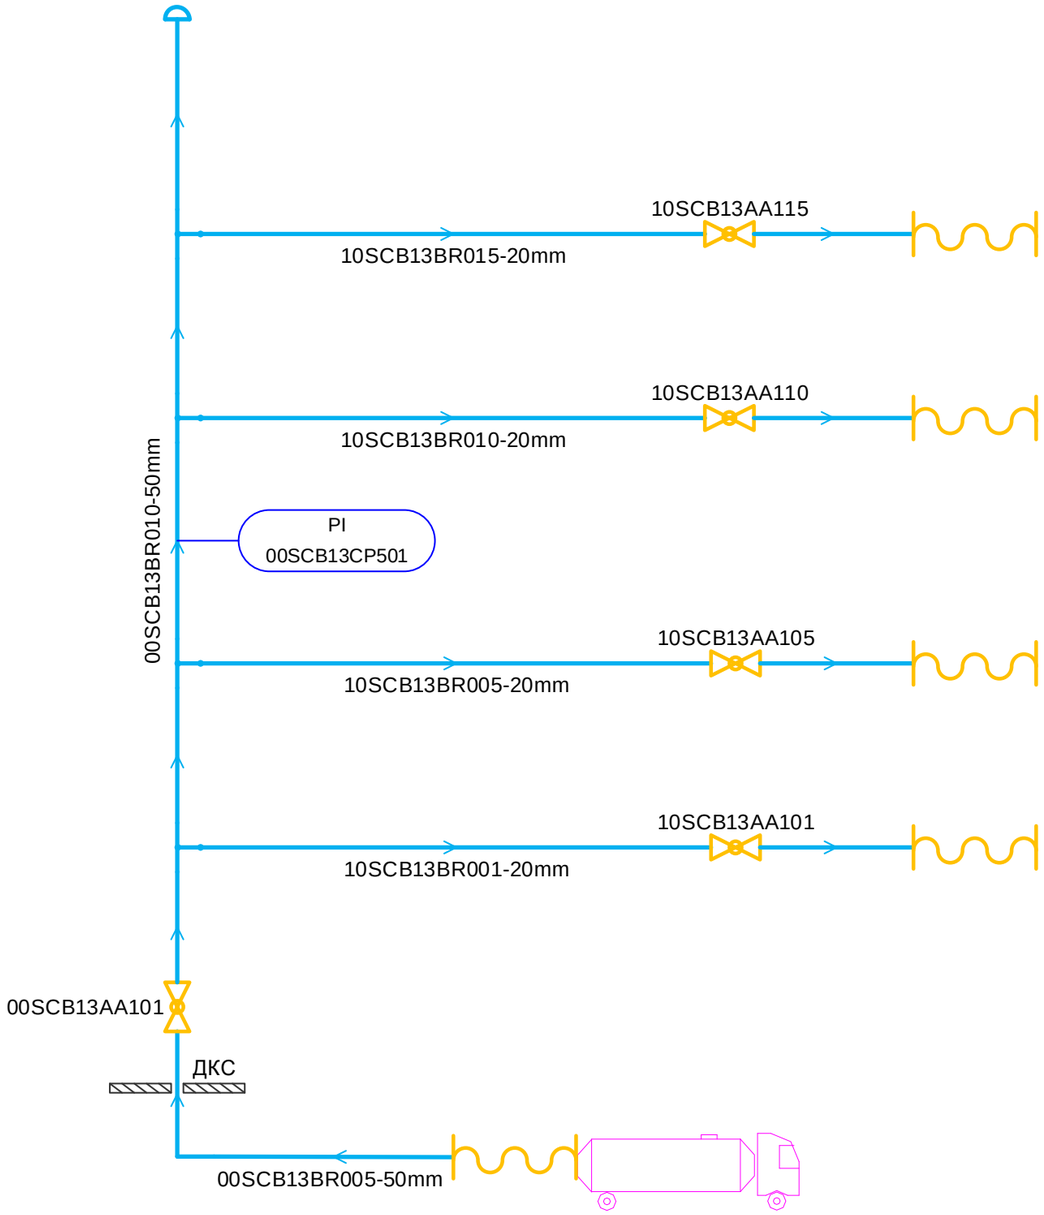

Согласовано

Взам. инв. №

Подпись и дата

Инв. № подл.

Изм.	Кол.уч	Лист	№ док.	Подп.	Дата
Разработал		Полянская			
Проверил		Стацура			
Н. контр.		Гридчина			

68N1 – 13UEP – 220 – TD.M

Строительство Якутской ГРЭС-2

Газодожимная компрессорная станция. PI-диаграмма сжатого воздуха на продувку газопроводов

Стадия	Лист	Листов
Р	2	

PI-диаграмма сжатого воздуха на продувку газопроводов. Система SCB.

АКЦИОНЕРНОЕ ОБЩЕСТВО ИНСТИТУТ ТЕПЛОЭЛЕКТРОПРОЕКТ Г. МОСКВА

Формат А3