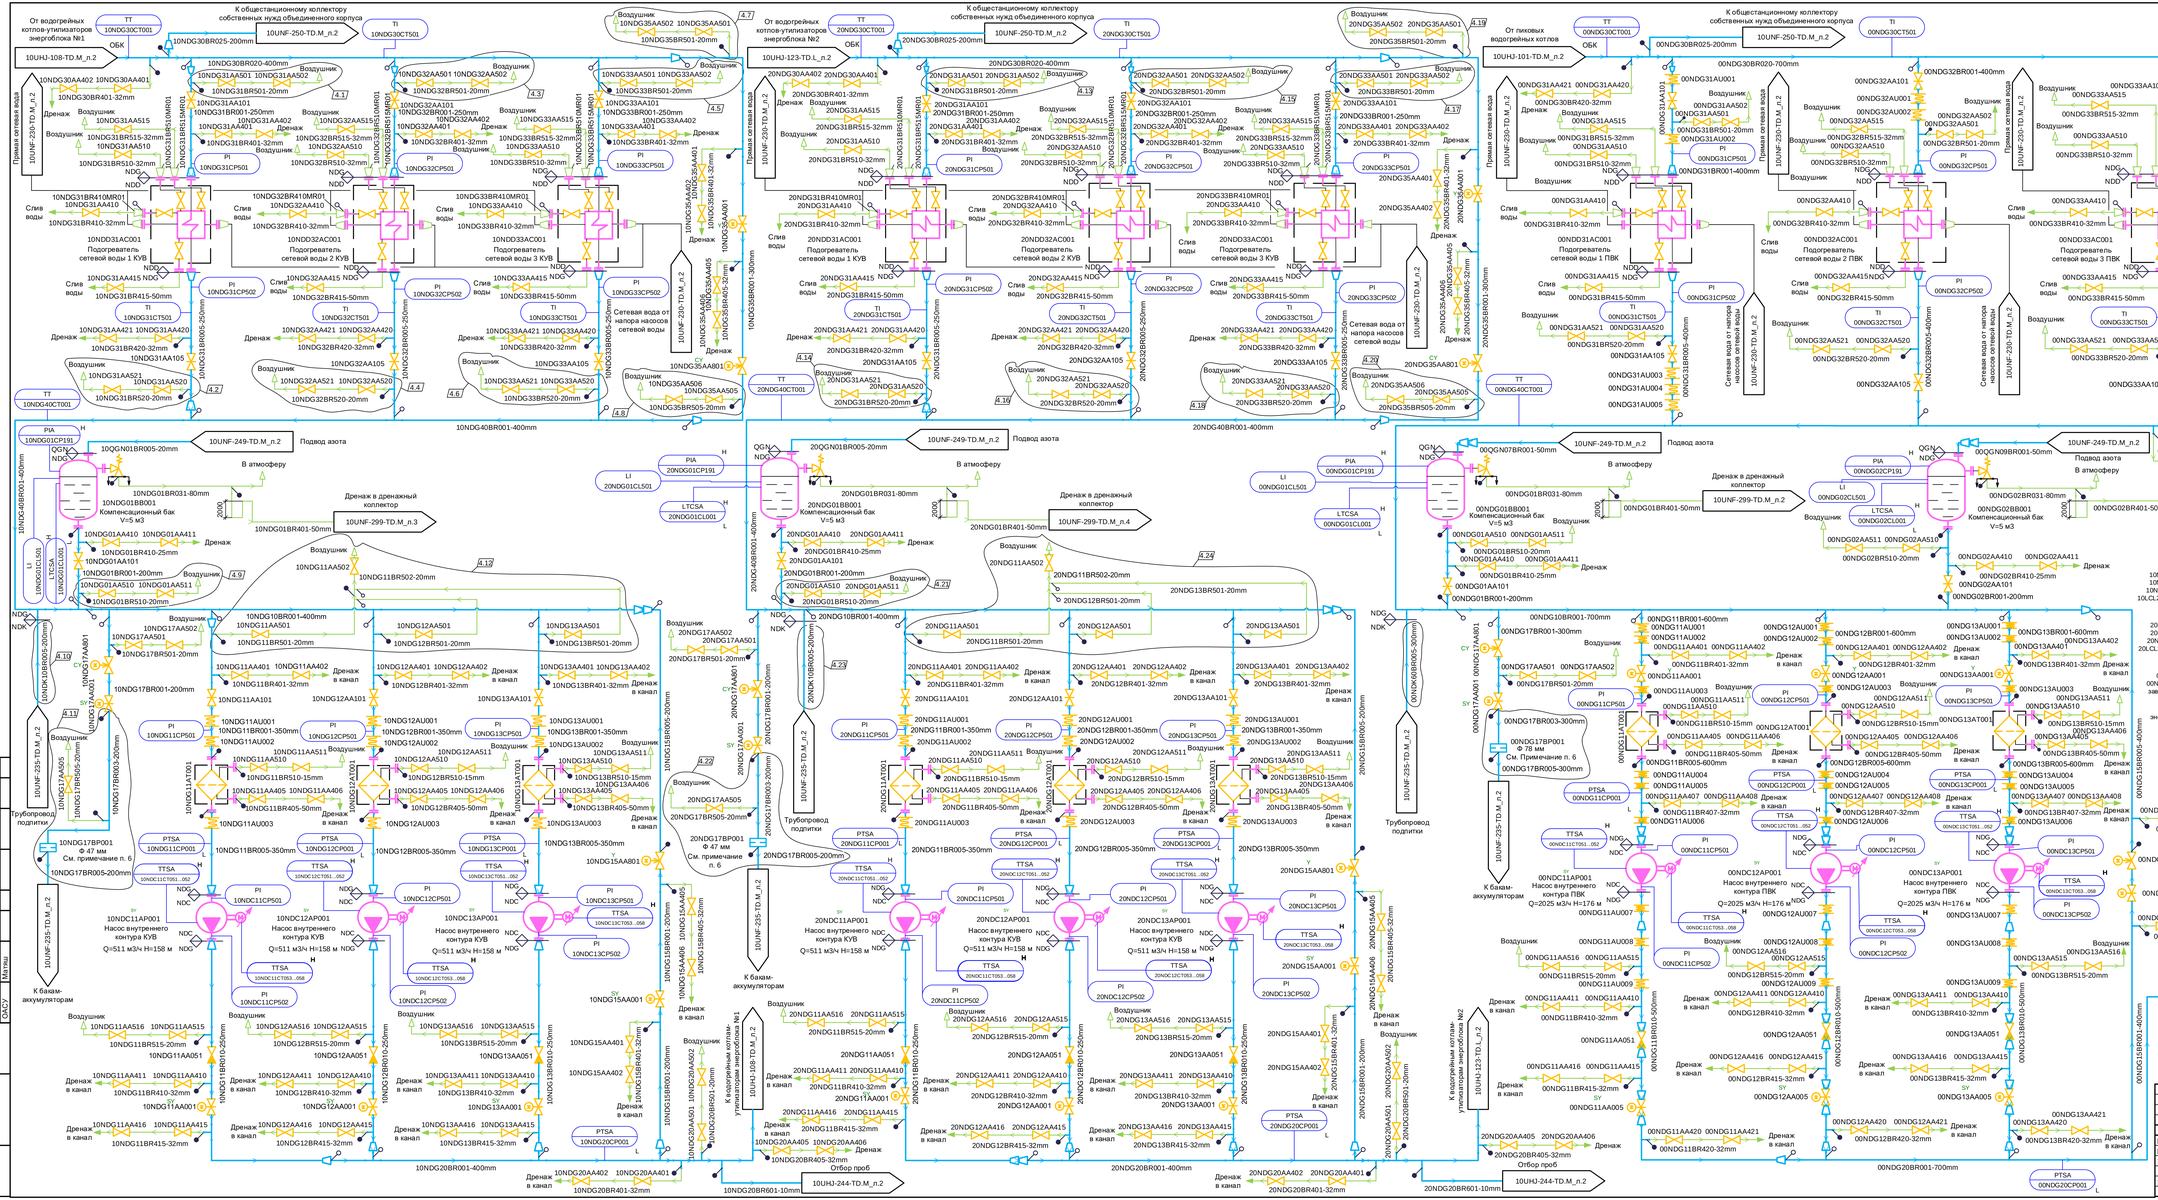
Примечание:
1. Деаэратор ПСВ КУВ энергоблока №1 10NDG11BR420-32mm, 10NDG11BR415-50mm, 10NDG11BR410-32mm, 10NDG11BR401-32mm, 10NDG12BR420-32mm, 10NDG12BR415-50mm, 10NDG12BR410-32mm, 10NDG12BR401-32mm, 10NDG13BR401-32mm, 10NDG13BR420-32mm, 10NDG13BR415-50mm, 10NDG13BR410-32mm, 10NDG13BR401-32mm, деаэратор на трубопроводе к компенсационному баку 10NDG01BR410-25mm заведены в коллектор 10LCL20BR001-150mm (См. PI-диаграмму трубопроводов деаэраций ПСВ КУВ энергоблока №1 68N1-10UNF-299-TD.M Лист 3).
2. Деаэратор ПСВ КУВ энергоблока №2 20NDG11BR420-32mm, 20NDG11BR415-50mm, 20NDG11BR410-32mm, 20NDG11BR401-32mm, 20NDG12BR420-32mm, 20NDG12BR415-50mm, 20NDG12BR410-32mm, 20NDG12BR401-32mm, 20NDG13BR401-32mm, 20NDG13BR420-32mm, 20NDG13BR415-50mm, 20NDG13BR410-32mm, 20NDG13BR401-32mm, деаэратор на трубопроводе к компенсационному баку 20NDG01BR410-25mm заведены в коллектор 20LCL20BR001-150mm (См. PI-диаграмму трубопроводов деаэраций ПСВ КУВ энергоблока №2 68N1-10UNF-299-TD.M Лист 4).
3. Деаэратор ПСВ ПВК 00NDG11BR410-32mm, 00NDG11BR415-50mm, 00NDG12BR410-32mm, 00NDG12BR415-50mm, 00NDG13BR410-32mm, 00NDG13BR415-50mm, 00NDG34BR410-32mm, 00NDG34BR415-50mm, 00NDG40BR420-32mm, 00NDG35BR420-32mm, деаэратор на трубопроводах к компенсационным бакам 00NDG01BR410-25mm, 00NDG02BR410-25mm заведены в коллектор 00LCL45BR001-400mm (См. PI-диаграмму трубопроводов деаэраций КУВ, ПВК 68N1-10UNF-299-TD.M Лист 2).
4. Деаэратор КУВ энергоблока №1 за стеной здания ОБК 10NDG30BR401-32mm, 10NDG20BR405-32mm, деаэратор КУВ энергоблока №2 за стеной здания ОБК 20NDG30BR401-32mm, 20NDG20BR405-32mm, деаэратор ПВК за стеной здания ОБК 00NDG30BR420-32mm, 00NDG20BR410-32mm заведены в коллектор 00LCL40BR001-400mm (См. PI-диаграмму трубопроводов деаэраций КУВ, ПВК 68N1-10UNF-299-TD.M Лист 2).
5. Деаэраторы насосов КУВ и ПВК заведены в деаэрационный канал.
6. Шайбу 10NDG17BP001, 20NDG17BP001,00NDG17BP001 установить как можно ближе к коллектору 00NDG18BR006-400mm (См. PI-диаграмму 68N1-10UNF-235-TD.M)
68N1 – 10UNF – 225 – TD.M
Строительство Якутской ГРЭС-2
Изм. Кол.уч. Лист № док. Подп. Дата
Разработал Калинкина
Проверил Бобров
Гл. спец. Стапура
Н. контр. Астраханцев
Объединенный корпус.
PI-диаграмма трубопроводов воды внутреннего контура КУВ и ПВК
PI-диаграмма трубопроводов воды внутреннего контура КУВ и ПВК. Система NDC, NDD, NDG
Стадия Лист Листов
Р 2
АКЦИОНЕРНОЕ ОБЩЕСТВО ТЕХЭНЕРГОПРОЕКТ
Формат А2х3