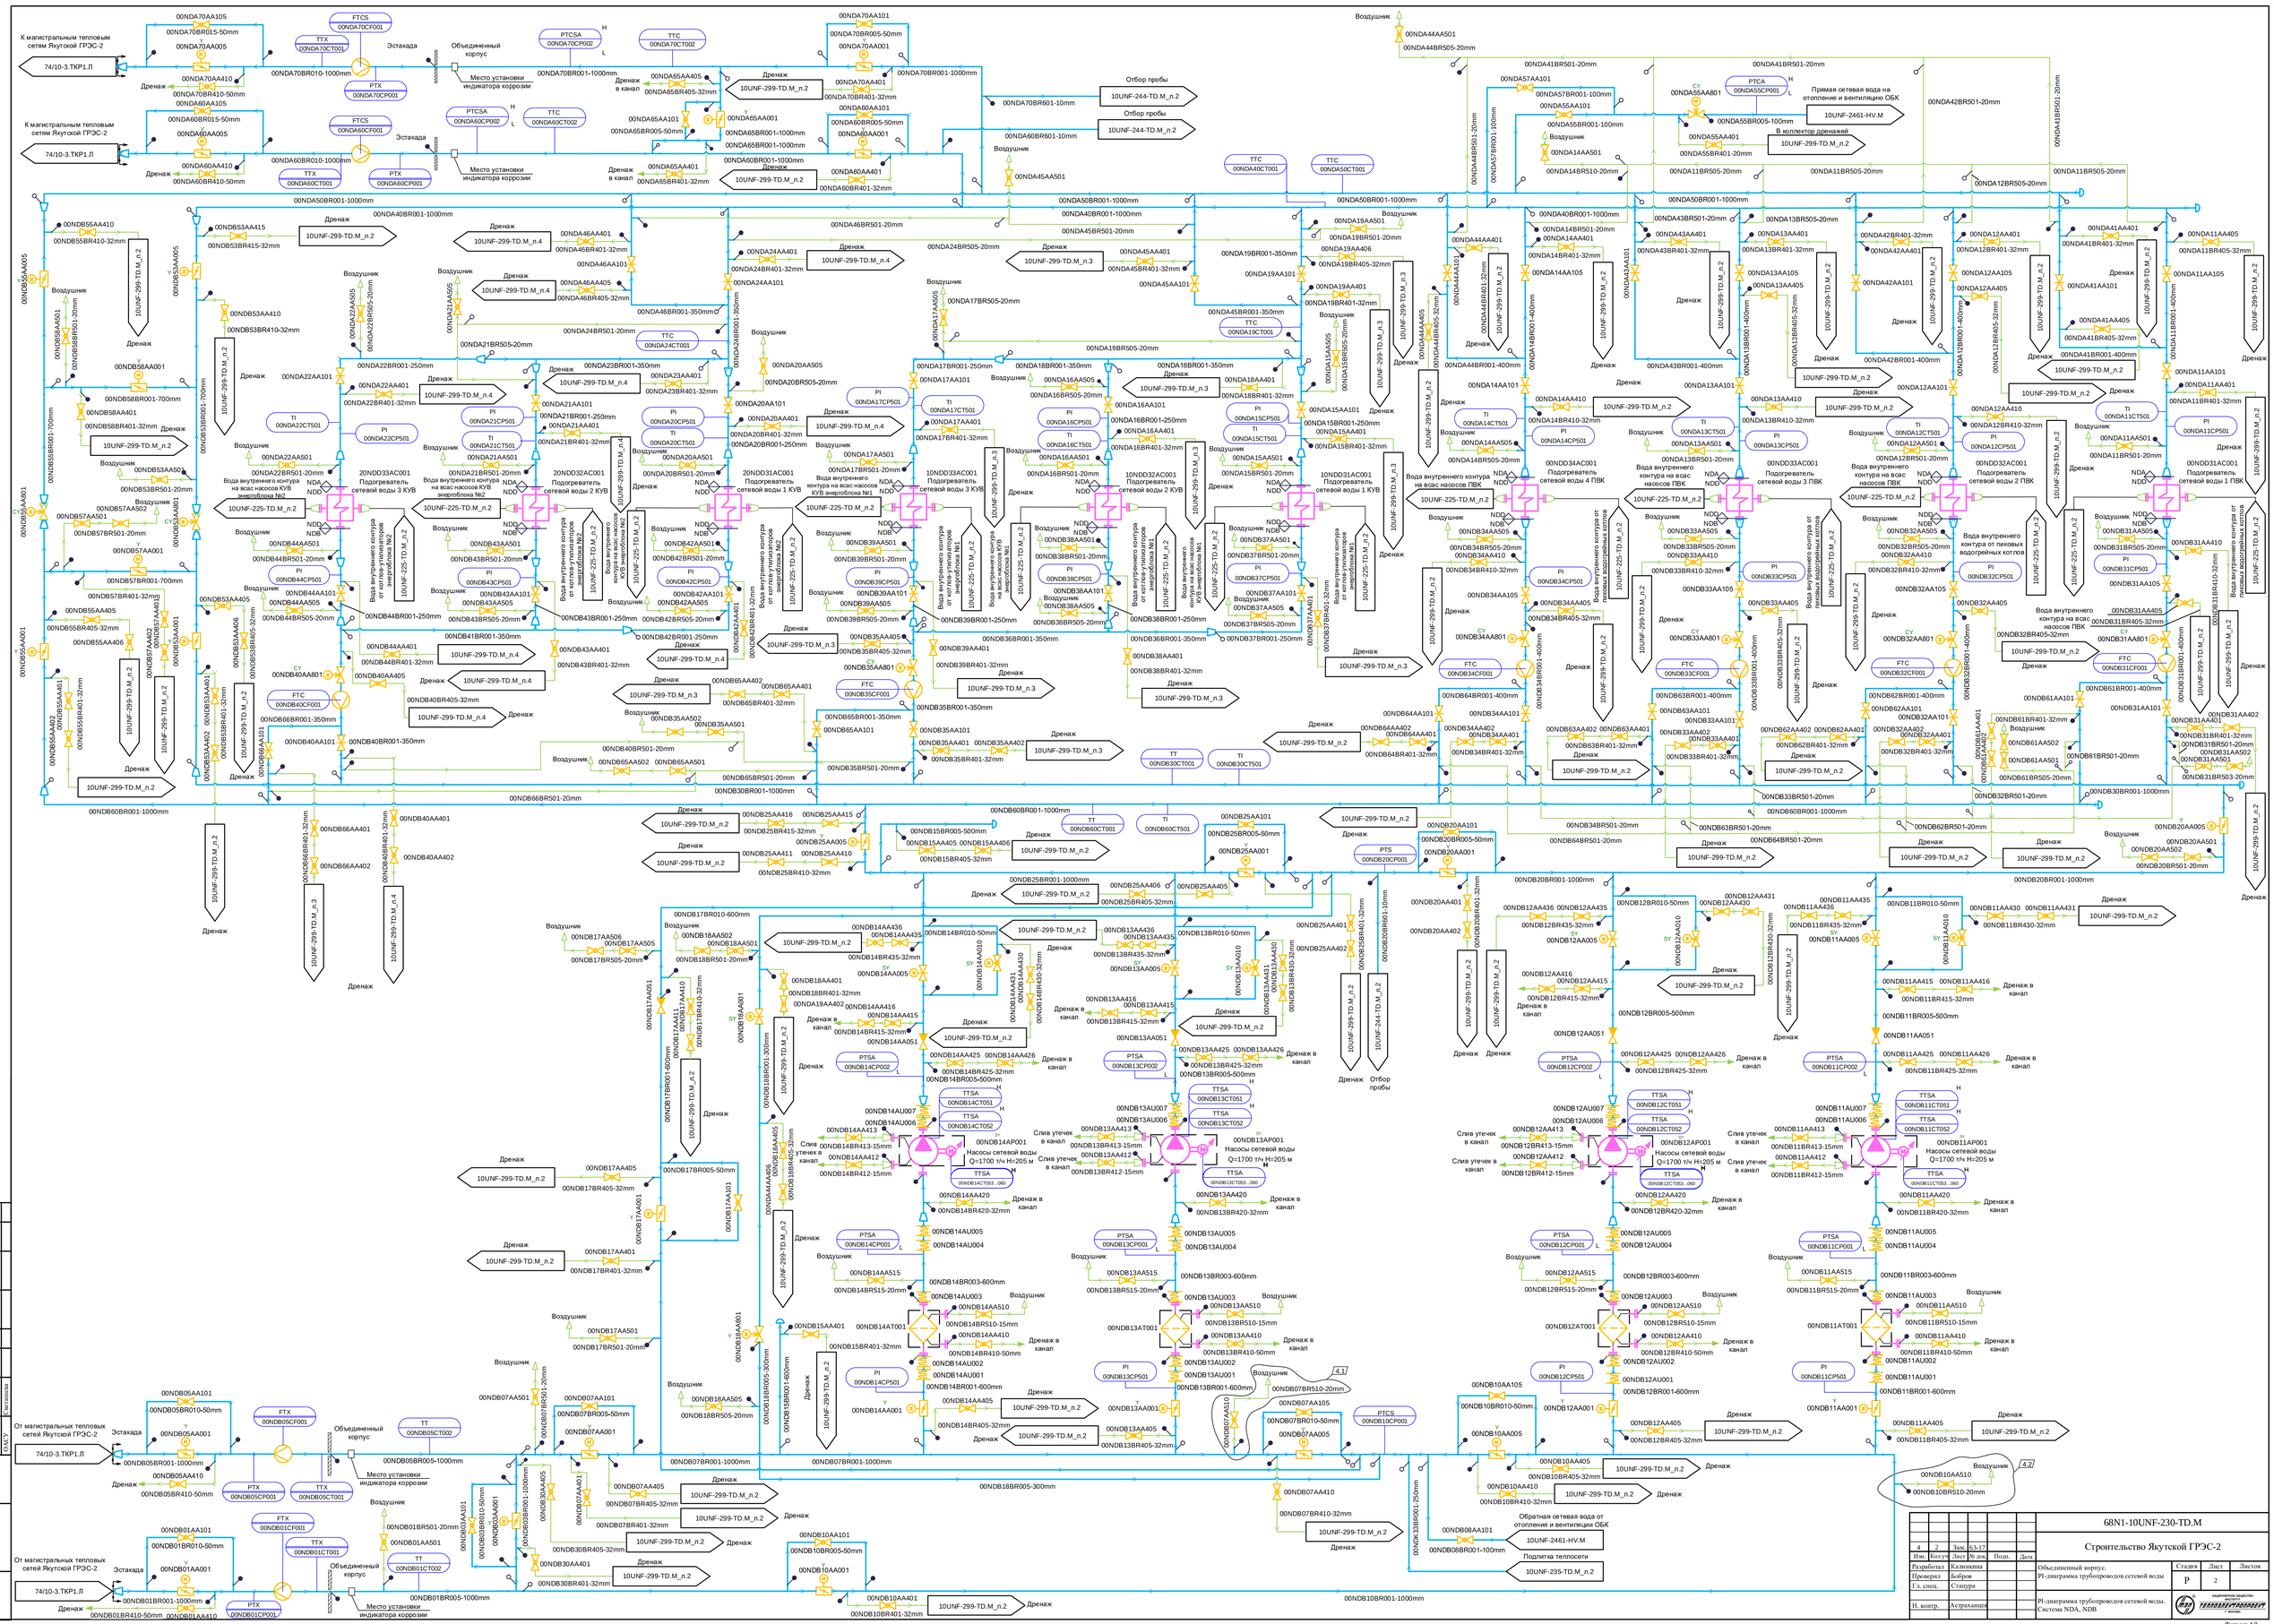

4	2	Зам.	63-17				
Изм.	Кол.уч	Лист	№ док.	Подп.	Дата		
Разработал	Калинкина					Объединенный корпус.	
Проверил	Бобров					Р1-диаграмма трубопроводов сетевой воды	
Гл. спец.	Стацура						
Н. контр.	Астраханцев					Р1-диаграмма трубопроводов сетевой воды. Система NDA, NDB	

68N1-10UNF-230-TD.M

Строительство Якутской ГРЭС-2

Стадия	Лист	Листов
Р	2	

АКЦИОНЕРНОЕ ОБЩЕСТВО ТЕХНОЭКСПОРТСТРОЙ

Согласовано

ОАСУ

Взам. инв. №

Подпись и дата

Инв. № подл.

Формат А0