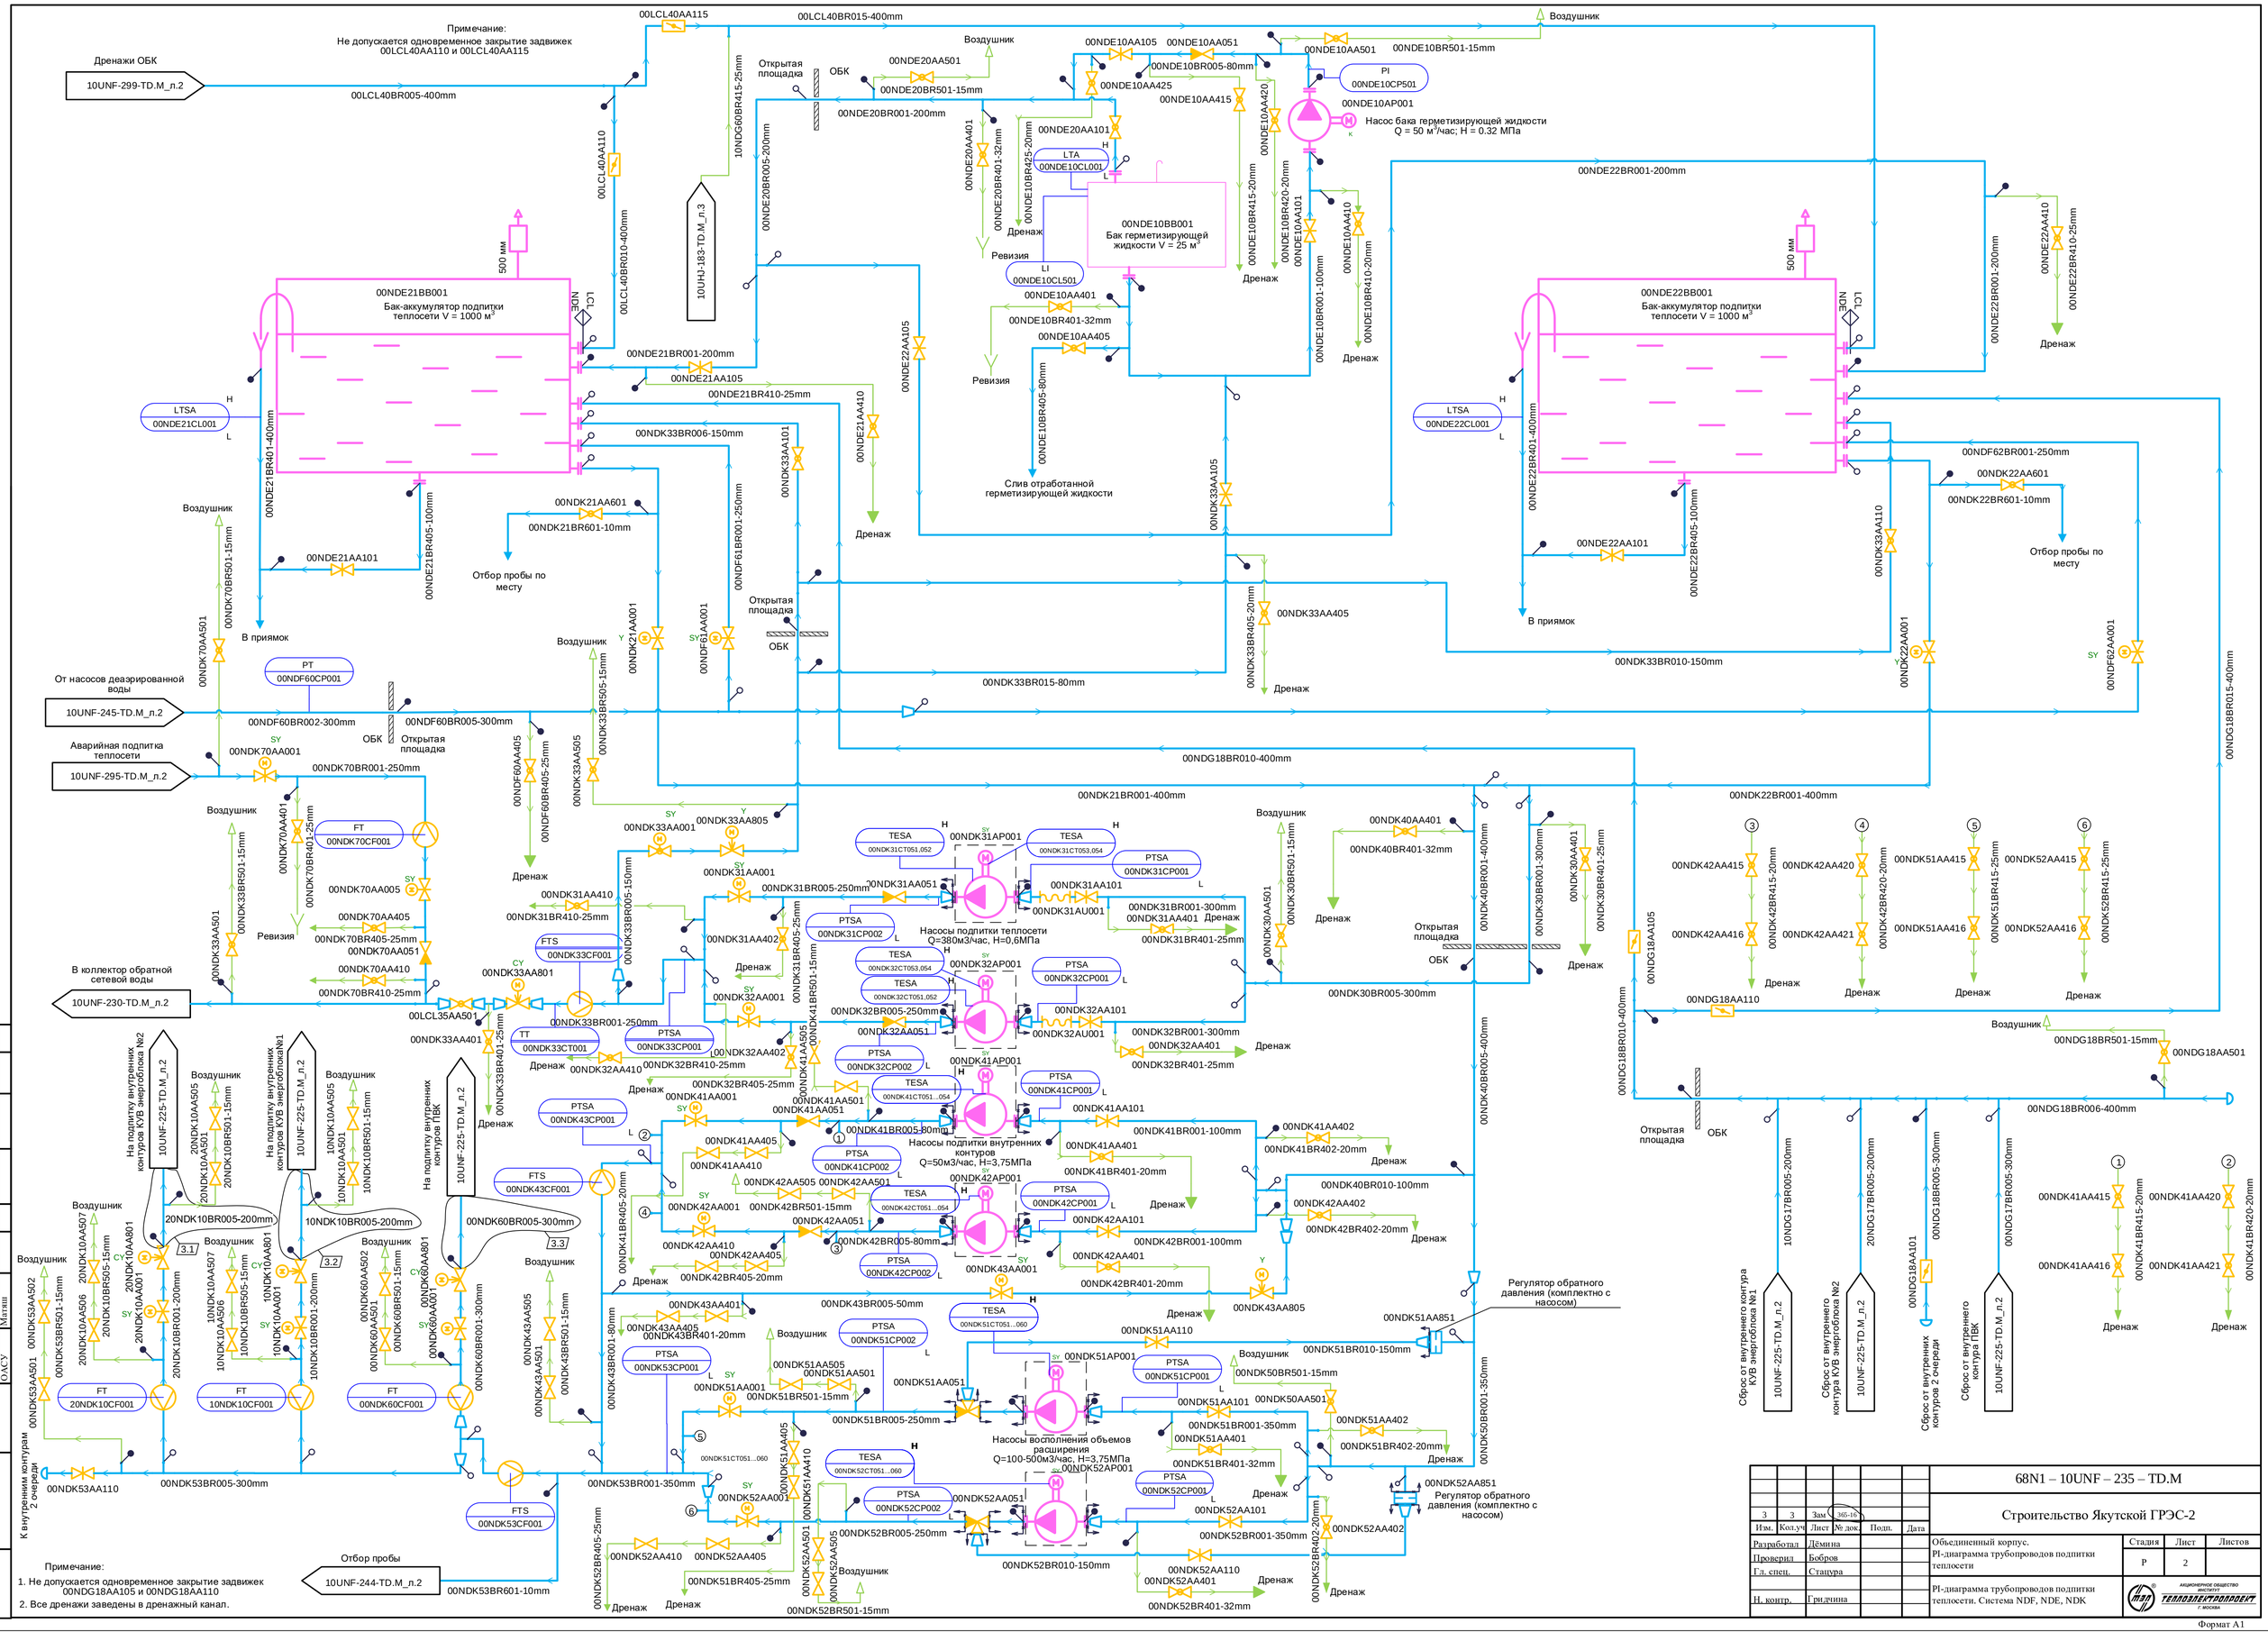

3	3	Зам	365-16				
Изм.	Кол.уч	Лист	№ док.	Подп.	Дата		
Разработал		Дёмина				Объединенный корпус. PI-диаграмма трубопроводов подпитки теплосети	Стадия: Р; Лист: 2; Листов:
Проверил		Бобров					
Гл. спец.		Стацура				PI-диаграмма трубопроводов подпитки теплосети. Система NDF, NDE, NDK	АКЦИОНЕРНОЕ ОБЩЕСТВО ИНСТИТУТ ТЕПЛОЭЛЕКТРОПРОЕКТ Г. МОСКВА
Н. контр.		Грядунна					

68N1 – 10UNF – 235 – TD.M

Строительство Якутской ГРЭС-2

Согласовано

ОАСУ | Магаш

Взам. инв. №

Подпись и дата

Инв. № подл.

Формат А1