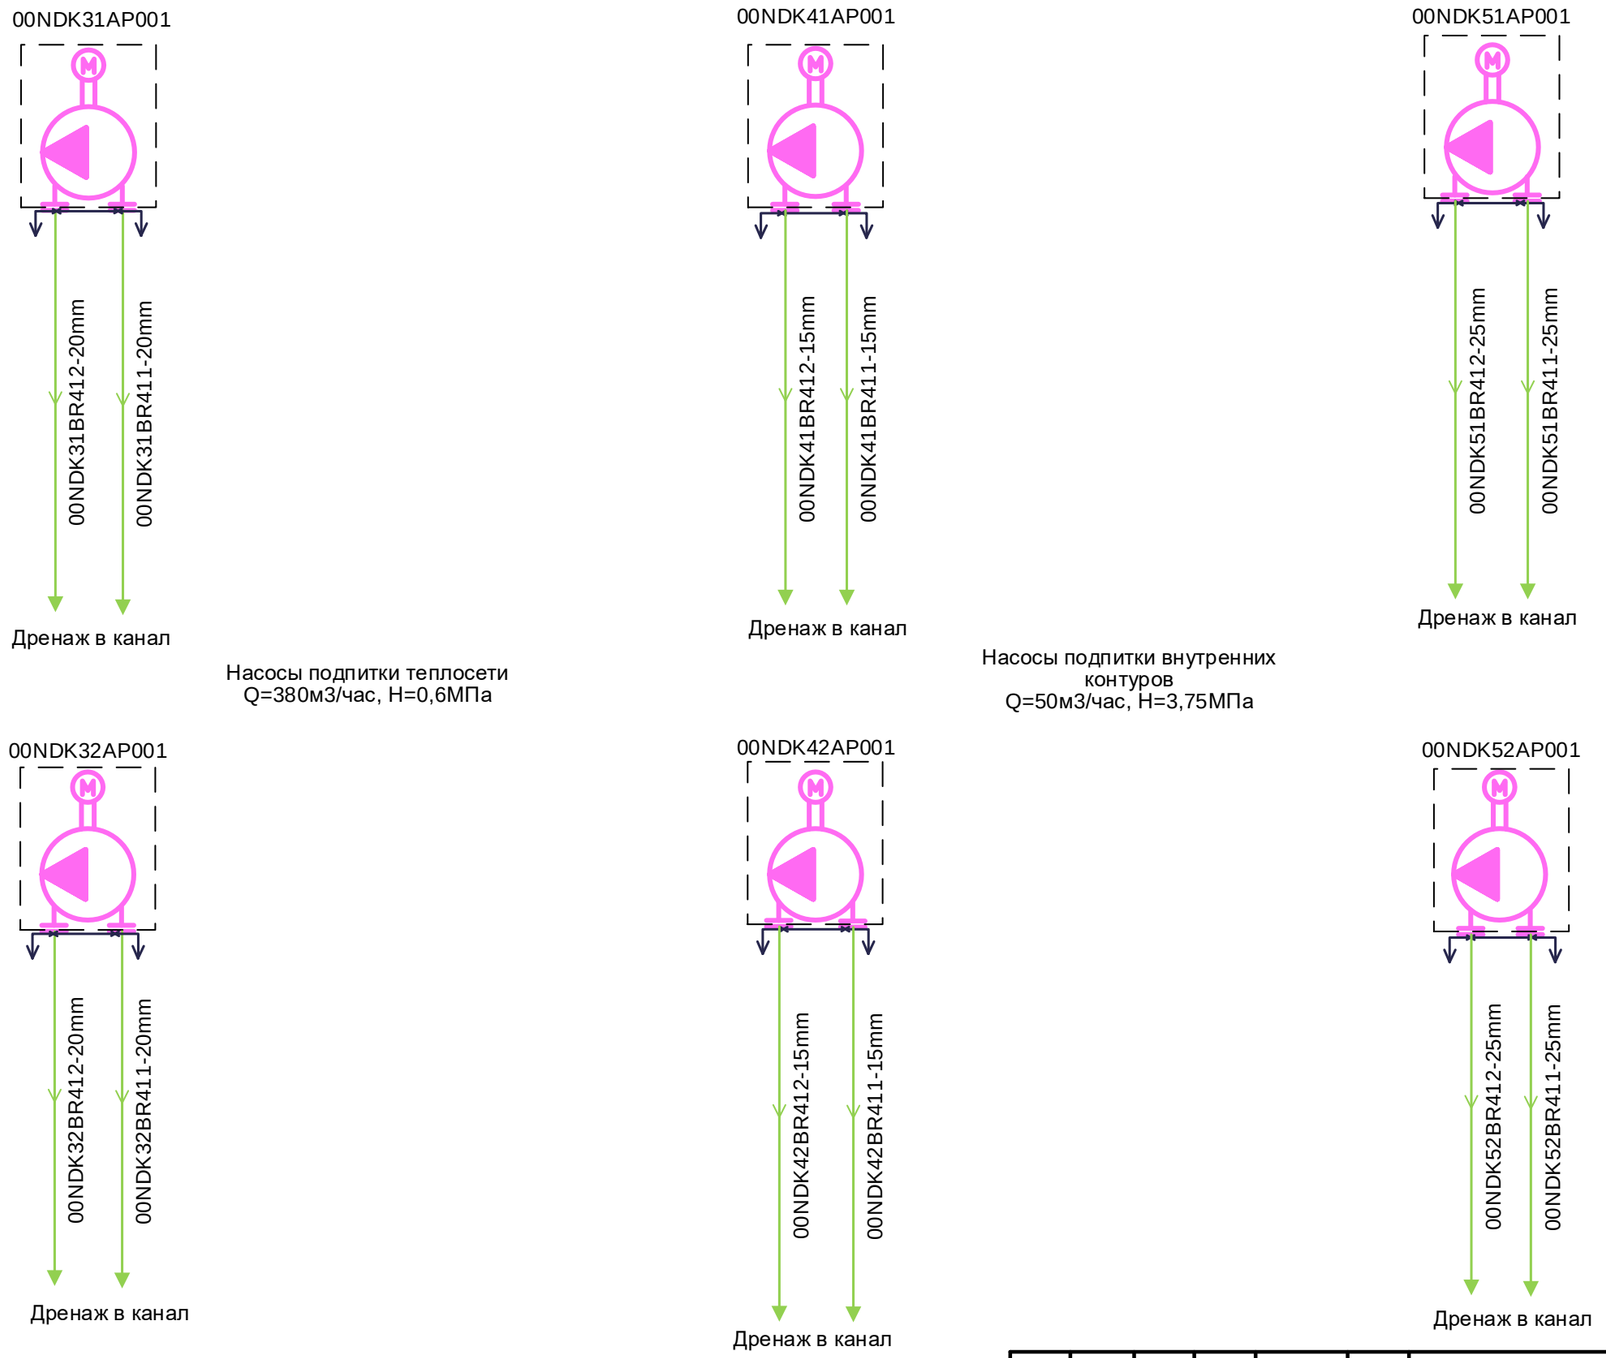

Согласовано

Взам. инв. №

Подпись и дата

Инв. № подл.

Изм.	Кол.уч	Лист	№ док.	Подп.	Дата
Разработал		Дёмина			
Проверил		Бобров			
Гл. спец.		Стацура			
Н. контр.		Астраханцев			

68N1 – 10UNF – 235 – TD.M

Строительство Якутской ГРЭС-2

Объединенный корпус.
PI-диаграмма трубопроводов подпитки теплосети

Стадия	Лист	Листов
Р	3	

PI-диаграмма трубопроводов обвязки насосов подпитки теплосети и внутренних контуров. Система NDK

АКЦИОНЕРНОЕ ОБЩЕСТВО ИНСТИТУТ ТЕПЛОЭЛЕКТРОПРОЕКТ Г. МОСКВА

Формат А3