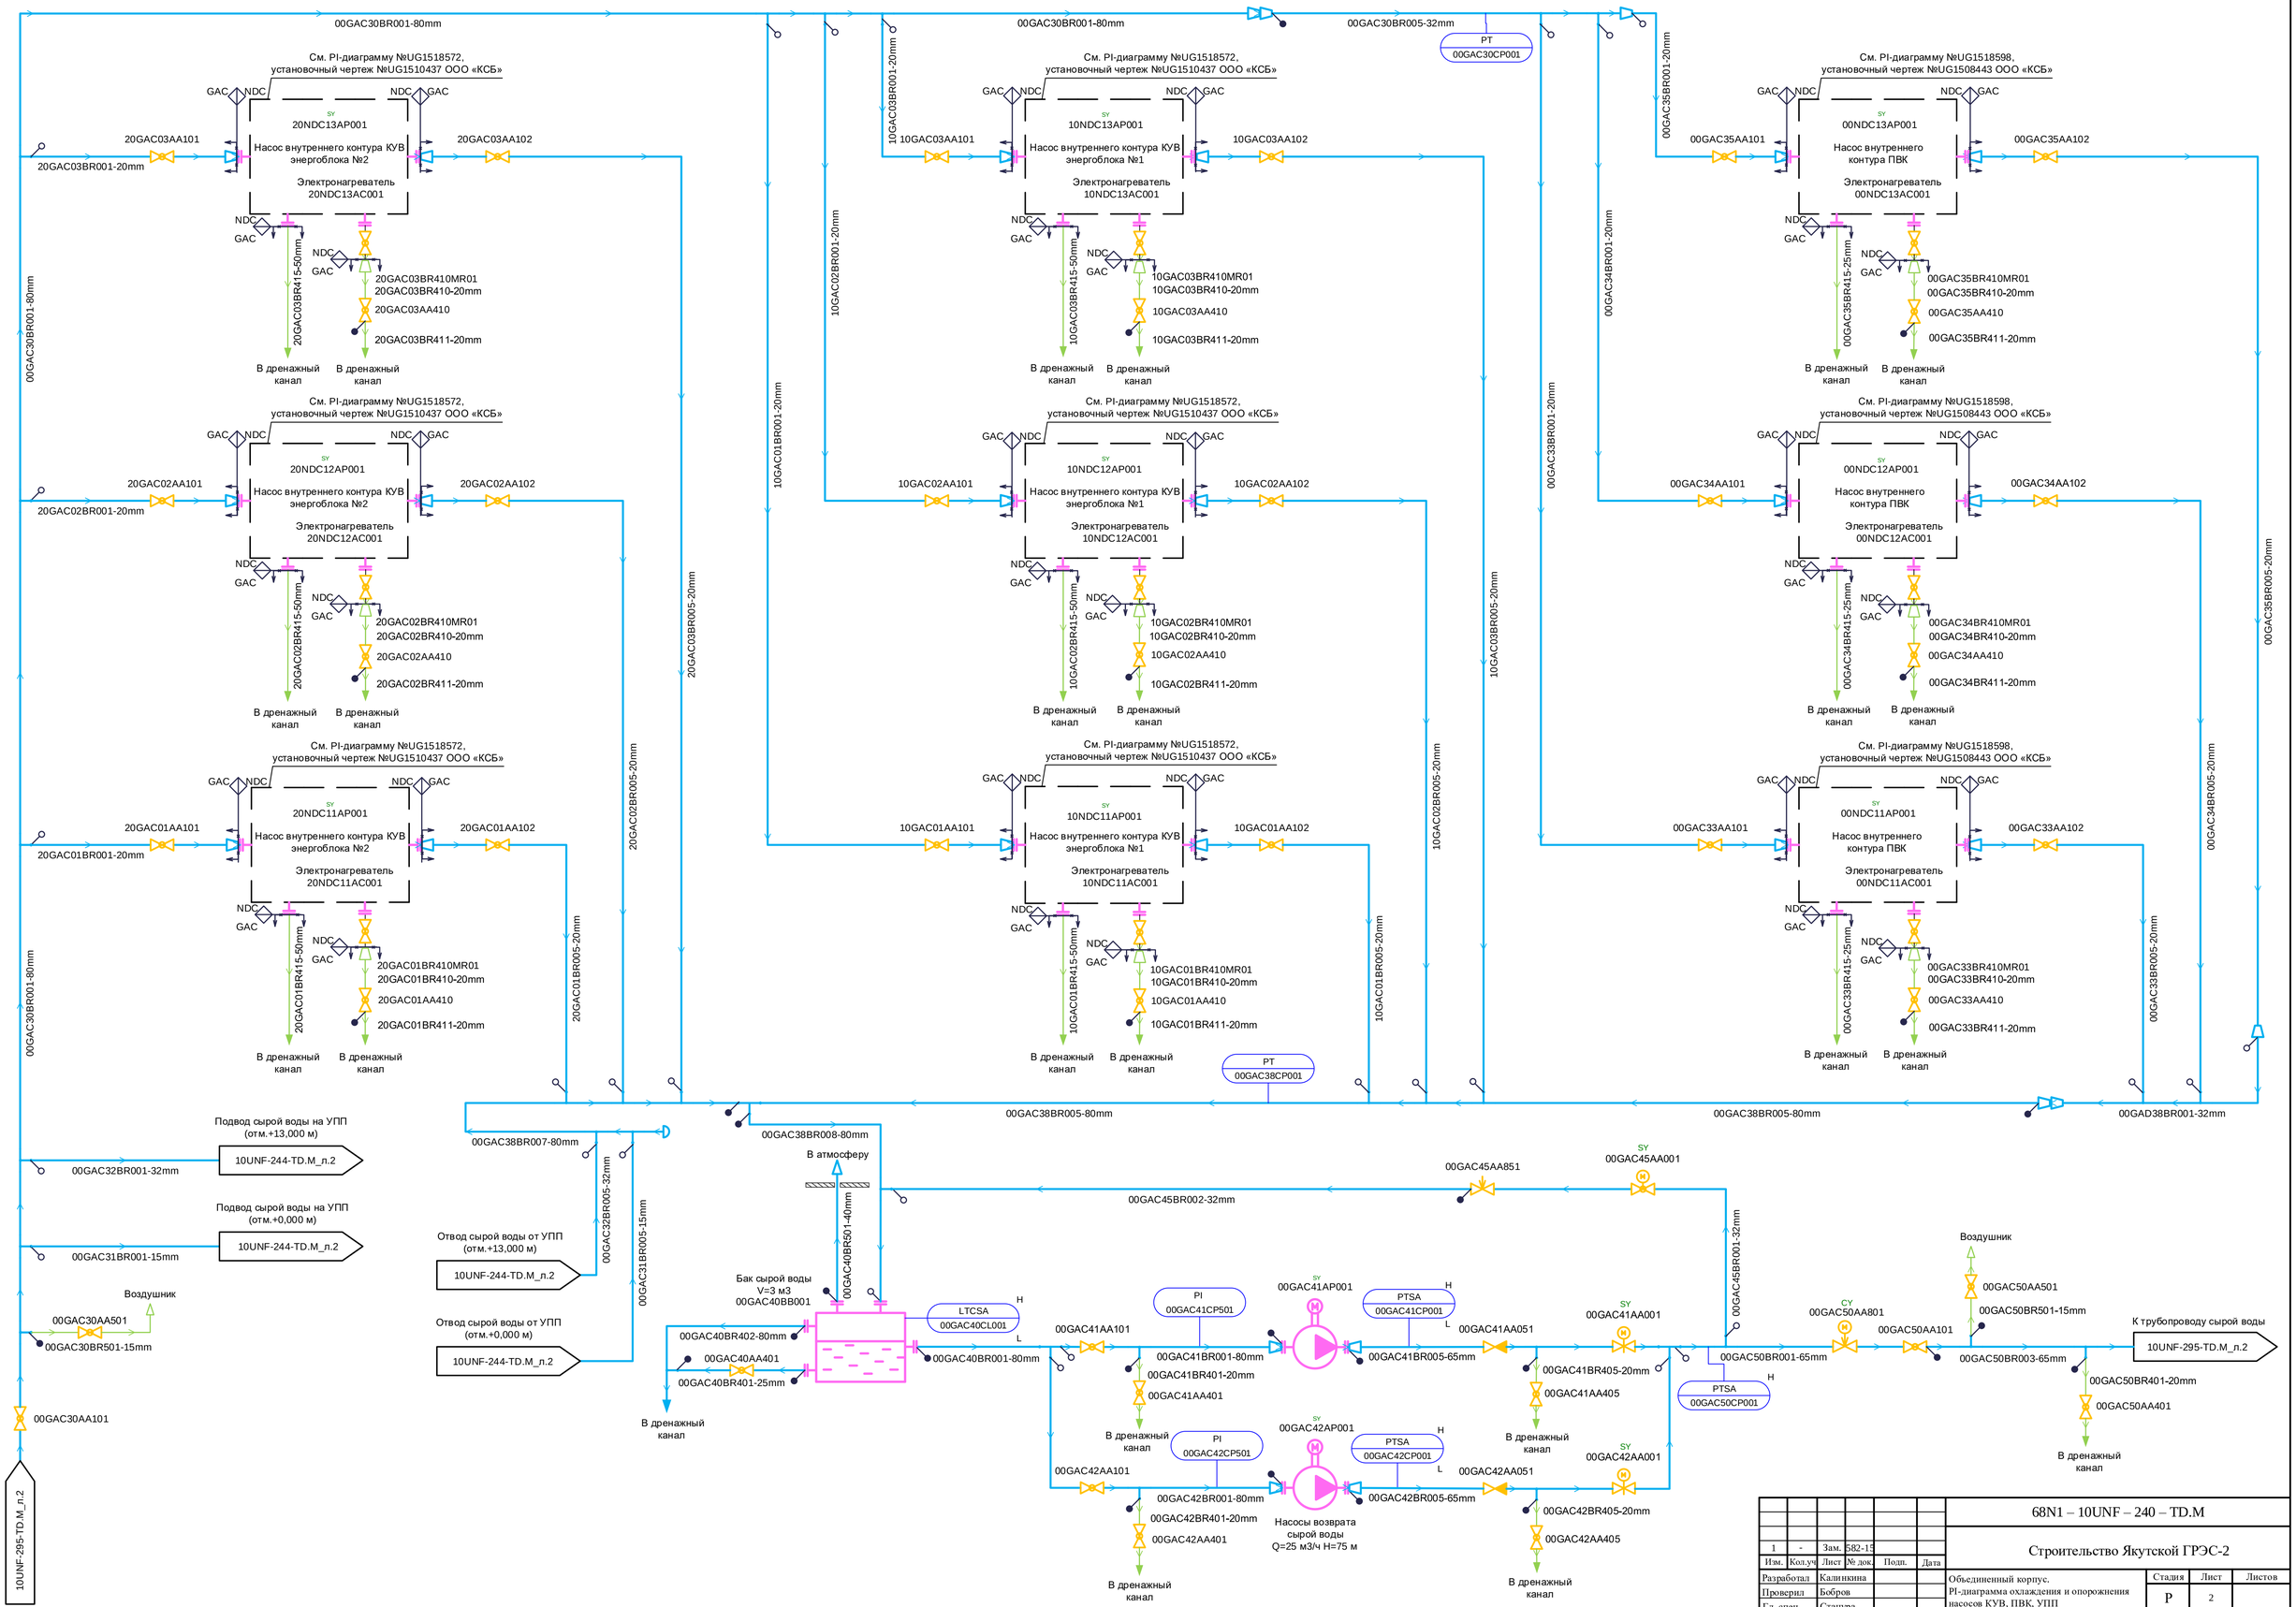

1	-	Зам.	582-15			68N1 – 10UNF – 240 – TD.M
Изм.	Кол.уч	Лист	№ док.	Подп.	Дата	Строительство Якутской ГРЭС-2
Разработал		Калинкина				Объединенный корпус. PI-диаграмма охлаждения и опорожнения насосов КУВ, ПВК, УПП — Стадия: Р; Лист: 2; Листов:
Проверил		Бобров				
Гл. спец.		Стацура				
Н. контр.		Астраханцев				PI-диаграмма охлаждения и опорожнения насосов КУВ, ПВК, УПП. Система GAC

Акционерное общество «Институт Теплоэлектропроект» г. Москва

Согласовано: ОАСУ, Светлакова

Взам. инв. №

Подпись и дата

Инв. № подл.

Формат А1