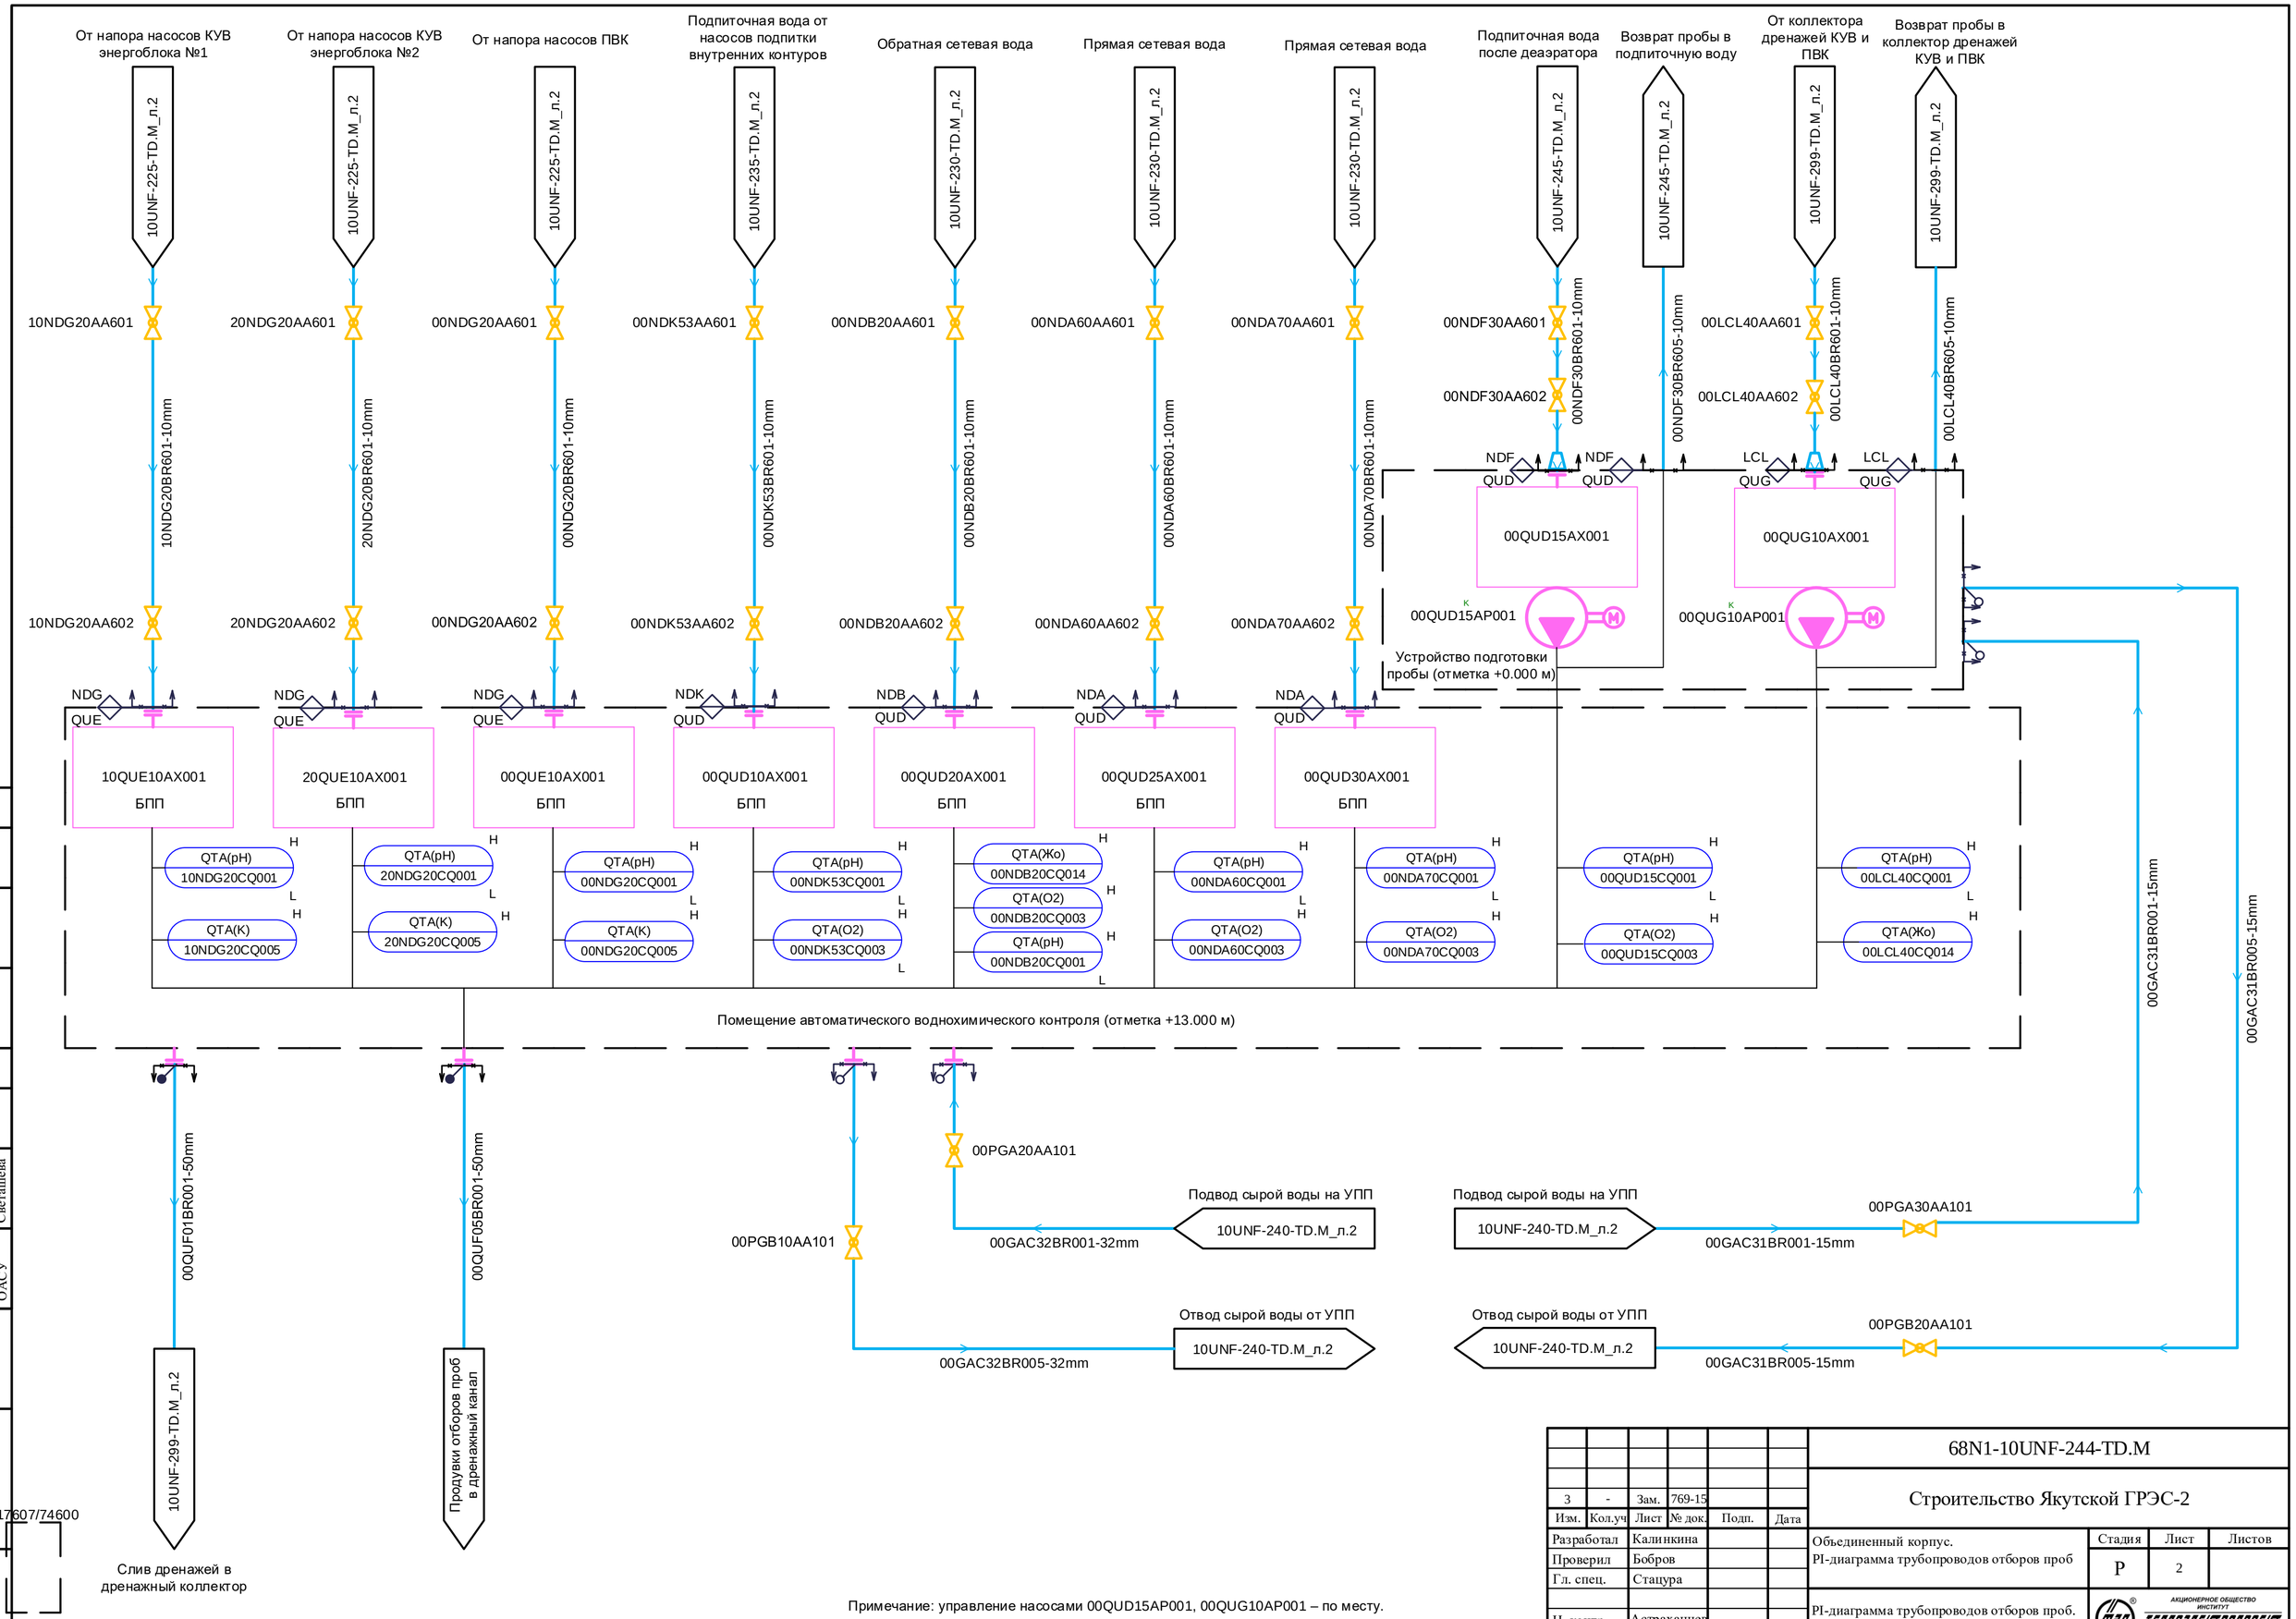

Примечание: управление насосами 00QUD15AP001, 00QUG10AP001 – по месту.

3	-	Зам.	769-15			
Изм.	Кол.уч	Лист	№ док.	Подп.	Дата	
Разработал		Калинкина				
Проверил		Бобров				
Гл. спец.		Стацура				
Н. контр.		Астраханцев				

68N1-10UNF-244-TD.M

Строительство Якутской ГРЭС-2

Объединенный корпус.
PI-диаграмма трубопроводов отборов проб

Стадия	Лист	Листов
Р	2	

PI-диаграмма трубопроводов отборов проб.
Система QU, GAC

АКЦИОНЕРНОЕ ОБЩЕСТВО ИНСТИТУТ ТЕПЛОЭЛЕКТРОПРОЕКТ г. МОСКВА

Согласовано
ОАСУ Светашева

Взам. инв. №
Подпись и дата
Инв. № подл.
=17607/74600

Формат А2