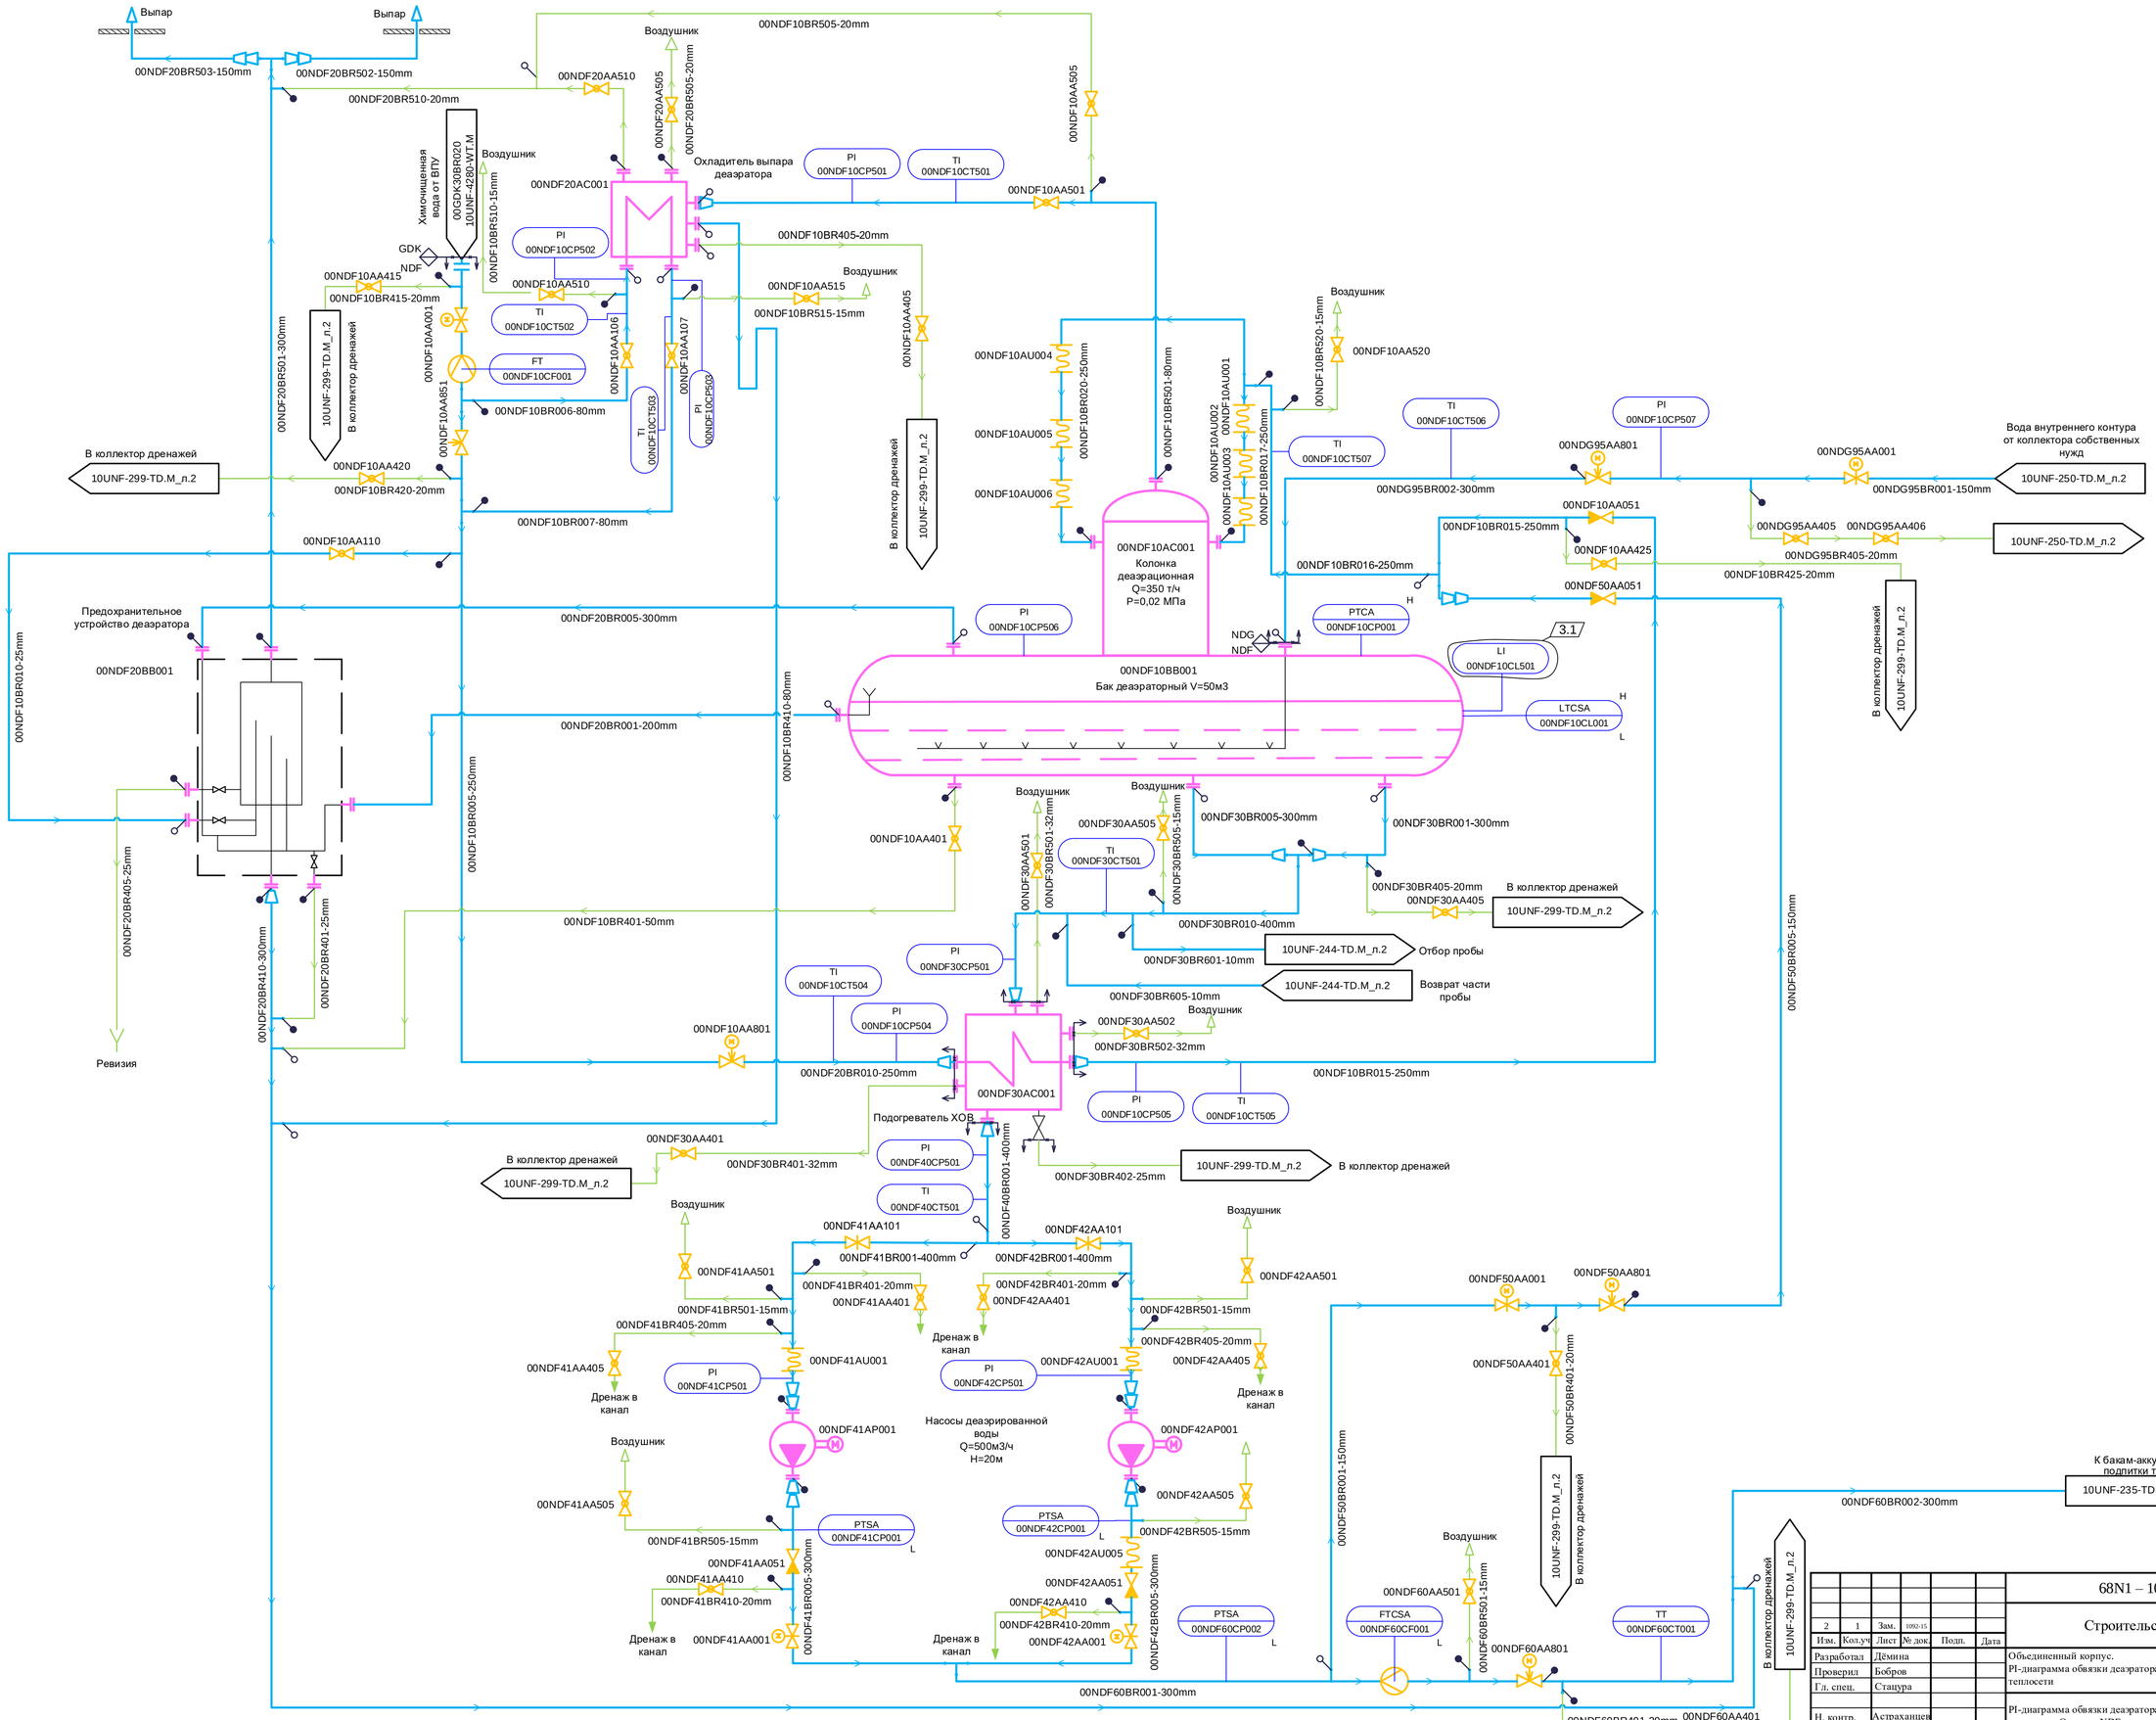

2	1	Зам.	1092-15			
Изм.	Кол.уч	Лист	№ док.	Подп.	Дата	
Разработал		Дёмина				
Проверил		Бобров				
Гл. спец.		Стацура				
Н. контр.		Астраханцев				

68N1 – 10UNF – 245 – TD.M

Строительство Якутской ГРЭС-2

Объединенный корпус.
PI-диаграмма обвязки деаэратора подпитки теплосети

Стадия	Лист	Листов
Р	2	

PI-диаграмма обвязки деаэратора подпитки теплосети. Система NDF

АКЦИОНЕРНОЕ ОБЩЕСТВО ВНИПИЭТ ТЕПЛОЭЛЕКТРОПРОЕКТ г. МОСКВА

Согласовано

Взам. инв. №

Подпись и дата

Инв. № подл.

Формат А1