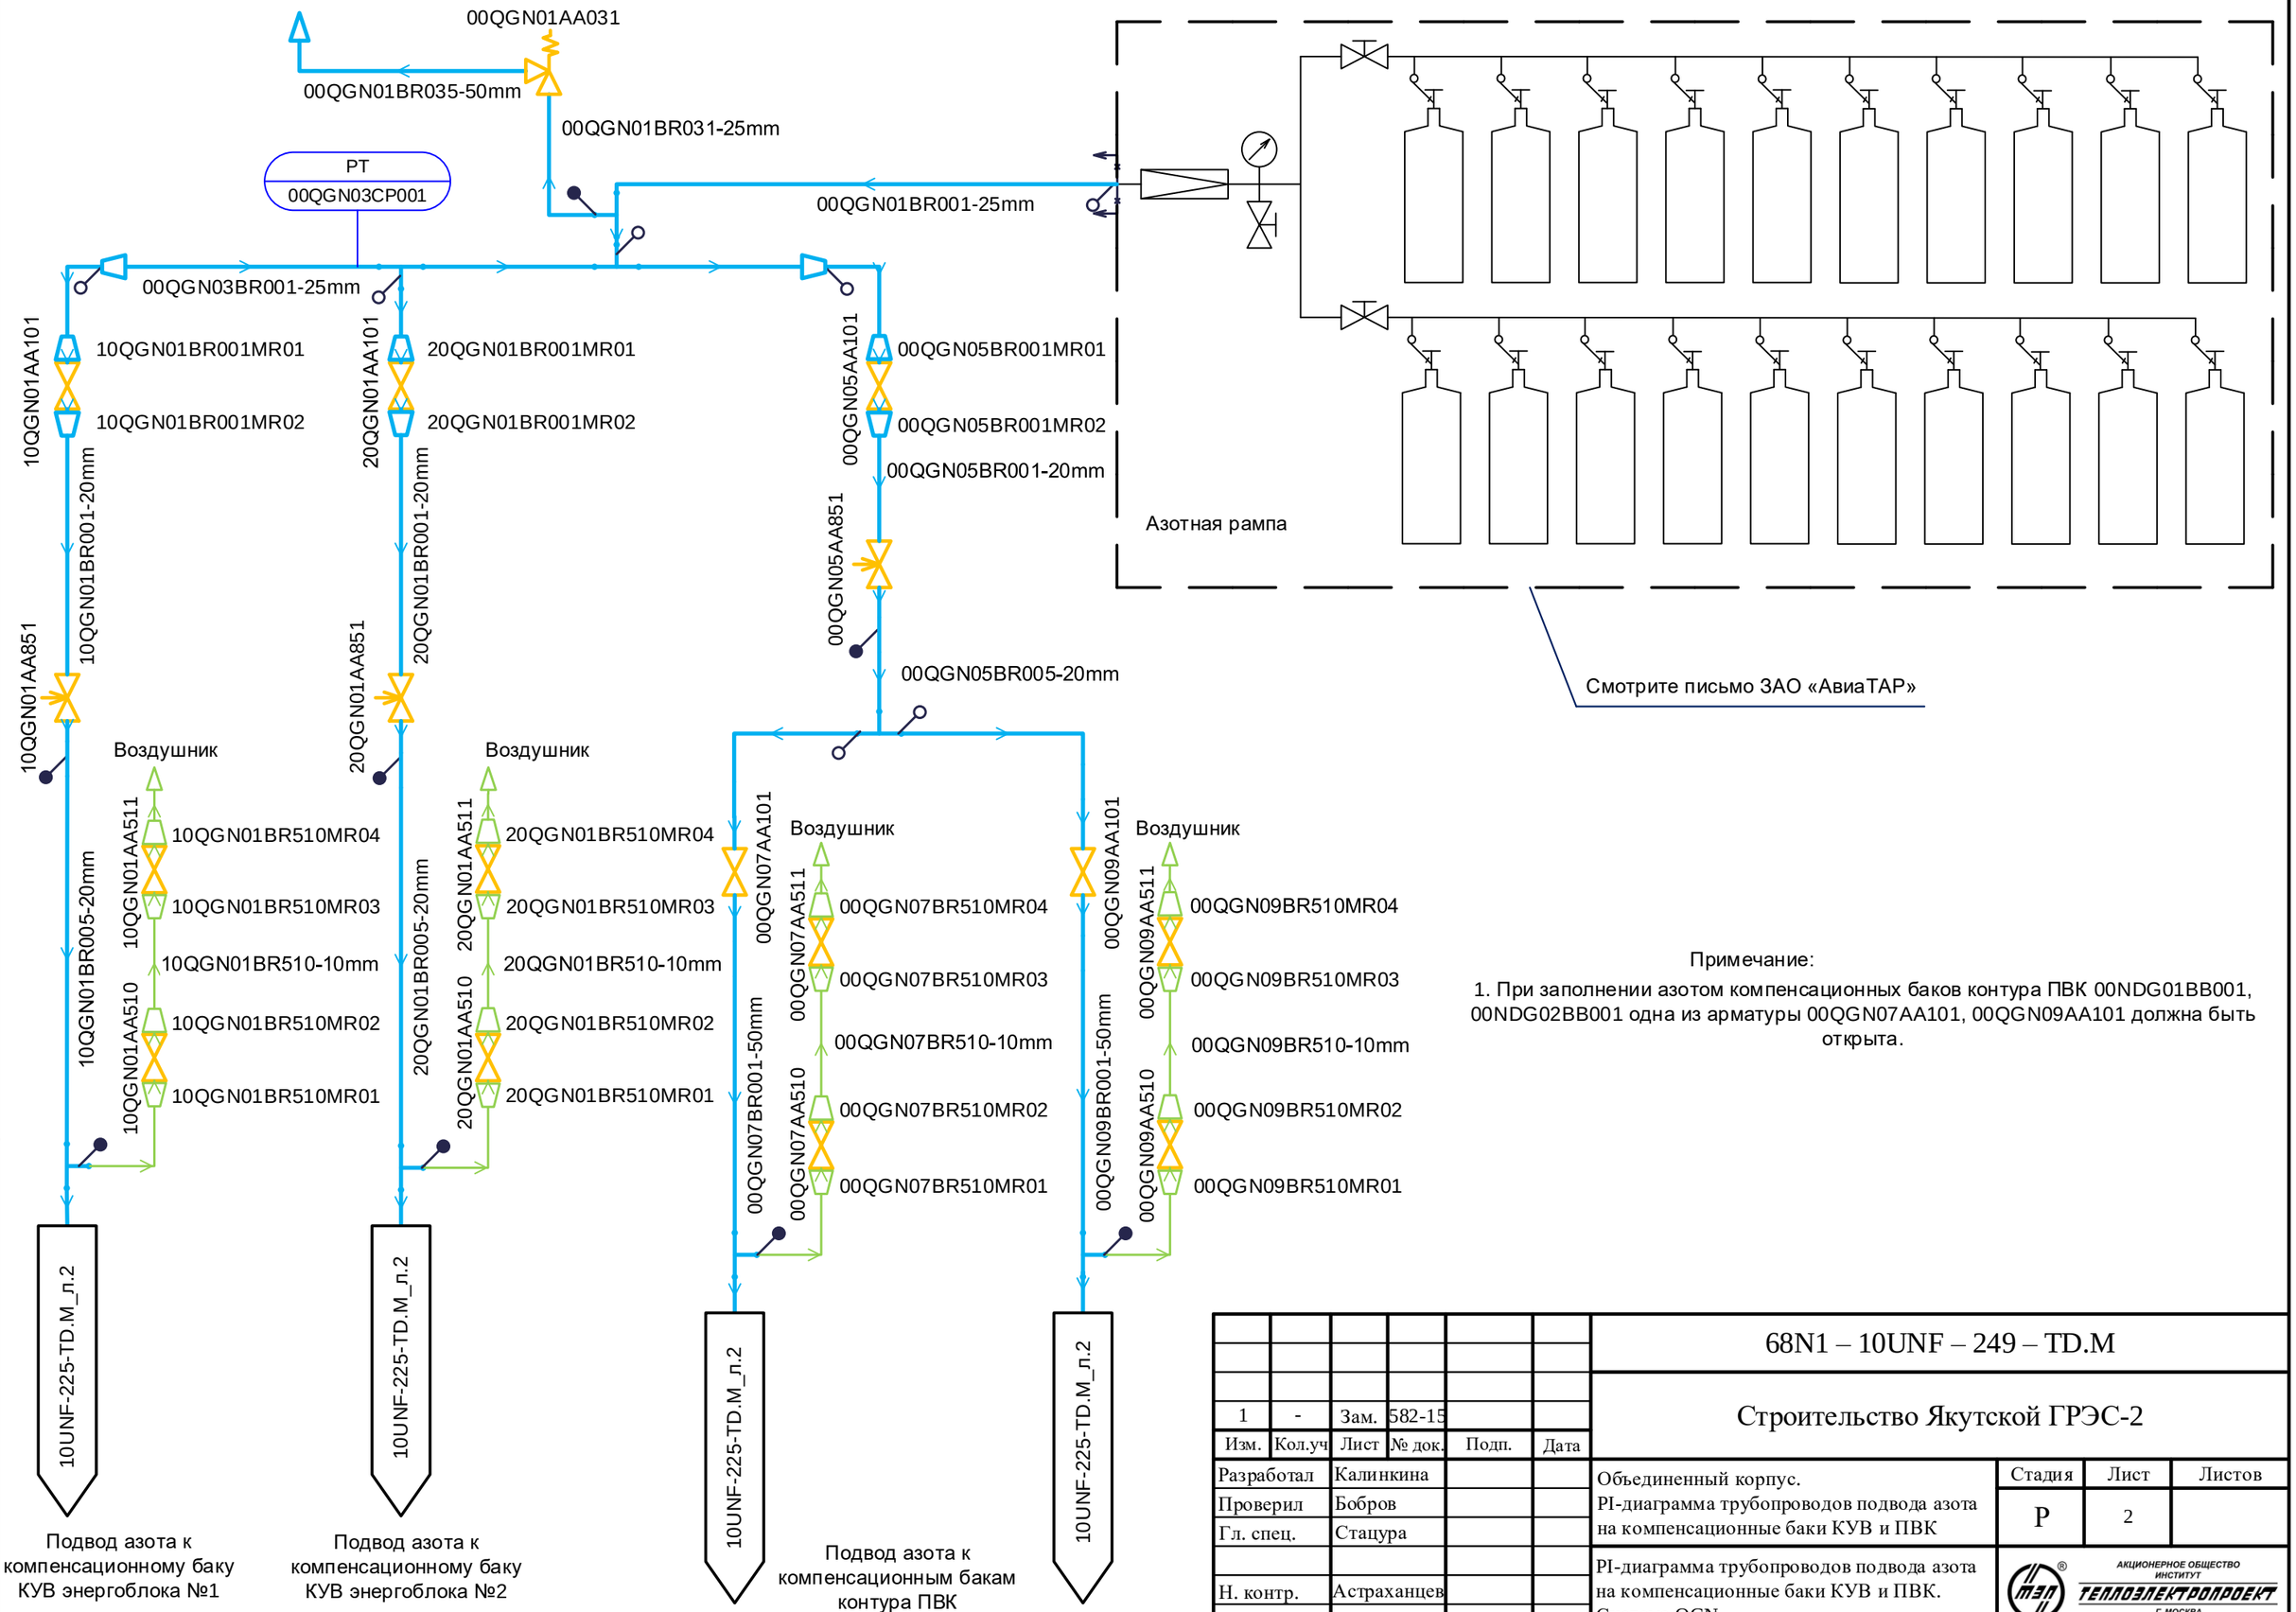

Примечание:

1. При заполнении азотом компенсационных баков контура ПВК 00NDG01BB001, 00NDG02BB001 одна из арматуры 00QGN07AA101, 00QGN09AA101 должна быть открыта.

Изм.	Кол.уч	Лист	№ док.	Подп.	Дата
1	-	Зам.	582-15		

Разработал	Калинкина	
Проверил	Бобров	
Гл. спец.	Стацура	
Н. контр.	Астраханцев	

68N1 – 10UNF – 249 – TD.M

Строительство Якутской ГРЭС-2

Объединенный корпус.
PI-диаграмма трубопроводов подвода азота на компенсационные баки КУВ и ПВК

Стадия	Лист	Листов
Р	2	

PI-диаграмма трубопроводов подвода азота на компенсационные баки КУВ и ПВК. Система QGN

АКЦИОНЕРНОЕ ОБЩЕСТВО ИНСТИТУТ ТЕПЛОЭЛЕКТРОПРОЕКТ г. МОСКВА

Согласовано

ОАСУ Матяш

Взам. инв. №

Подпись и дата

Инв. № подл.

Формат А3