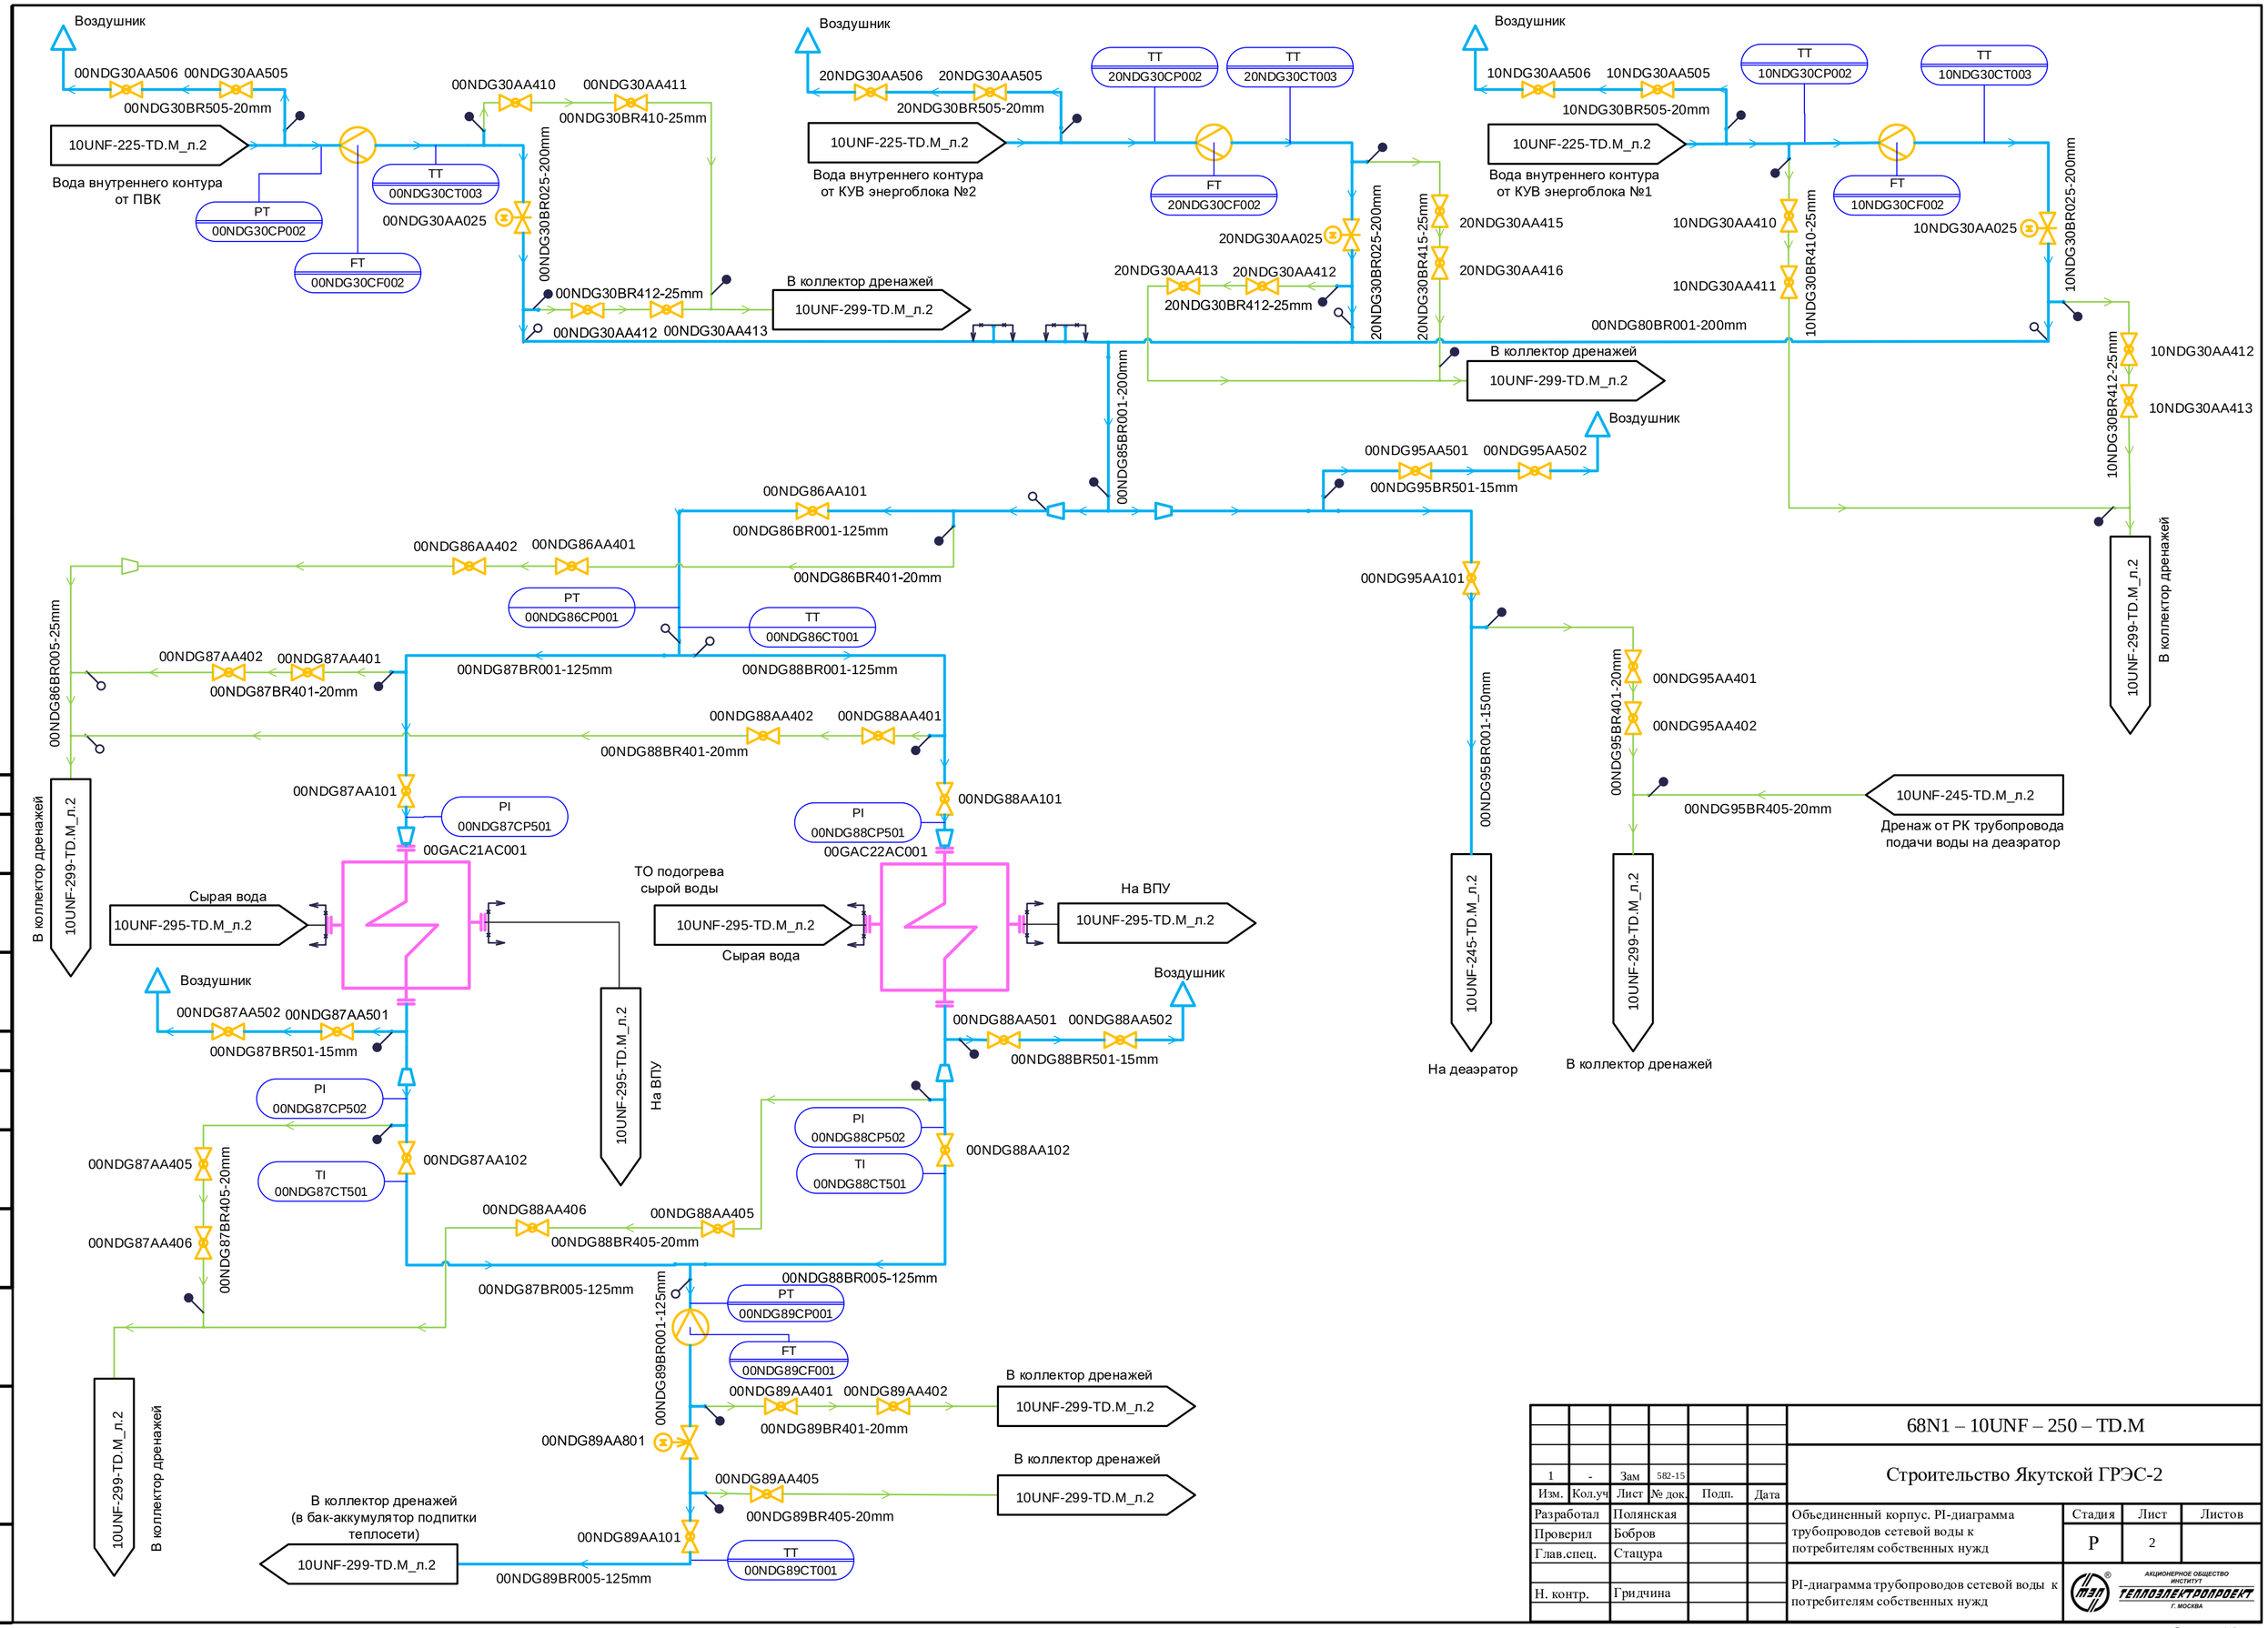

						68N1 – 10UNF – 250 – TD.M			
						Строительство Якутской ГРЭС-2			
1	-	Зам	582-15						
Изм.	Кол.уч	Лист	№ док.	Подп.	Дата				
Разработал		Полянская				Объединенный корпус. PI-диаграмма трубопроводов сетевой воды к потребителям собственных нужд	Стадия	Лист	Листов
Проверил		Бобров					Р	2	
Глав.спец.		Стацура							
Н. контр.		Гридчина				PI-диаграмма трубопроводов сетевой воды к потребителям собственных нужд	АКЦИОНЕРНОЕ ОБЩЕСТВО ИНСТИТУТ ТЕПЛОЭЛЕКТРОПРОЕКТ Г. МОСКВА		

Согласовано

Взам. инв. №

Подпись и дата

Инв. № подл.

Формат А2