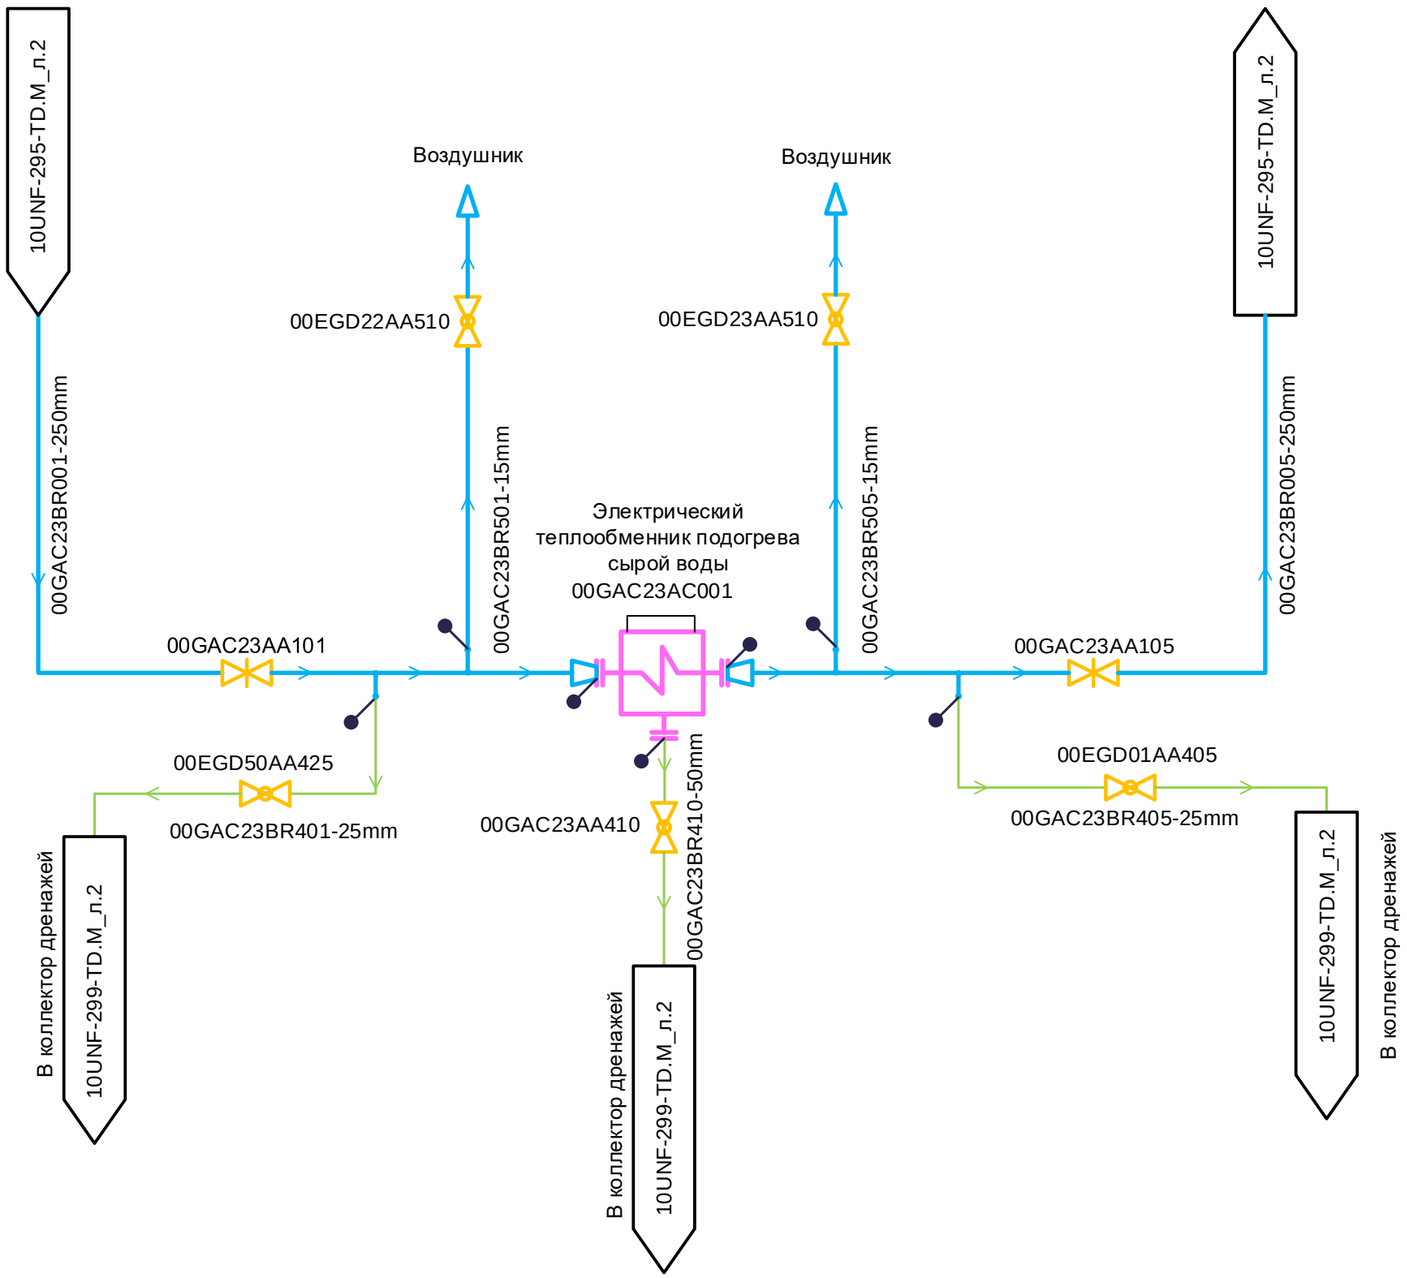

Согласовано

ОАСУ Светашева

Взам. инв. №

Подпись и дата

Инв. № подл.

Изм.	Кол.уч	Лист	№ док.	Подп.	Дата
1	-	Зам.	715-16		

Разработал	Полянская	
Проверил	Бобров	
Гл.спец.	Стацура	
Н. контр.	Гридчина	

68N1 – 10UNF – 2712 – TD.M

Строительство Якутской ГРЭС-2

Объединенный корпус. Трубопроводы подогрева сырой воды. PI-диаграмма

Стадия	Лист	Листов
Р	2	

PI-диаграмма трубопроводов подогрева сырой воды. Система GAC

АКЦИОНЕРНОЕ ОБЩЕСТВО ИНСТИТУТ ТЕПЛОЭЛЕКТРОПРОЕКТ Г. МОСКВА

Формат А3