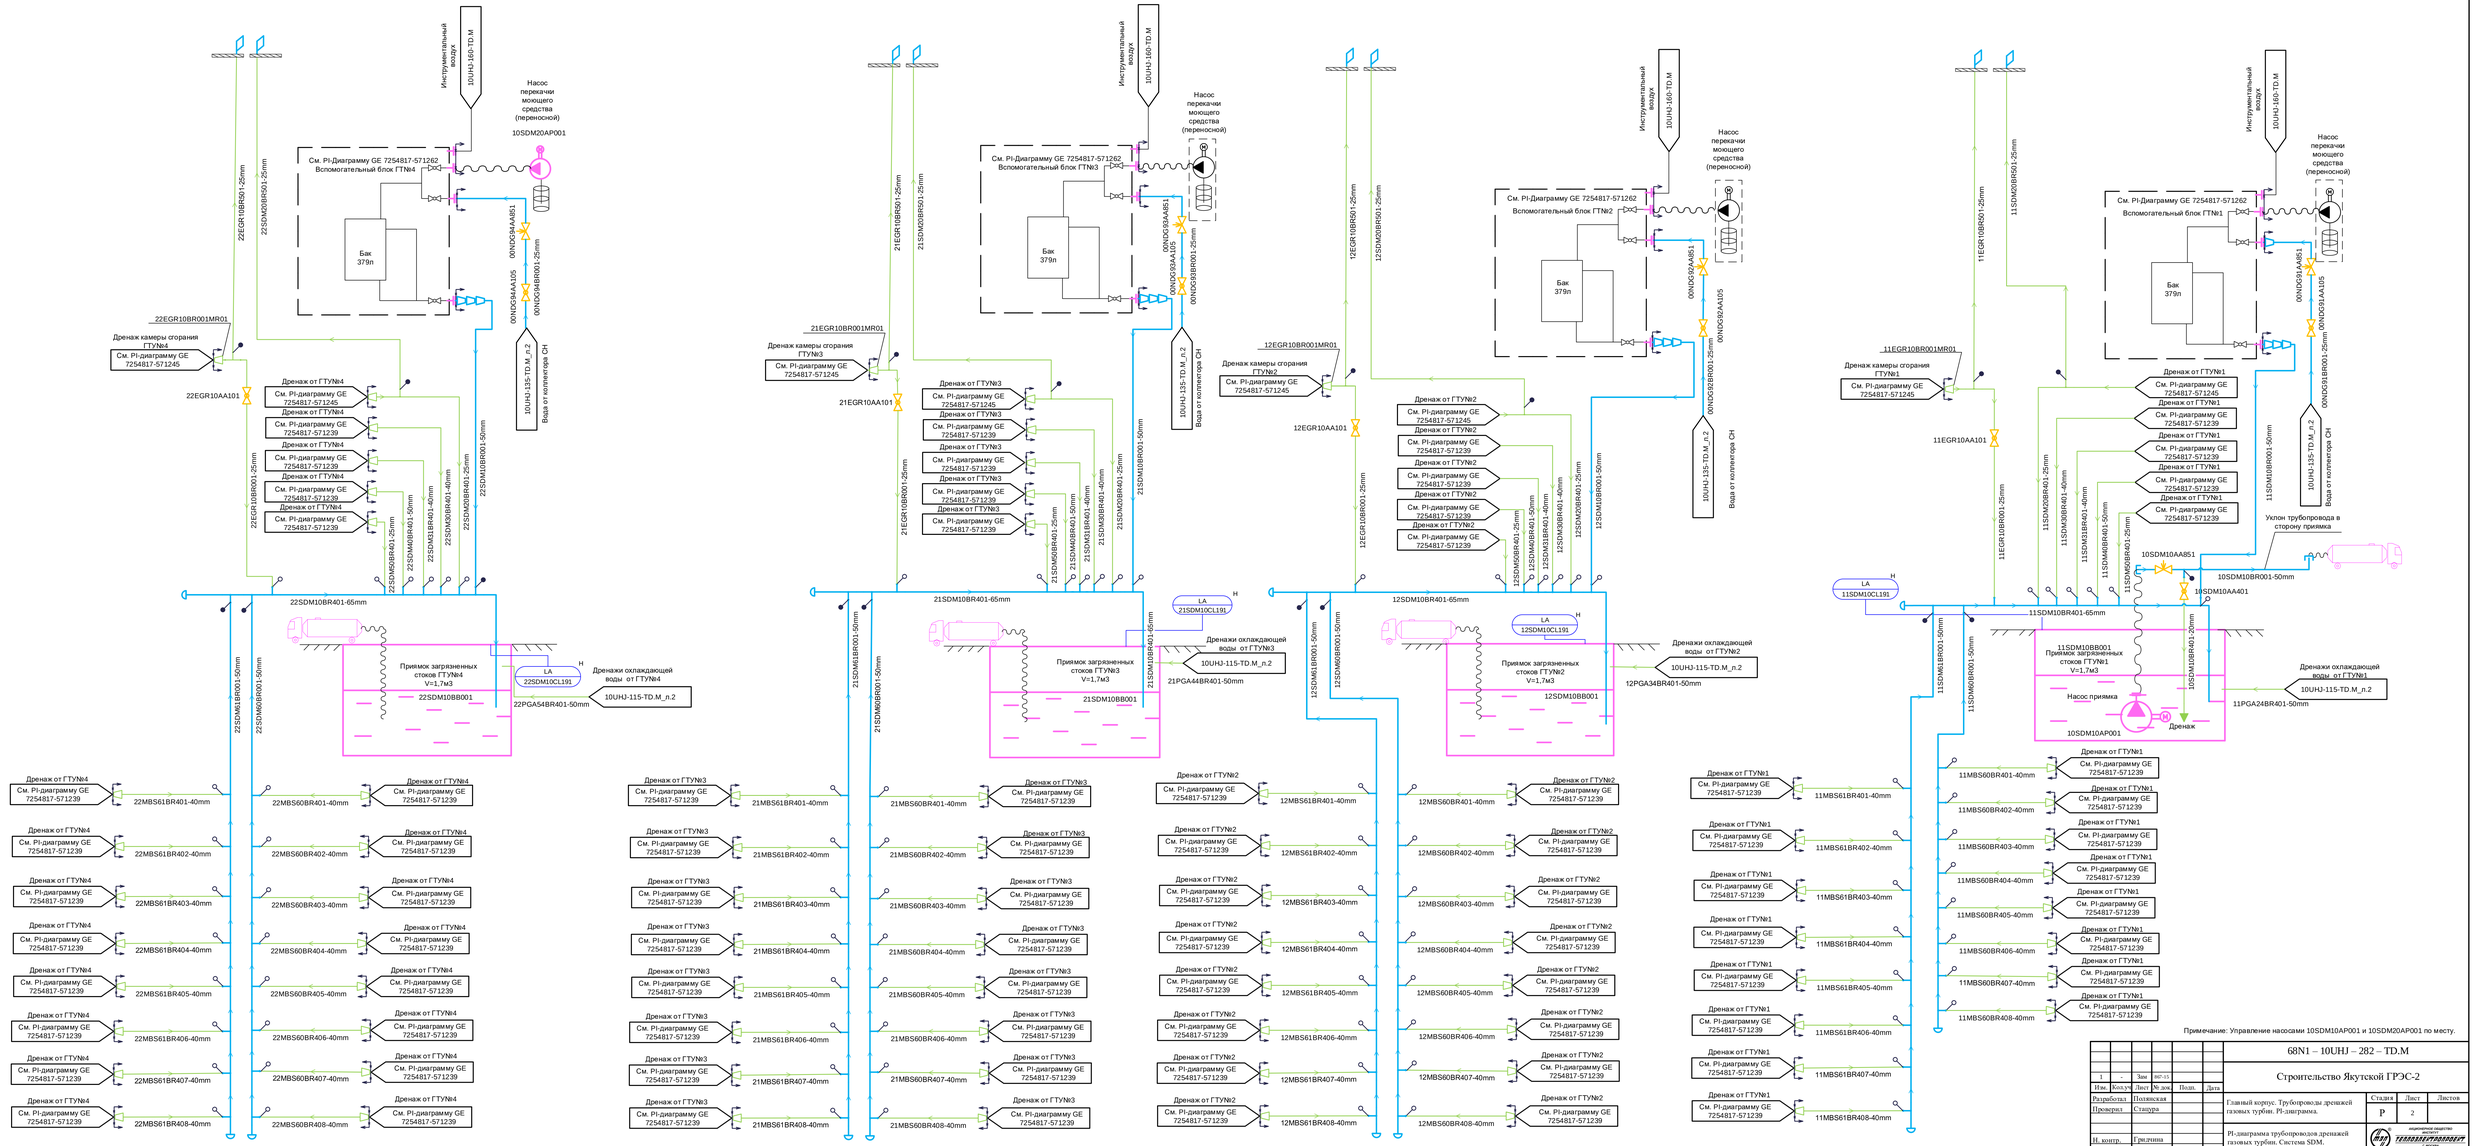

Примечание: Управление насосами 10SDM10AP001 и 10SDM20AP001 по месту.

						68N1 – 10UHJ – 282 – TD.M	
1	-	Зам	ВР-15			Строительство Якутской ГРЭС-2	
Изм.	Кол.уч	Лист	№ док.	Подп.	Дата		
Разработал	Полянская					Главный корпус. Трубопроводы дренажей газовых турбин. PI-диаграмма.	Стадия: Р; Лист: 2; Листов:
Проверил	Сидора						
Н. контр.	Грецкина					PI-диаграммы трубопроводов дренажей газовых турбин. Система SDM.	Федеральное государственное унитарное предприятие «Российский Федеральный Ядерный Центр – ВНИИЭФ»

Согласовано

Взам. инв. №	Подпись и дата	Инв. № подл.

Формат А2х3