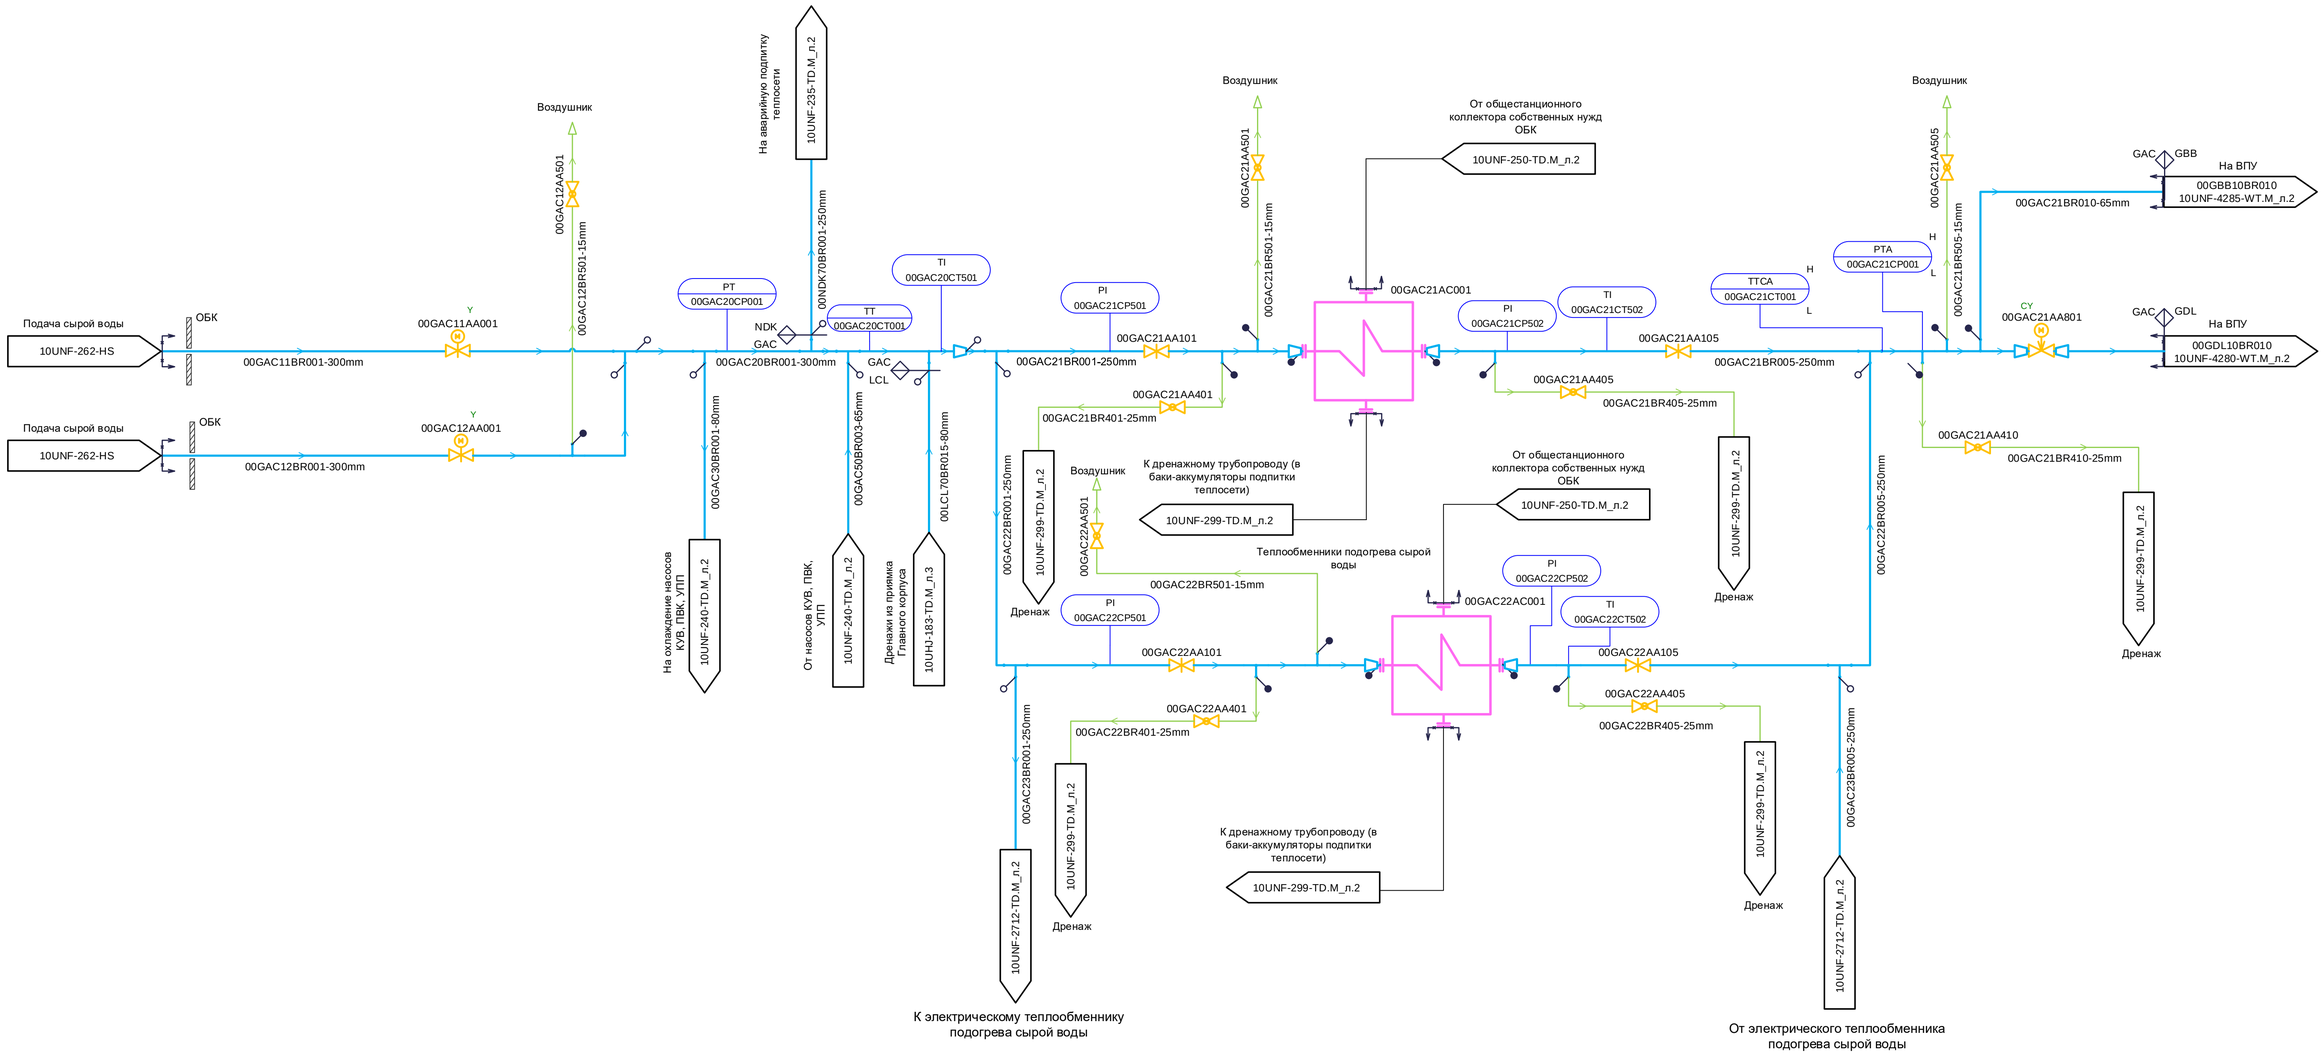

Примечание: 1. Задвижки 00GAC11AA001 И 00GAC12AA001 управляются оператором через ПТК без блокировок.

2. Регулирующий клапан 00GAC21AA801 поддерживает уровень в баке исходной воды 00GDL11CL001, 00GDL12CL001, задание 600см от дна бака, управляется оператором через ПТК.

Изм.	Кол.уч	Лист	№ док.	Подп.	Дата
2	-	Зам.	715-16		

68N1 – 10UNF – 295 – TD.M

Строительство Якутской ГРЭС-2

Разработал	Дёмина		
Проверил	Бобров		
Гл. спец.	Стацура		
Н. контр.	Астраханцев		

Объединенный корпус.
PI-диаграмма трубопроводов сырой воды

Стадия	Лист	Листов
Р	2	

PI-диаграмма трубопроводов сырой воды. Система GAC

АКЦИОНЕРНОЕ ОБЩЕСТВО «ОРГЭНЕРГО» ТЕПЛОЭЛЕКТРОПРОЕКТ Г. МОСКВА

Согласовано

Взам. инв. №

Подпись и дата

Инв. № подл.

Формат А1