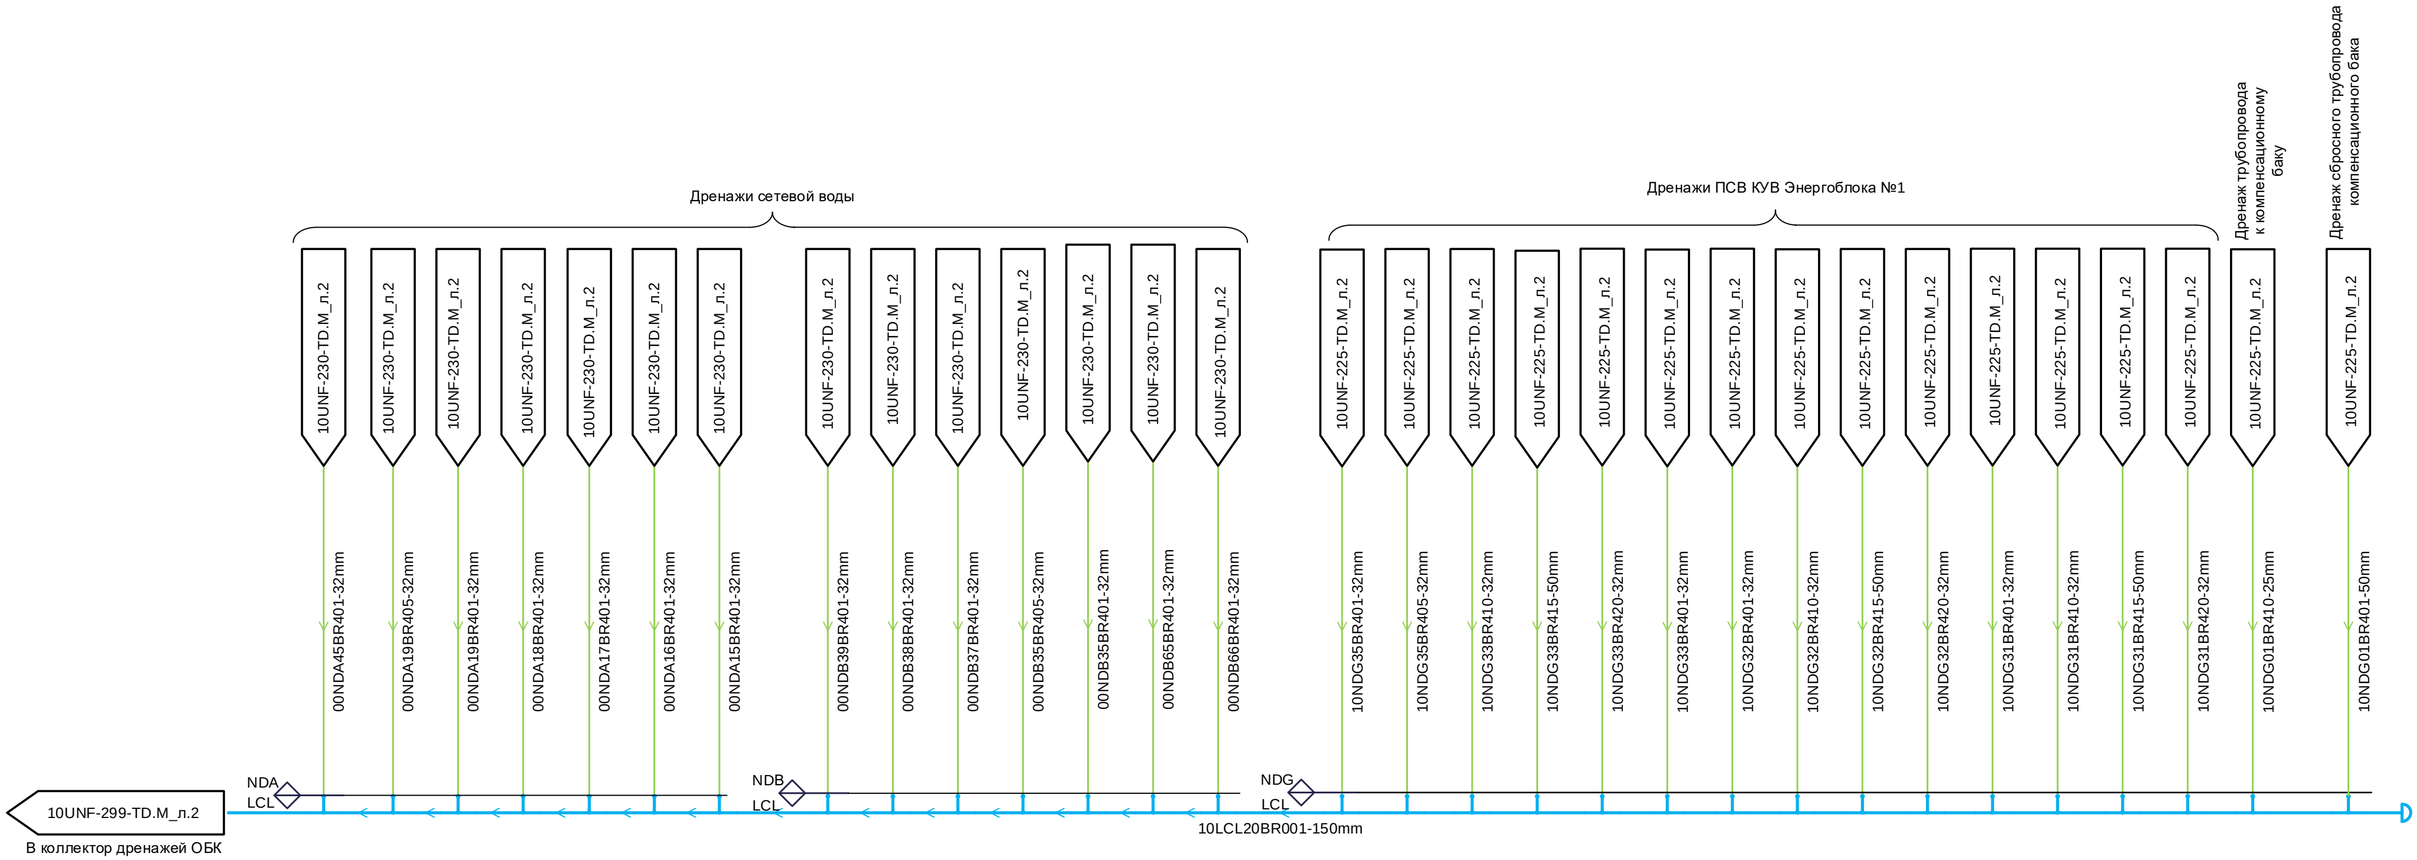

3	-	Зам	864-16			
Изм.	Кол.уч	Лист	№ док.	Подп.	Дата	
Разработал		Полянская				
Проверил		Бобров				
Гл. спец.		Стацура				
Н. контр.		Гридчина				

68N1 – 10UNF – 299 – TD.M

Строительство Якутской ГРЭС-2

Объединенный корпус.
Трубопроводы дренажей КУВ, ПВК.
PI-диаграмма

Стадия	Лист	Листов
Р	3	

PI-диаграмма трубопроводов дренажей ПСВ КУВ Энергоблока №1. Система LCL.

АКЦИОНЕРНОЕ ОБЩЕСТВО ИНСТИТУТ ТЕПЛОЭЛЕКТРОПРОЕКТ Г. МОСКВА

Согласовано

ОАСУ

Взам. инв. №

Подпись и дата

Инв. № подл.

Формат А2