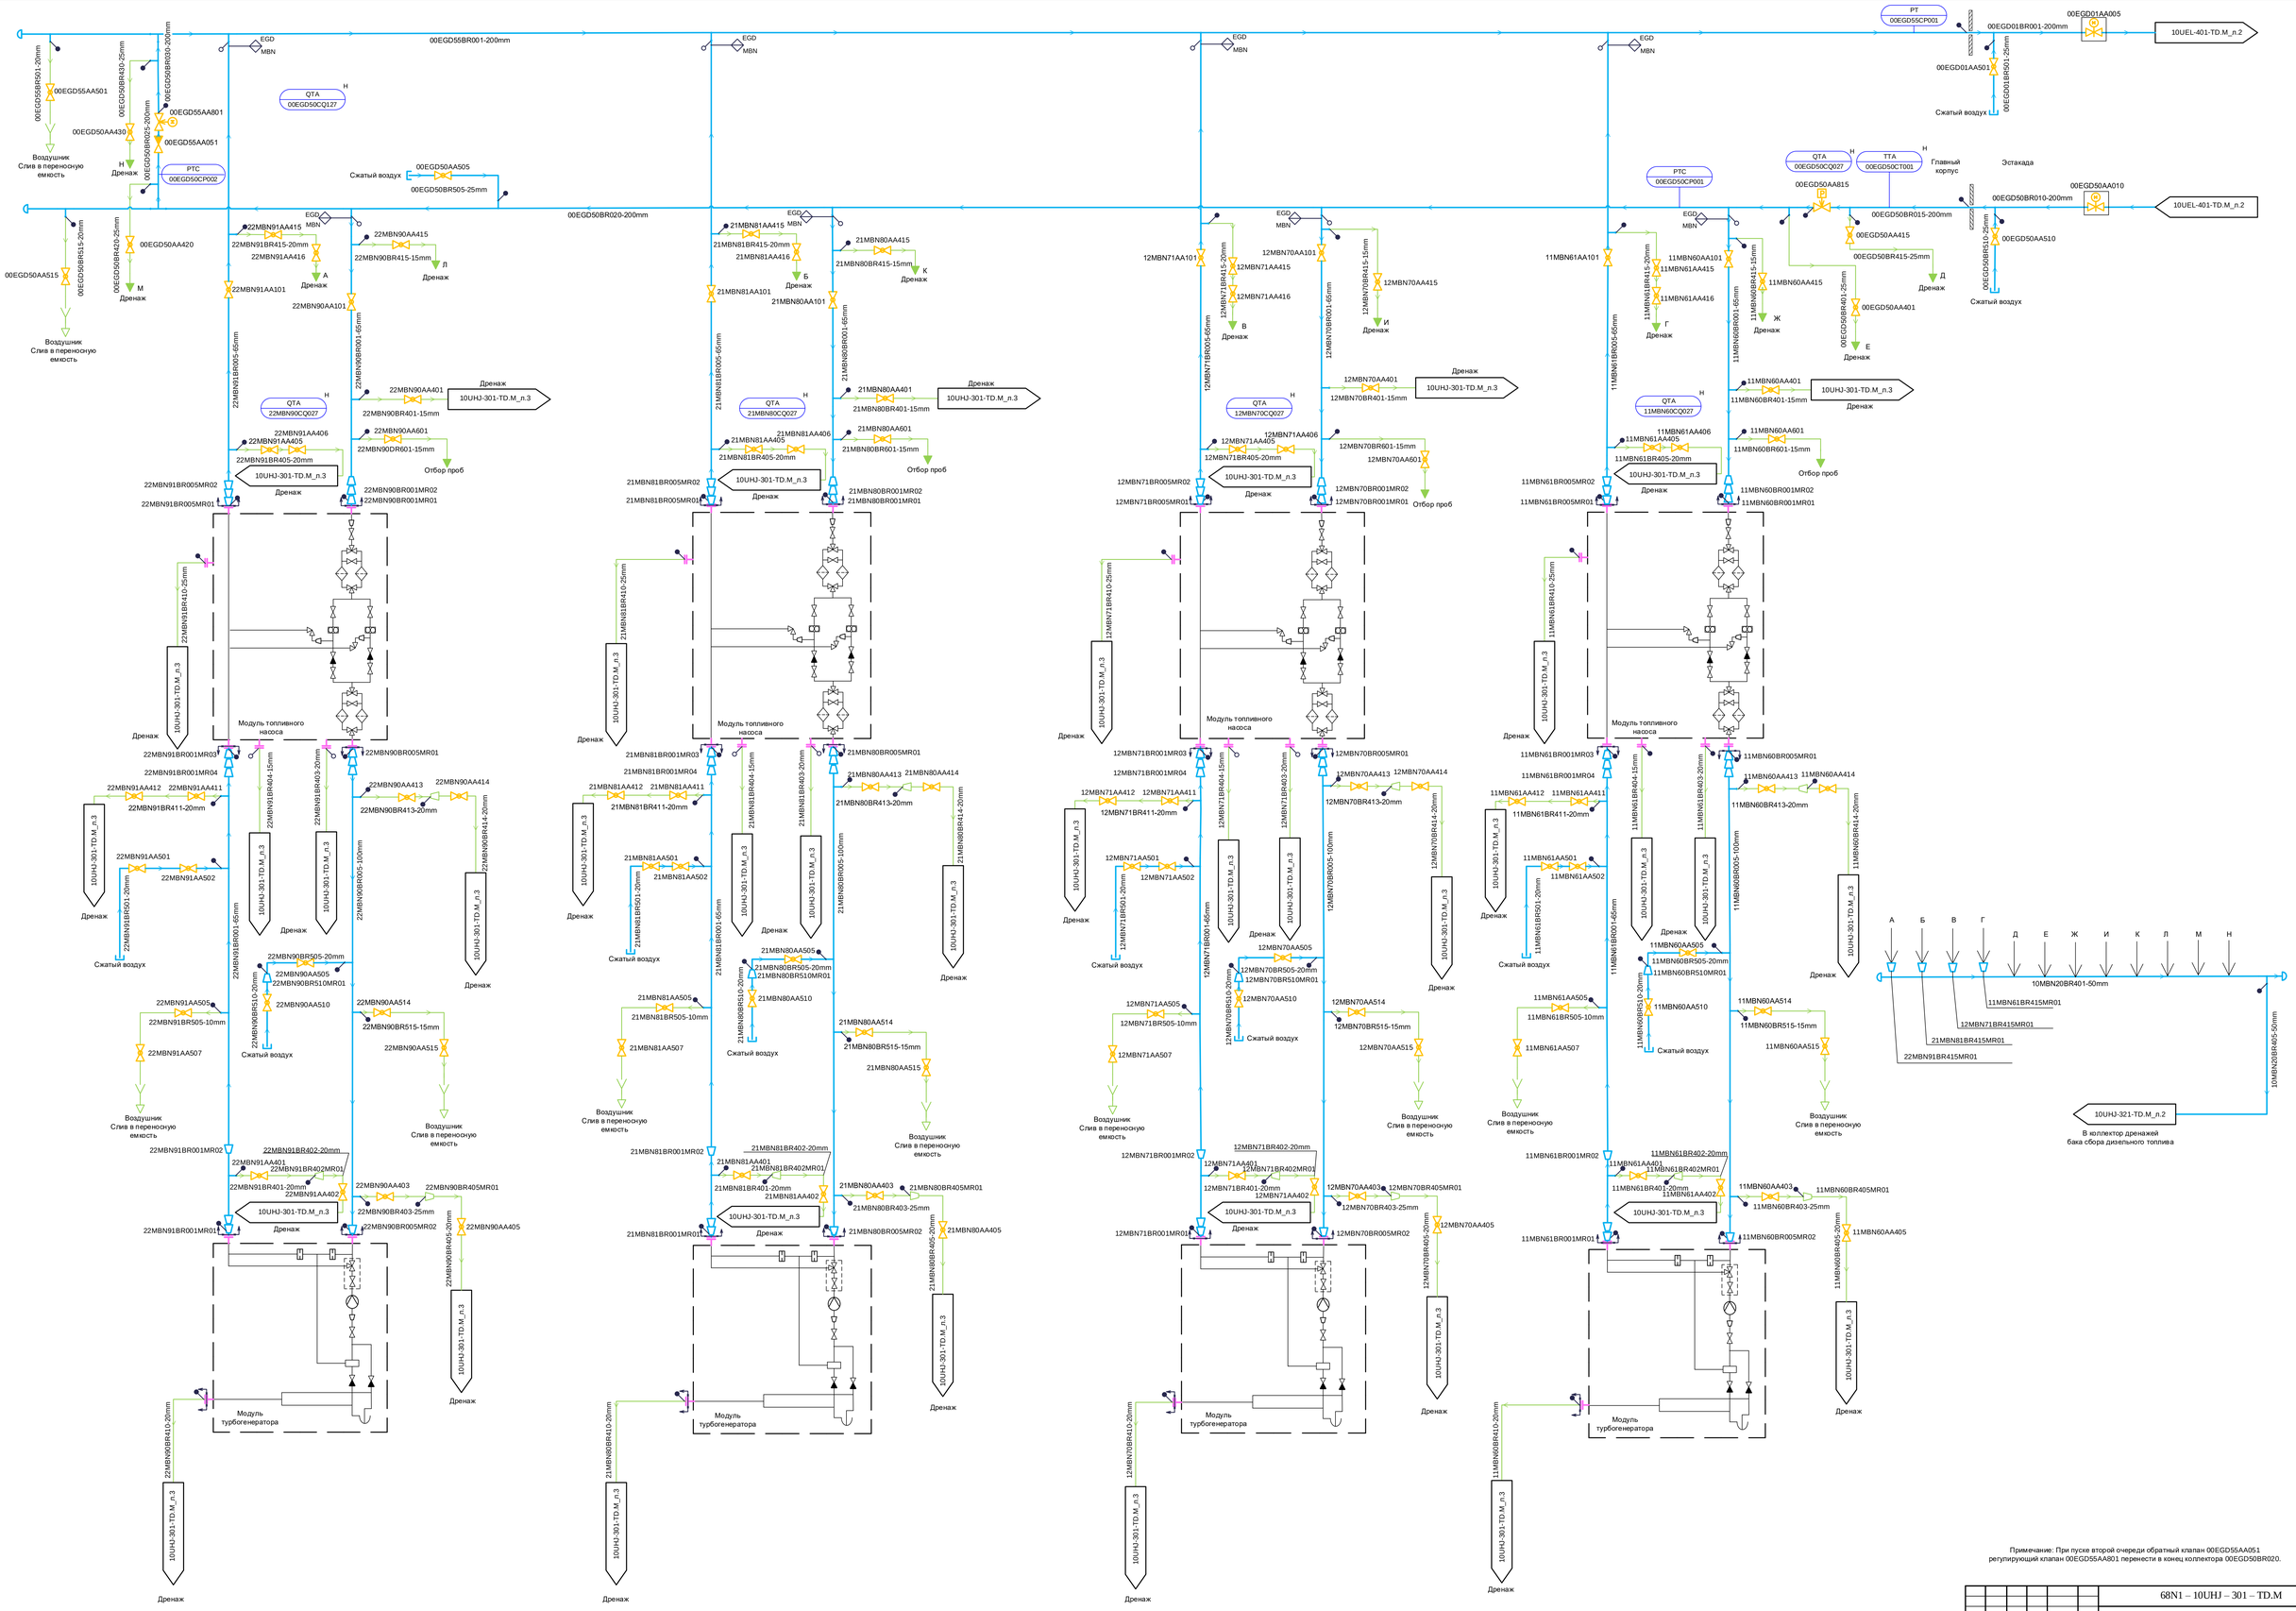

						68N1 – 10UHJ – 301 – TD.M	
1	- -	Зам	69-13			Строительство Якутской ГРЭС-2	
Изм.	Кол.уч	Лист	№ док.	Подп.	Дата		
Разработал	Полевская					Главный корпус. PI-диаграмма трубопроводов дизельного топлива к ГТУ	Стадия: Р; Лист: 2; Листов:
Проверил	Бобров						
Гл.спец.	Стацура						
Н. контр.	Астразанцев					PI-диаграмма трубопроводов дизельного топлива к ГТУ. Система MBN,EGD.	Российский газовый концерн ТРАНСГАЗГРУППА

Согласовано

Взам. инв. №

Подпись и дата

Инв. № подл.

Формат А0