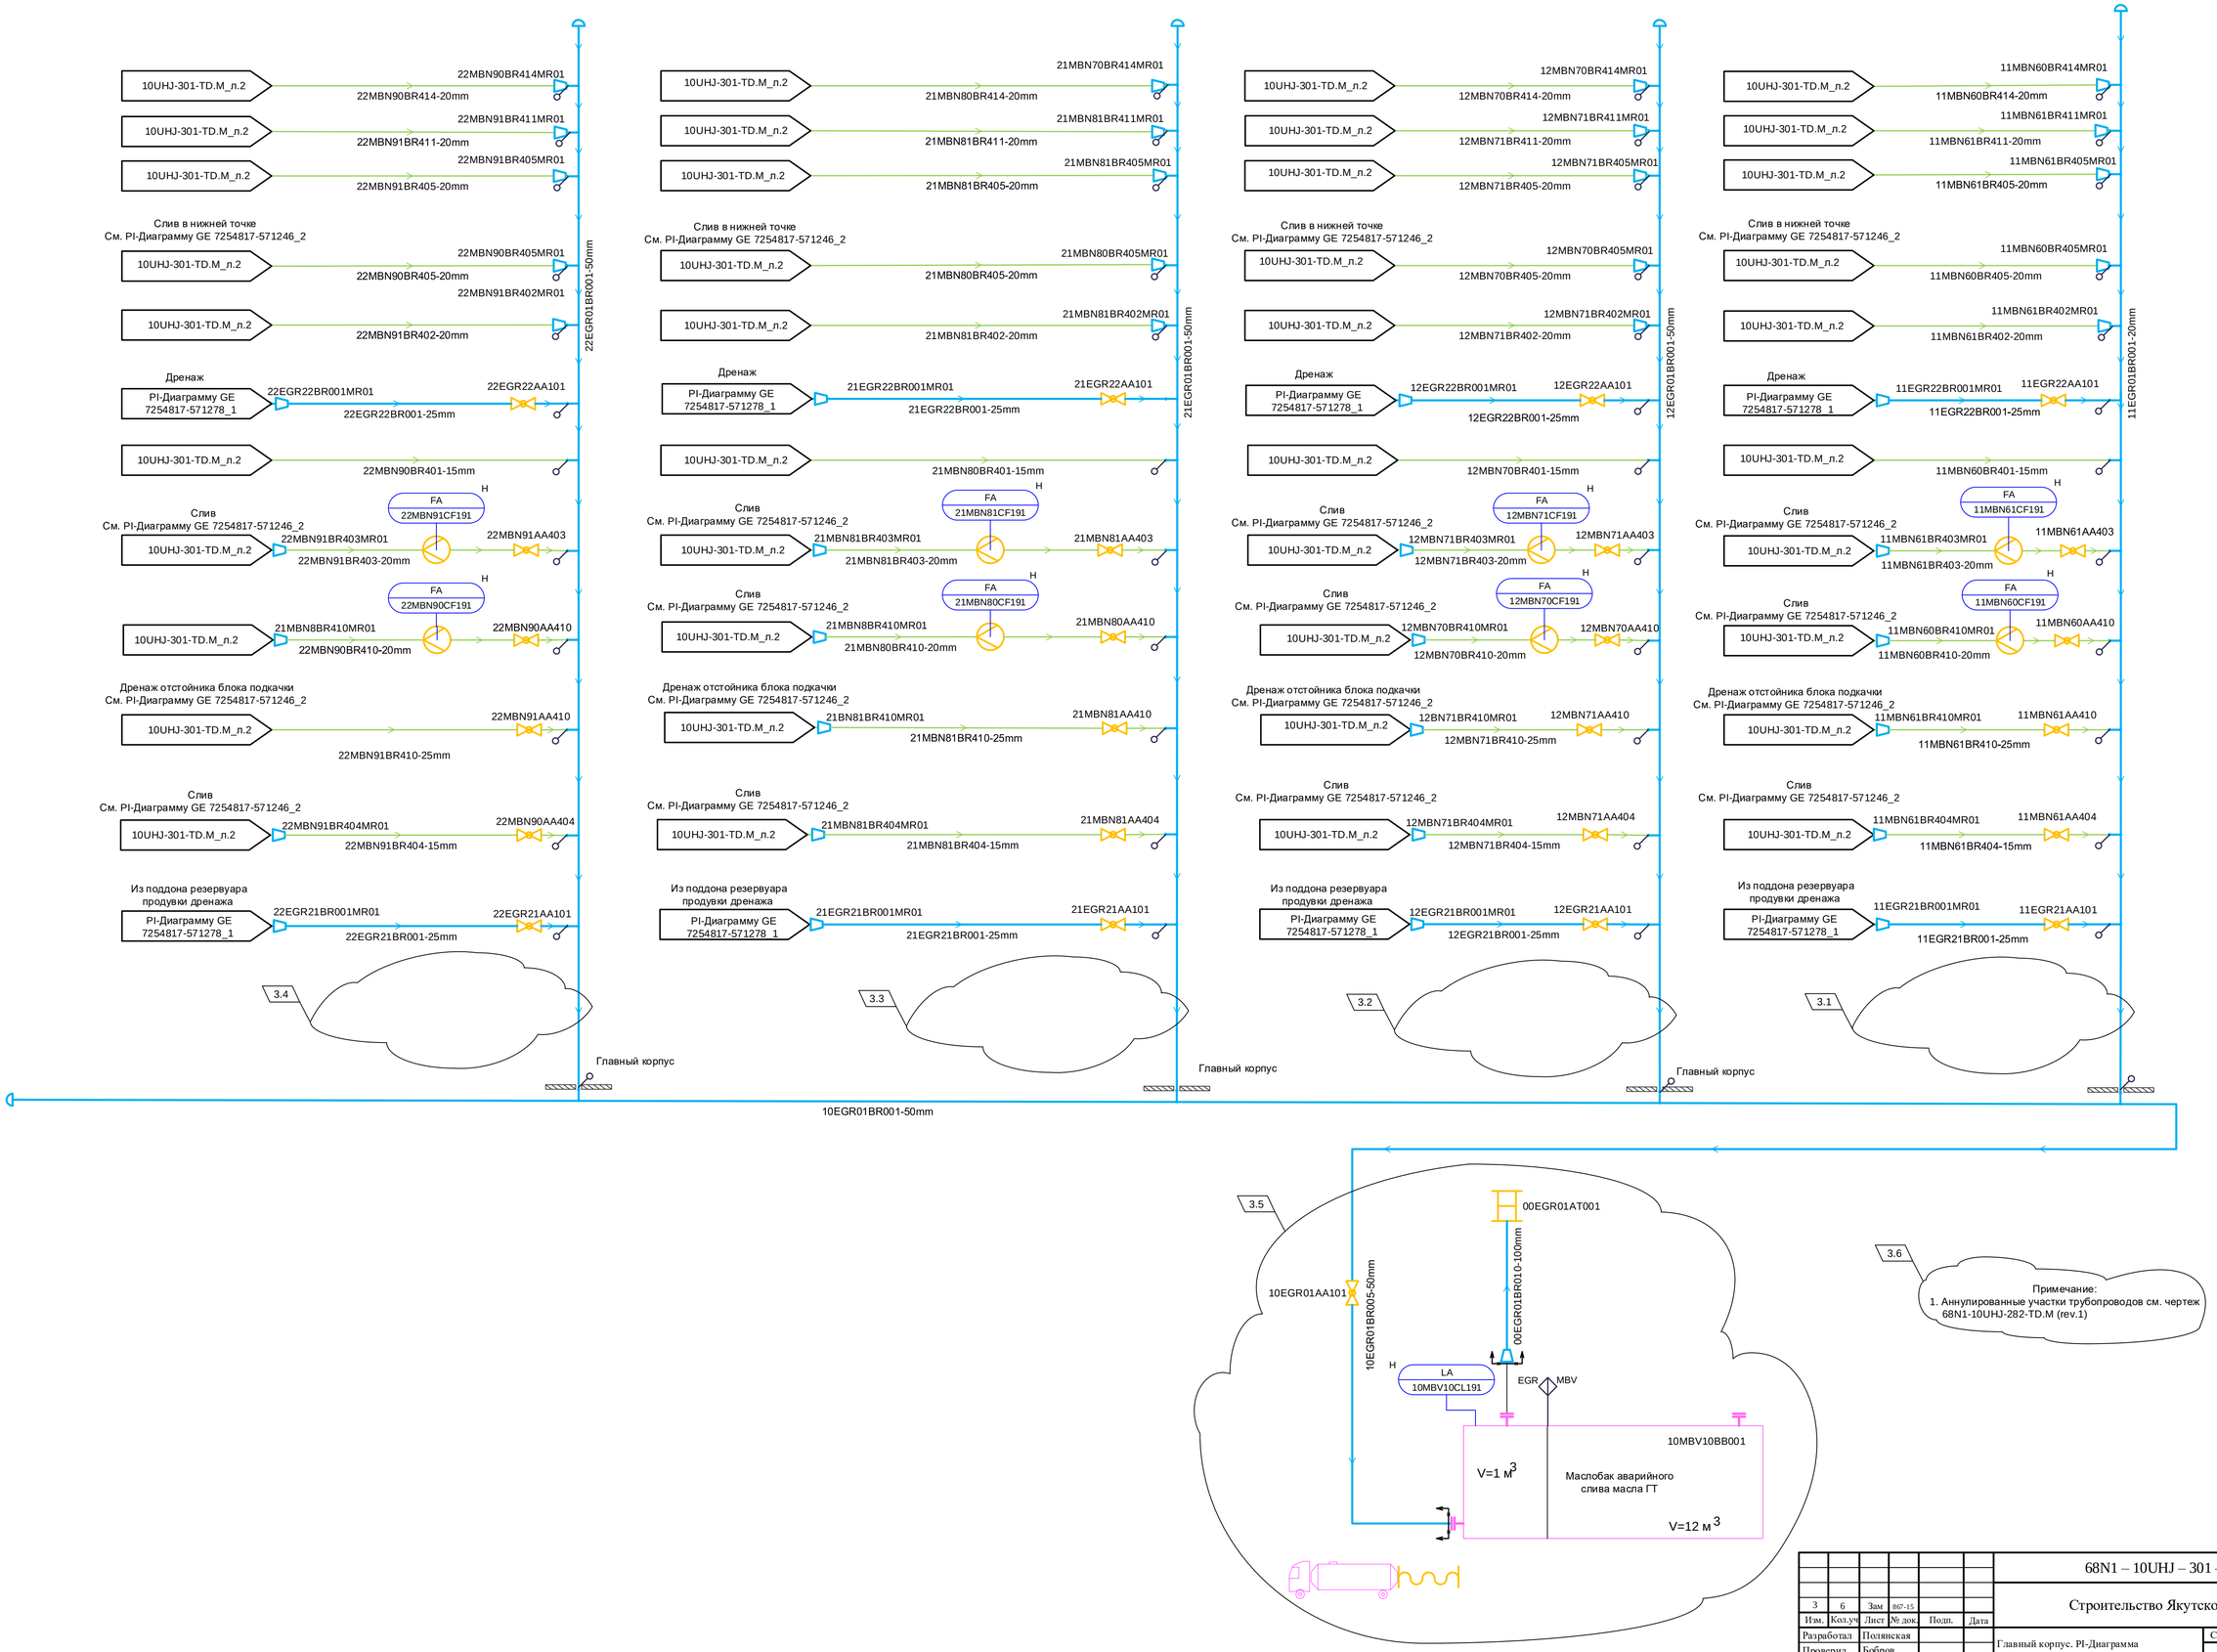

3	6	Зам	867-15			
Изм.	Кол.уч	Лист	№ док.	Подп.	Дата	
Разработал		Полянская				
Проверил		Бобров				
Гл.спец.		Стацура				
Н. контр.		Астраханцев				

68N1 – 10UHJ – 301 – TD.M

Строительство Якутской ГРЭС-2

Главный корпус. PI-Диаграмма трубопроводов дизельного топлива к ГТУ

Стадия	Лист	Листов
Р	3	

PI-Диаграмма трубопроводов дренажей дизельного топлива ГТУ. Системы EKR, MBN

АКЦИОНЕРНОЕ ОБЩЕСТВО ИНСТИТУТ ТЕПЛОЭЛЕКТРОПРОЕКТ г. МОСКВА

Согласовано

Взам. инв. №

Подпись и дата

Инв. № подл.

Формат А1