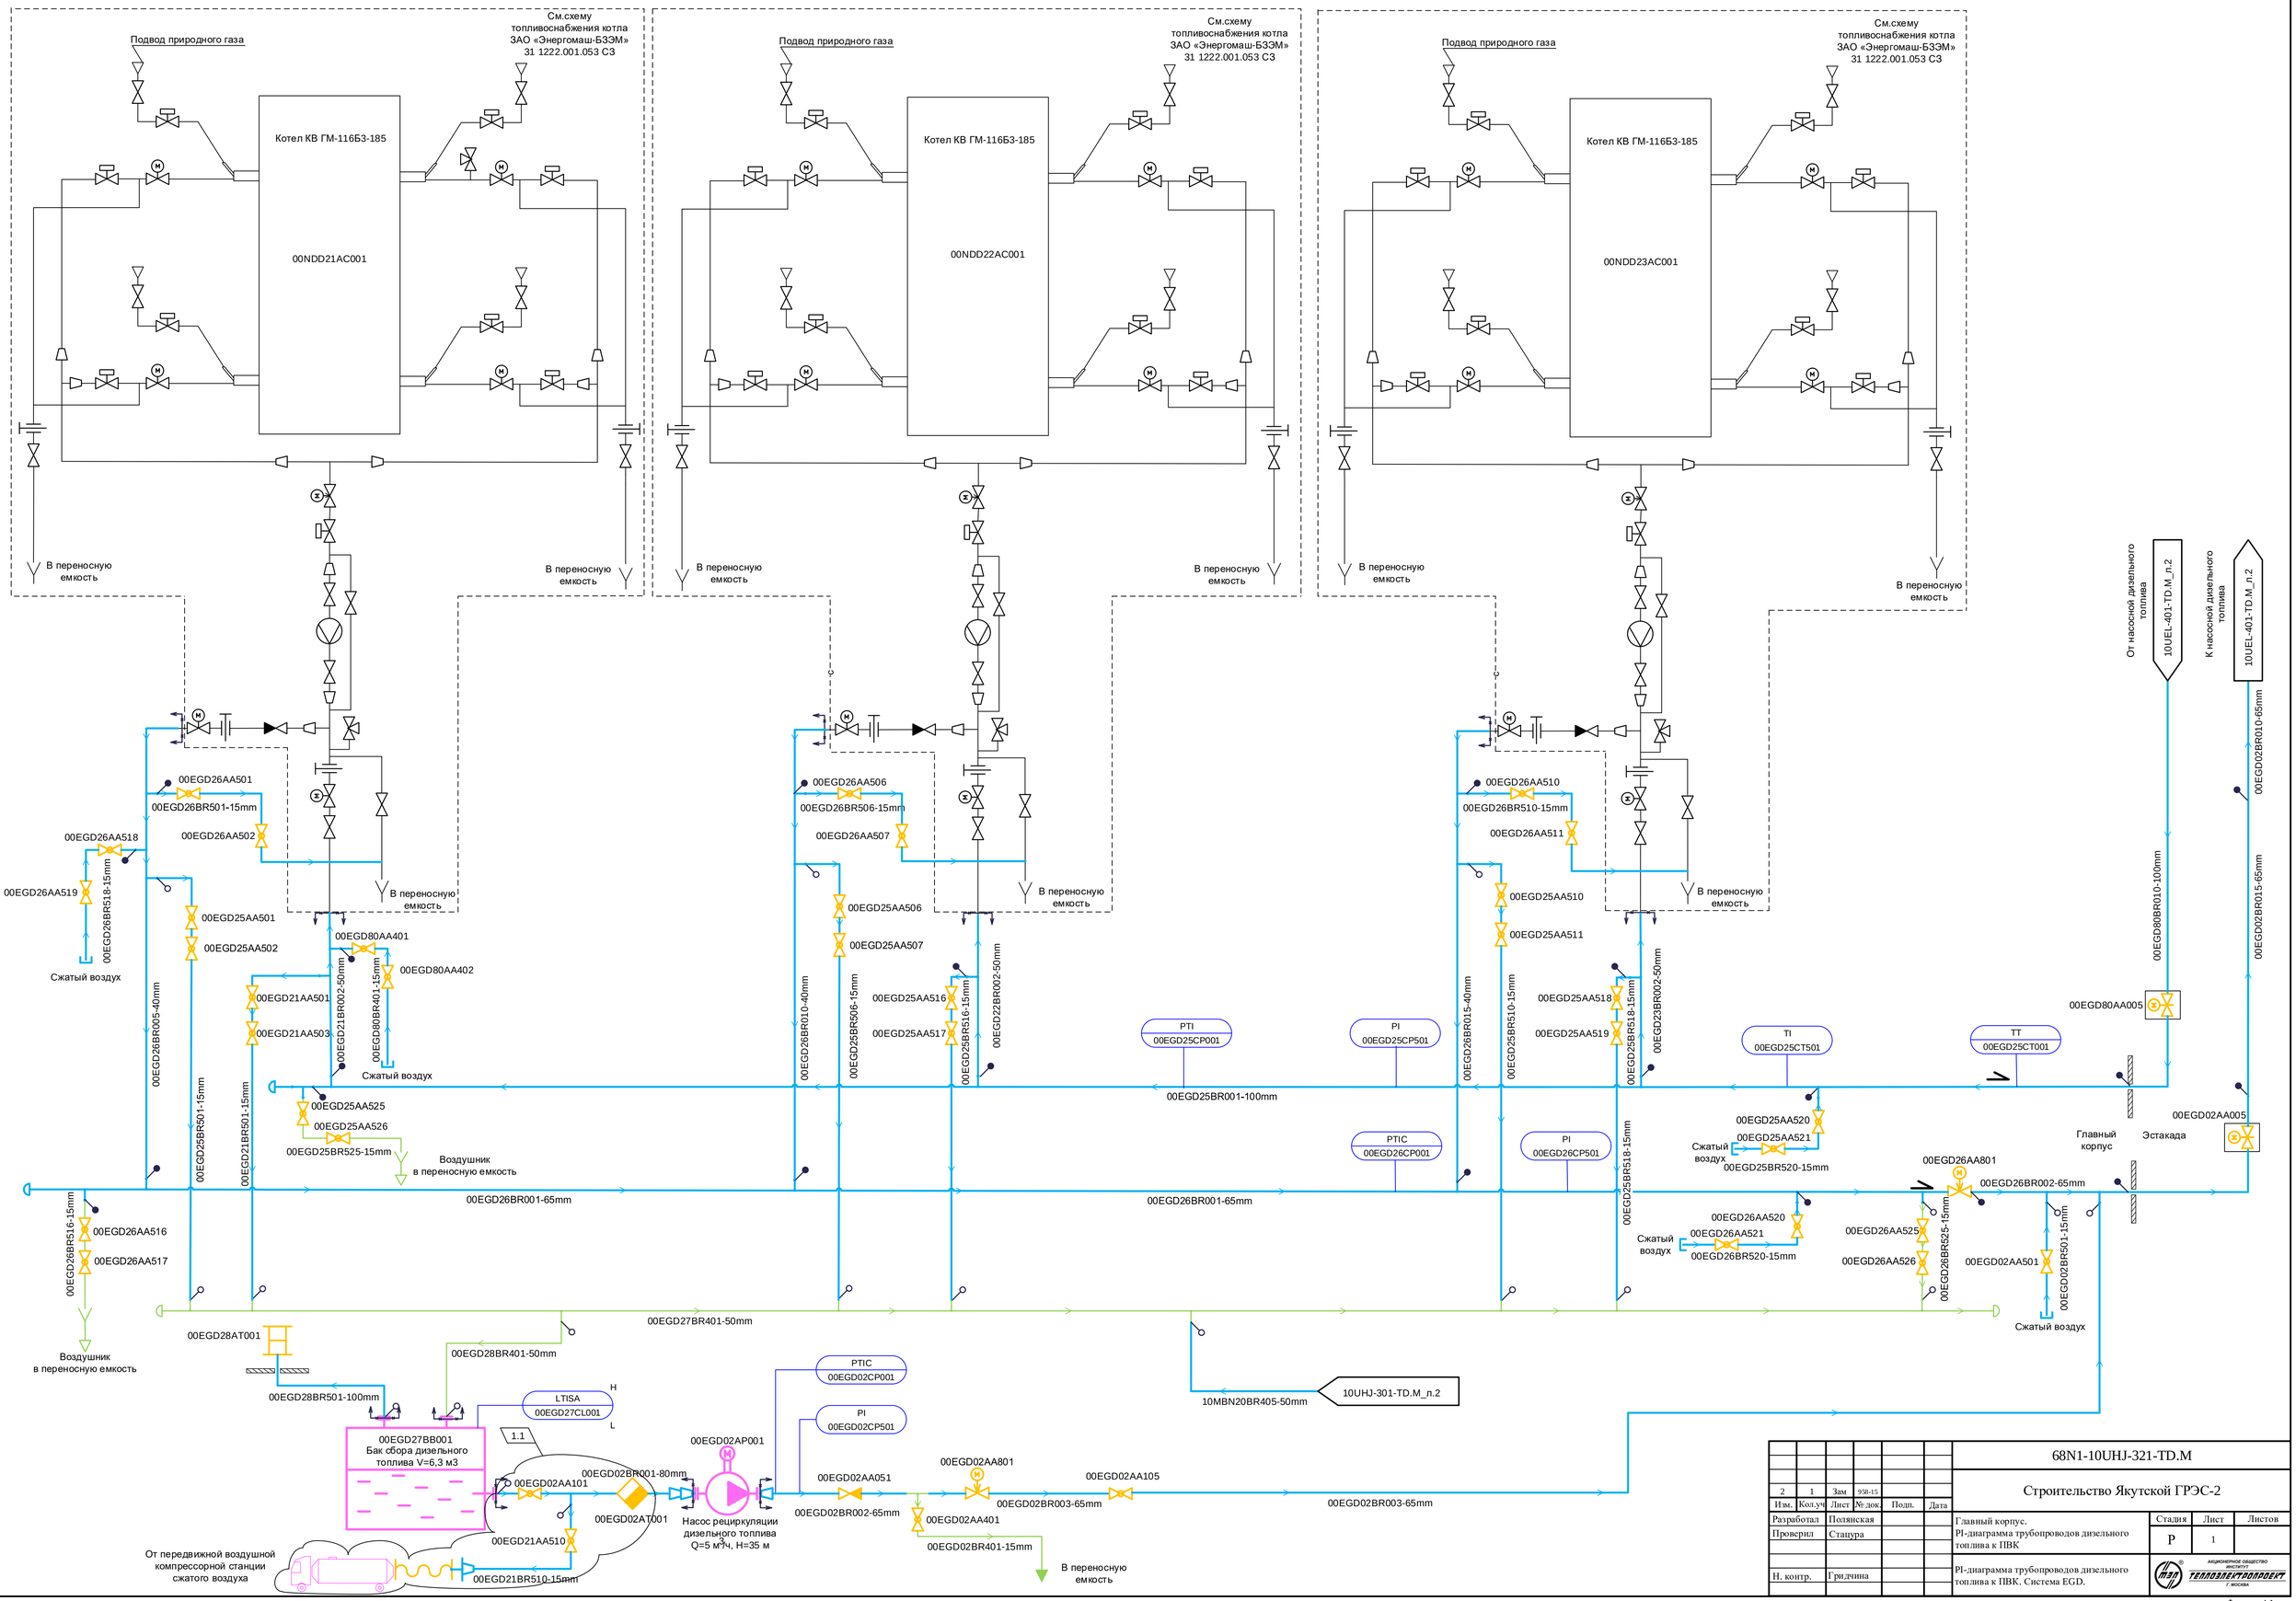

2	1	Зам	958-15			
Изм.	Кол.уч	Лист	№ док.	Подп.	Дата	
Разработал		Полянская				
Проверил		Стацура				
Н. контр.		Грядчина				

68N1-10UHJ-321-TD.M

Строительство Якутской ГРЭС-2

Главный корпус.
PI-диаграмма трубопроводов дизельного топлива к ПВК

Стадия	Лист	Листов
Р	1	

PI-диаграмма трубопроводов дизельного топлива к ПВК. Система EGD.

АКЦИОНЕРНОЕ ОБЩЕСТВО ИНЖИНИРИНГОВАЯ КОМПАНИЯ ТЕПЛОЭЛЕКТРОПРОЕКТ г. МОСКВА

Согласовано

Взам. инв. №

Подпись и дата

Инв. № подл.

Формат А1