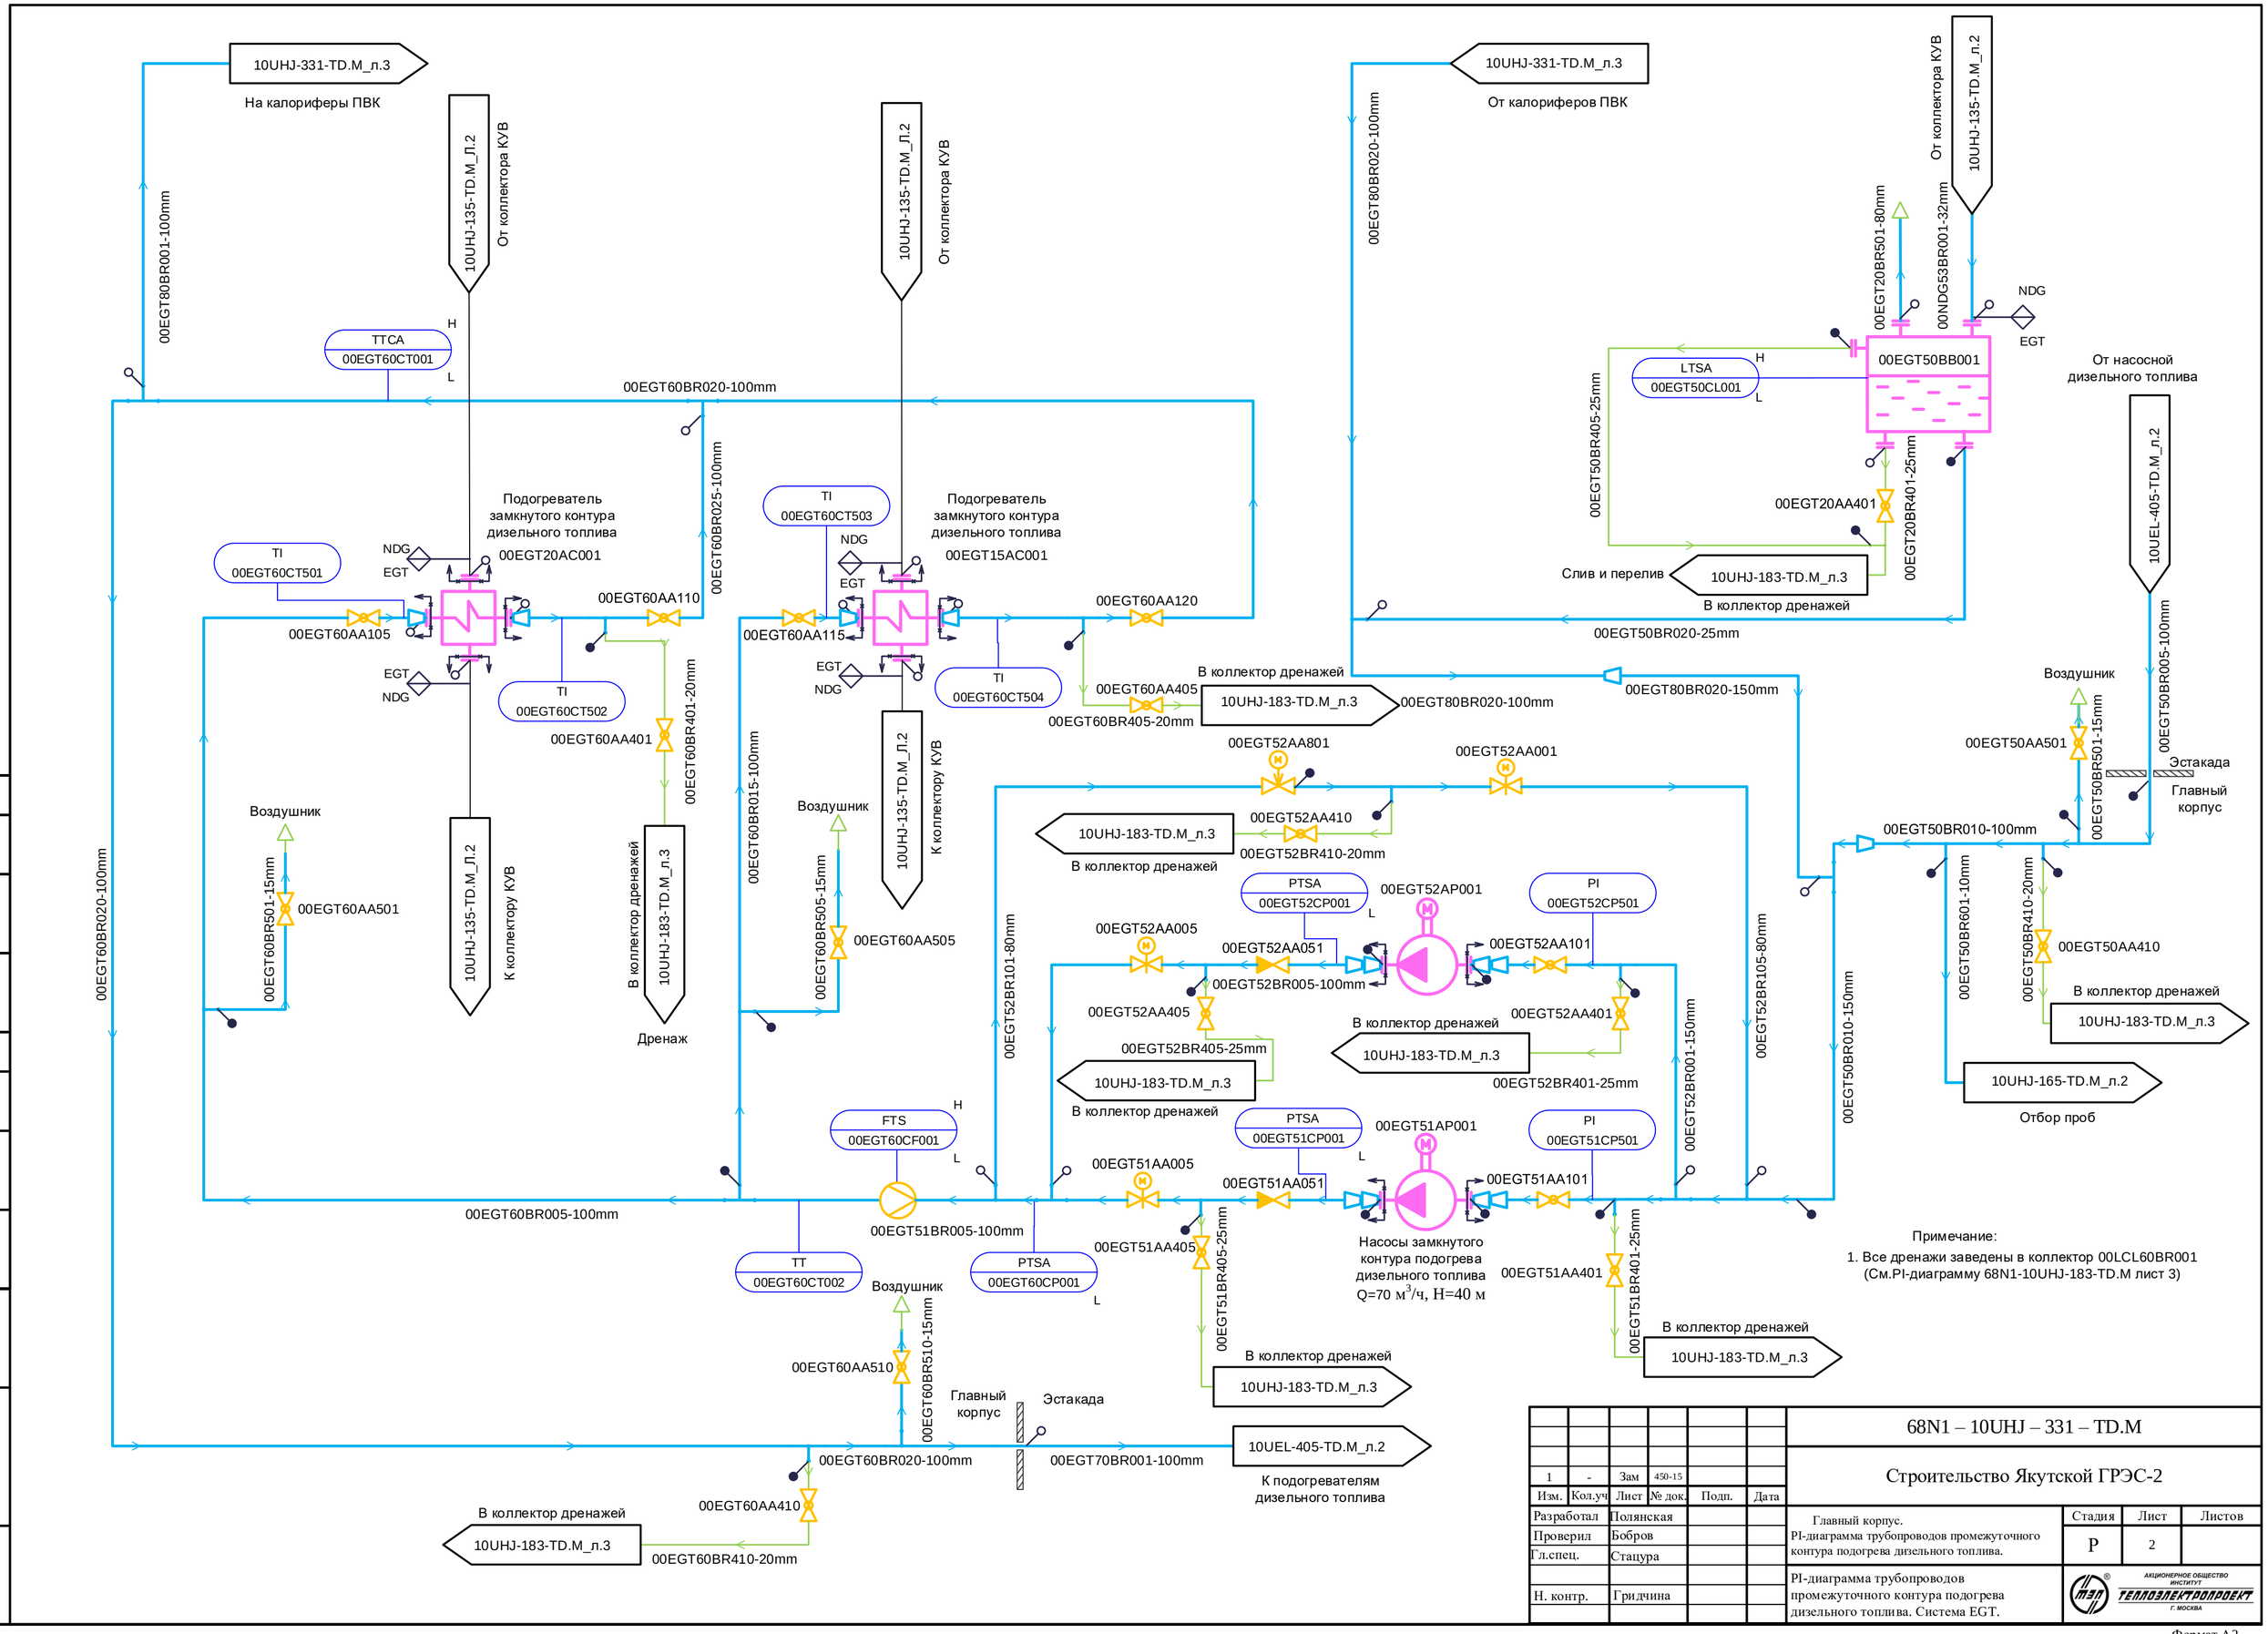

Примечание:

1. Все дренажи заведены в коллектор 00LCL60BR001 (См.PI-диаграмму 68N1-10UHJ-183-TD.M лист 3)

Изм.	Кол.уч	Лист	№ док.	Подп.	Дата
1	-	Зам	450-15		

Разработал	Полянская	
Проверил	Бобров	
Гл.спец.	Стацура	
Н. контр.	Гридчина	

68N1 – 10UHJ – 331 – TD.M

Строительство Якутской ГРЭС-2

Главный корпус.
PI-диаграмма трубопроводов промежуточного контура подогрева дизельного топлива.

PI-диаграмма трубопроводов промежуточного контура подогрева дизельного топлива. Система EGT.

Стадия	Лист	Листов
Р	2	

АКЦИОНЕРНОЕ ОБЩЕСТВО ИНСТИТУТ ТЕПЛОЭЛЕКТРОПРОЕКТ Г. МОСКВА

Согласовано

Взам. инв. №

Подпись и дата

Инв. № подл.

Формат А2