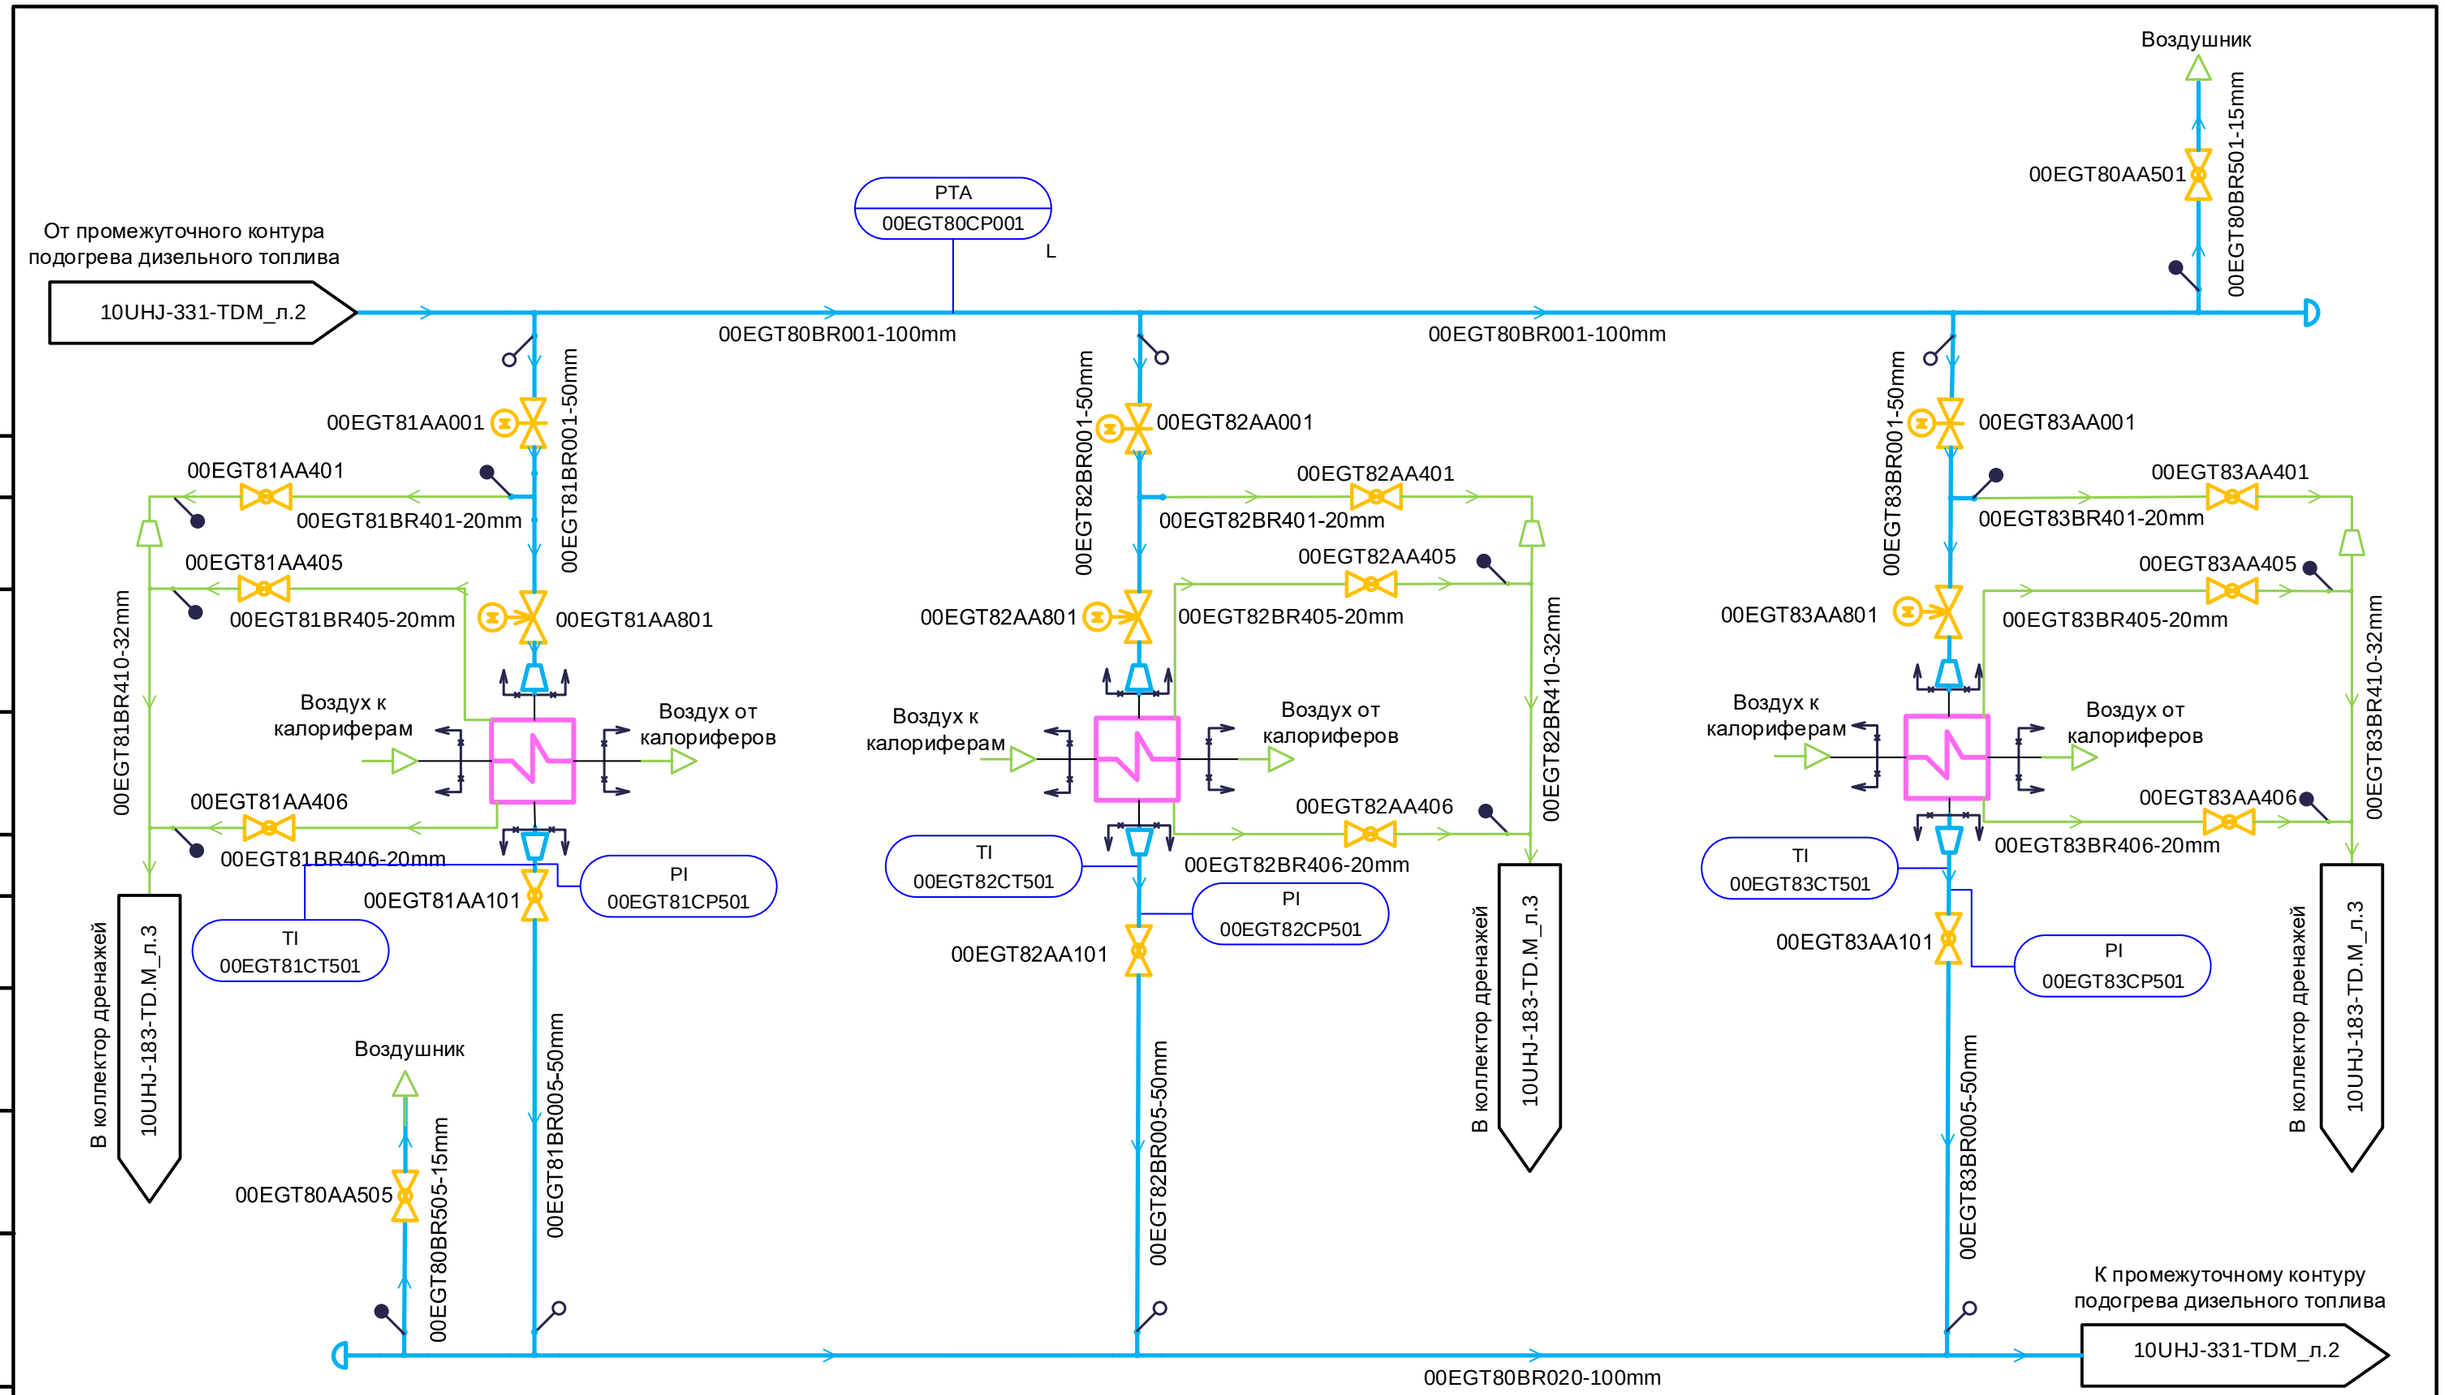

1	-	Зам	450-15			
Изм.	Кол.уч	Лист	№ док.	Подп.	Дата	
Разработал		Полянская				
Проверил		Бобров				
Гл.спец.		Стацура				
Н. контр.		Гридчина				

68N1-10UHJ-331-TD.M

Строительство Якутской ГРЭС-2

Главный корпус.
PI-Диаграмма трубопроводов промежуточного контура подогрева дизельного топлива

Стадия	Лист	Листов
Р	3	

PI-диаграмма трубопроводов подогрева воздуха на калориферы. Система EGT.

АКЦИОНЕРНОЕ ОБЩЕСТВО ИНСТИТУТ ТЕПЛОЭЛЕКТРОПРОЕКТ Г. МОСКВА

Согласовано
ОАСУ
Взам. инв. №
Подпись и дата
Инв. № подл.

Формат А3