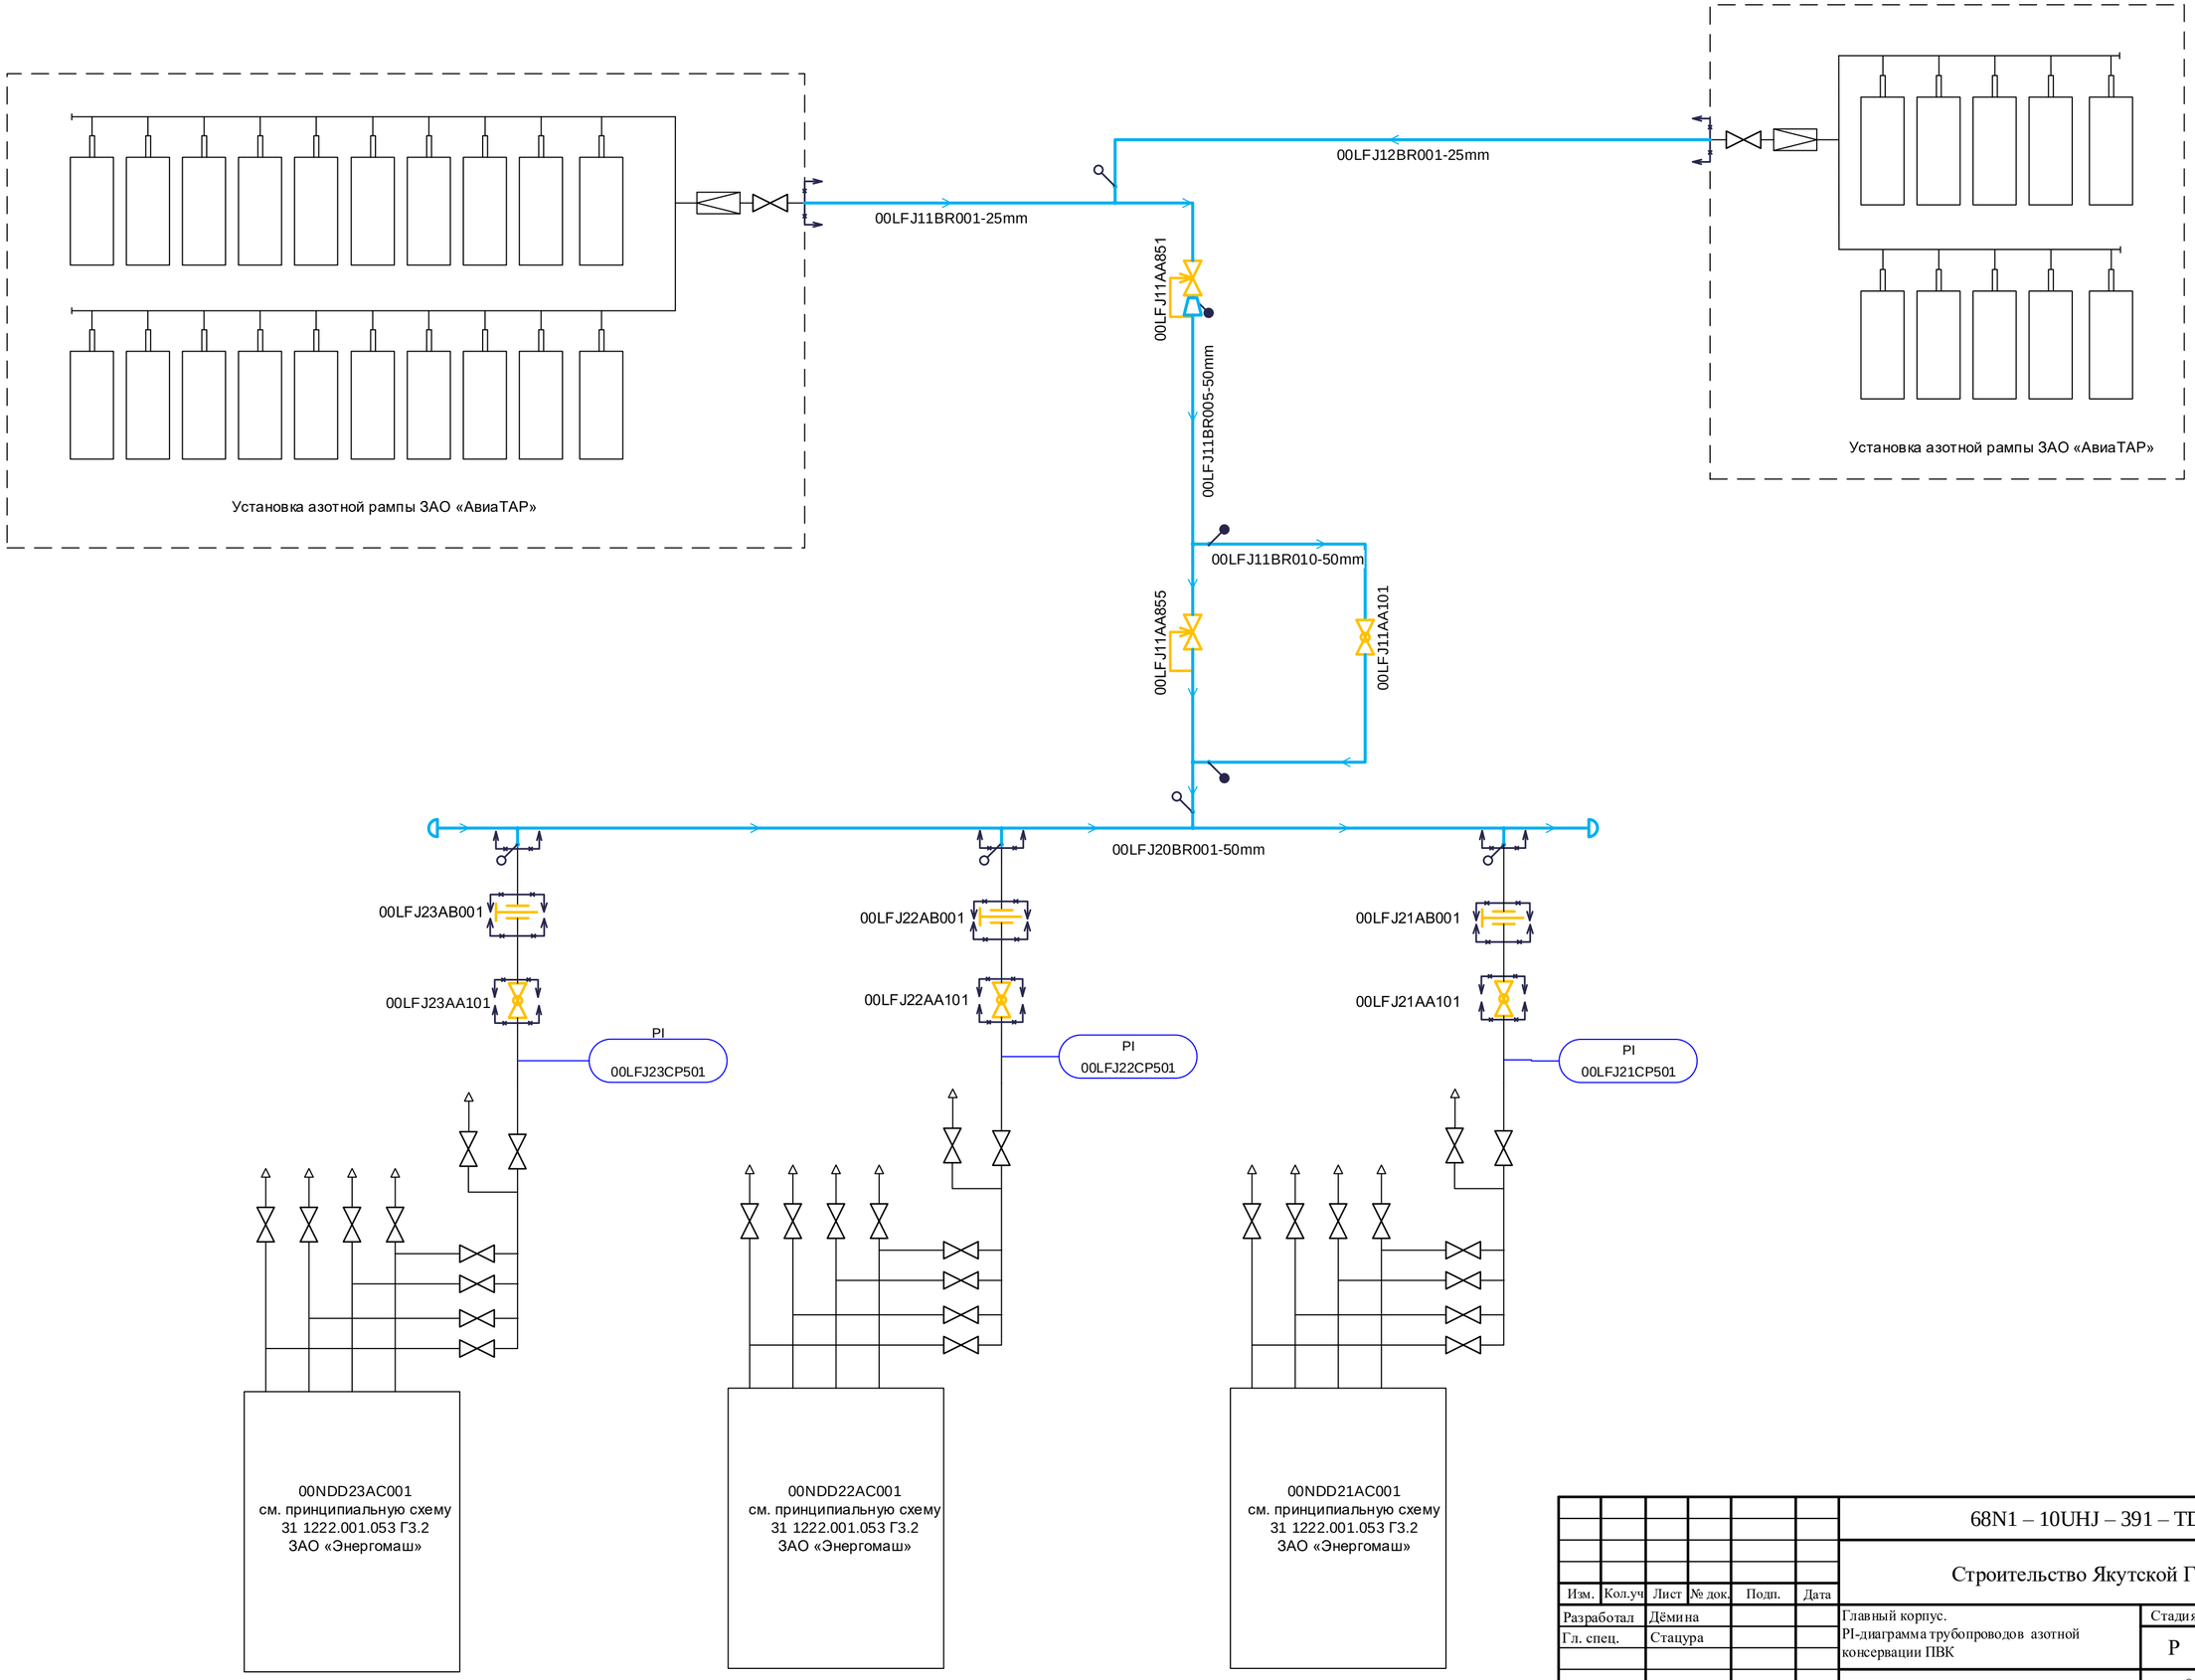

Изм.	Кол.уч	Лист	№ док.	Подп.	Дата
Разработал		Дёмина			
Гл. спец.		Стацура			
Н. контр.		Астраханцев			

68N1 – 10UHJ – 391 – TD.M

Строительство Якутской ГРЭС-2

Главный корпус.
PI-диаграмма трубопроводов азотной консервации ПВК

Стадия	Лист	Листов
Р	2	

PI-диаграмма трубопроводов азотной консервации ПВК. Система LFJ

АКЦИОНЕРНОЕ ОБЩЕСТВО ИНСТИТУТ ТЕПЛОЭЛЕКТРОПРОЕКТ Г. МОСКВА

Согласовано

ОАСУ

Взам. инв. №

Подпись и дата

Инв. № подл.

Формат А2