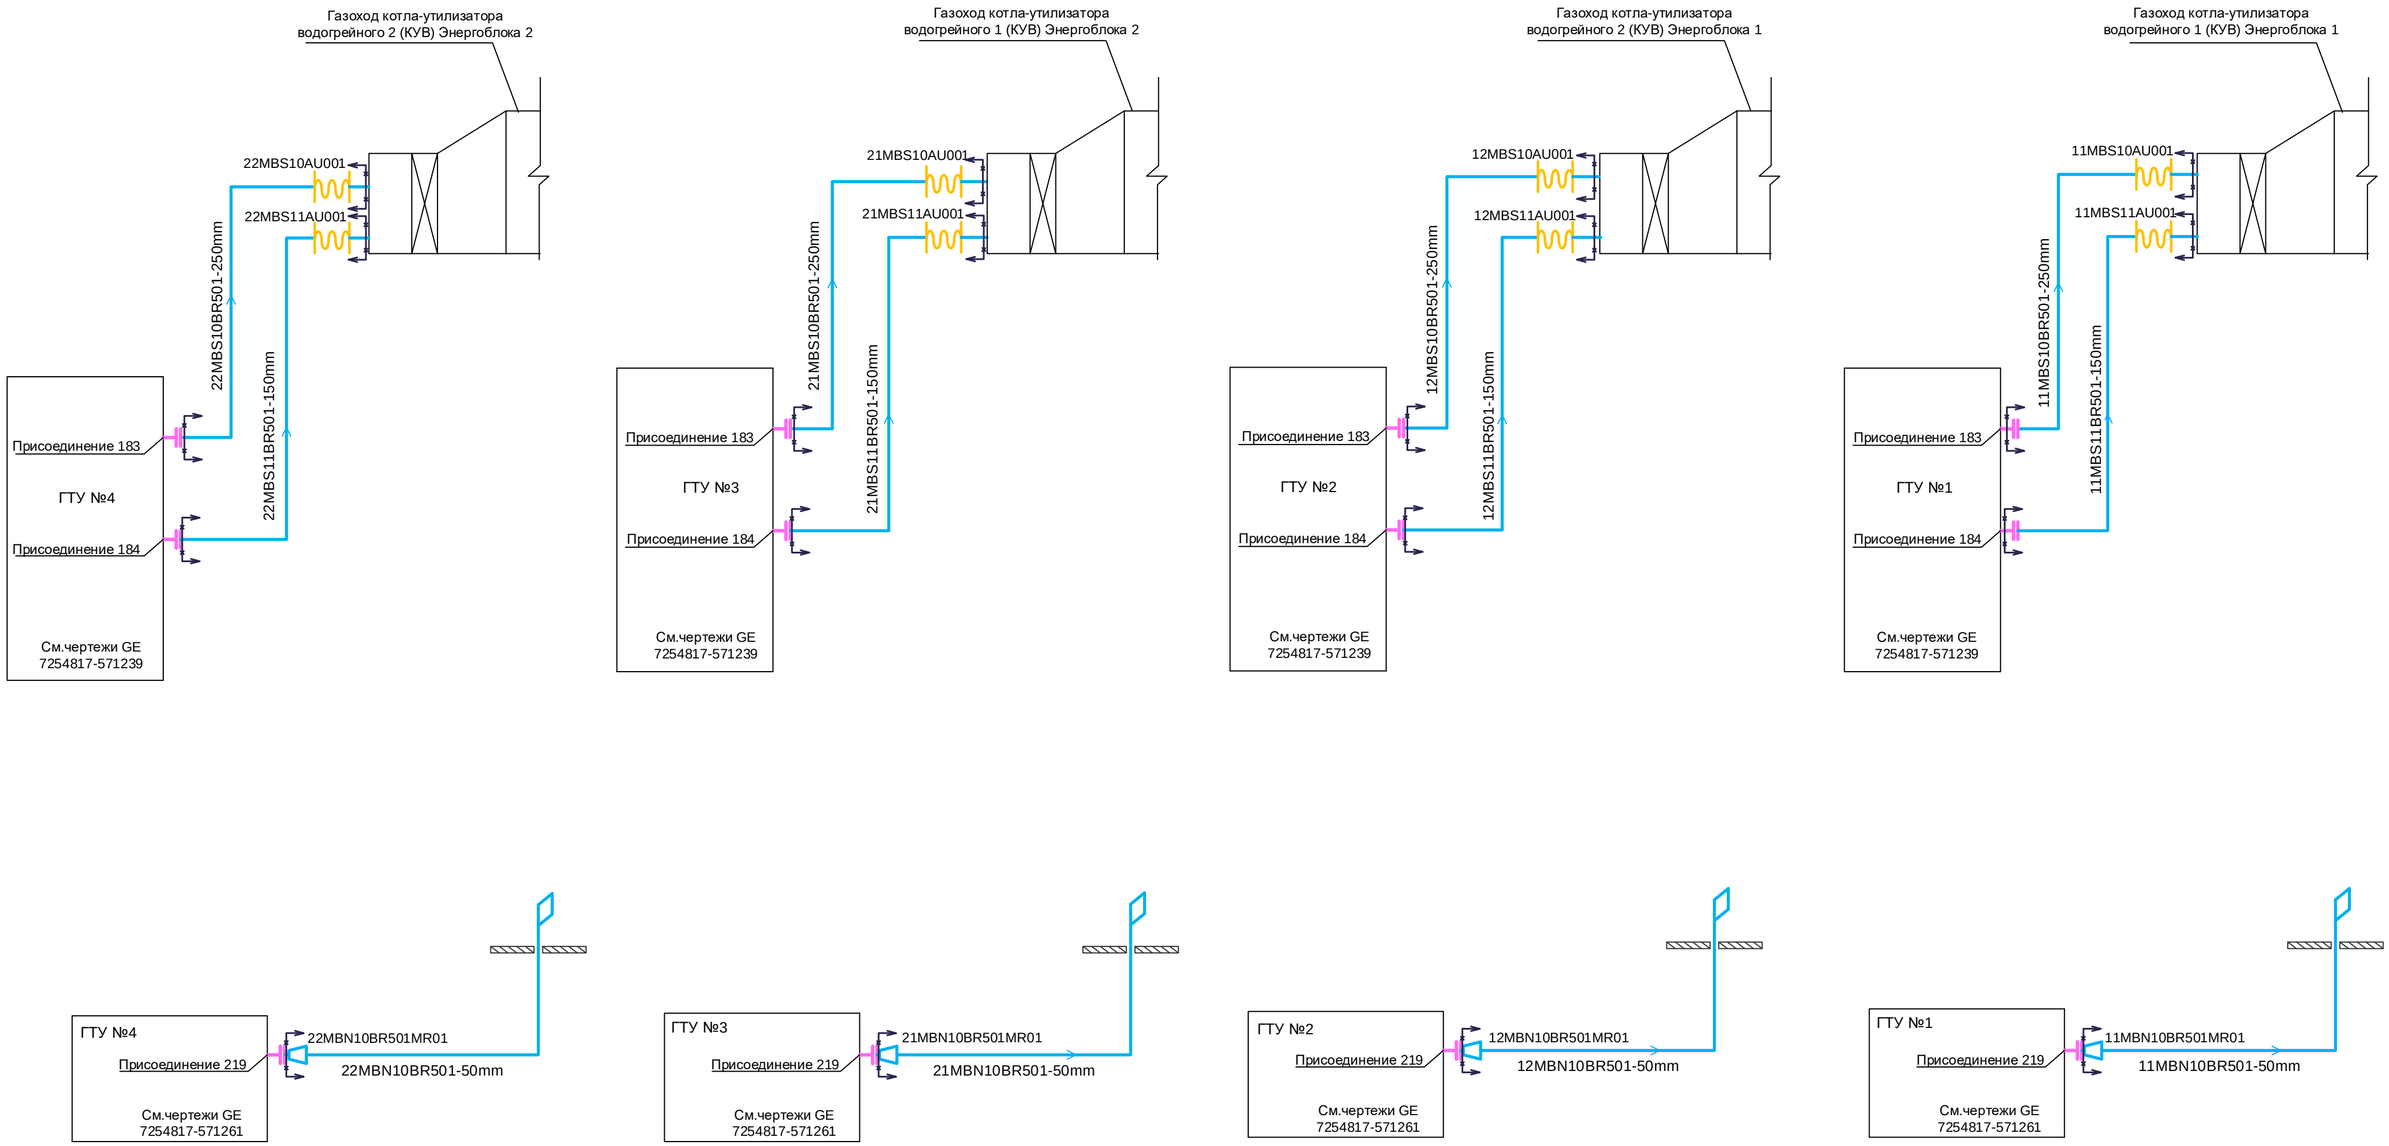

Согласовано

Взам. инв. №

Подпись и дата

Инв. № подл.

1	-	Зам	769-15			
Изм.	Кол.уч	Лист	№ док.	Подп.	Дата	
Разработал		Полянская				
Проверил		Стацура				
Н. контр.		Гридчина				

68N1 – 10UHJ – 397 – TD.M

Строительство Якутской ГРЭС-2

Главный корпус. PI-диаграмма вспомогательных трубопроводов ГТУ.

Стадия	Лист	Листов
Р	2	

PI-диаграмма вспомогательных трубопроводов ГТУ. Система MBS, MBN

АКЦИОНЕРНОЕ ОБЩЕСТВО ИНСТИТУТ ТЕПЛОЭЛЕКТРОПРОЕКТ Г. МОСКВА

Формат А2