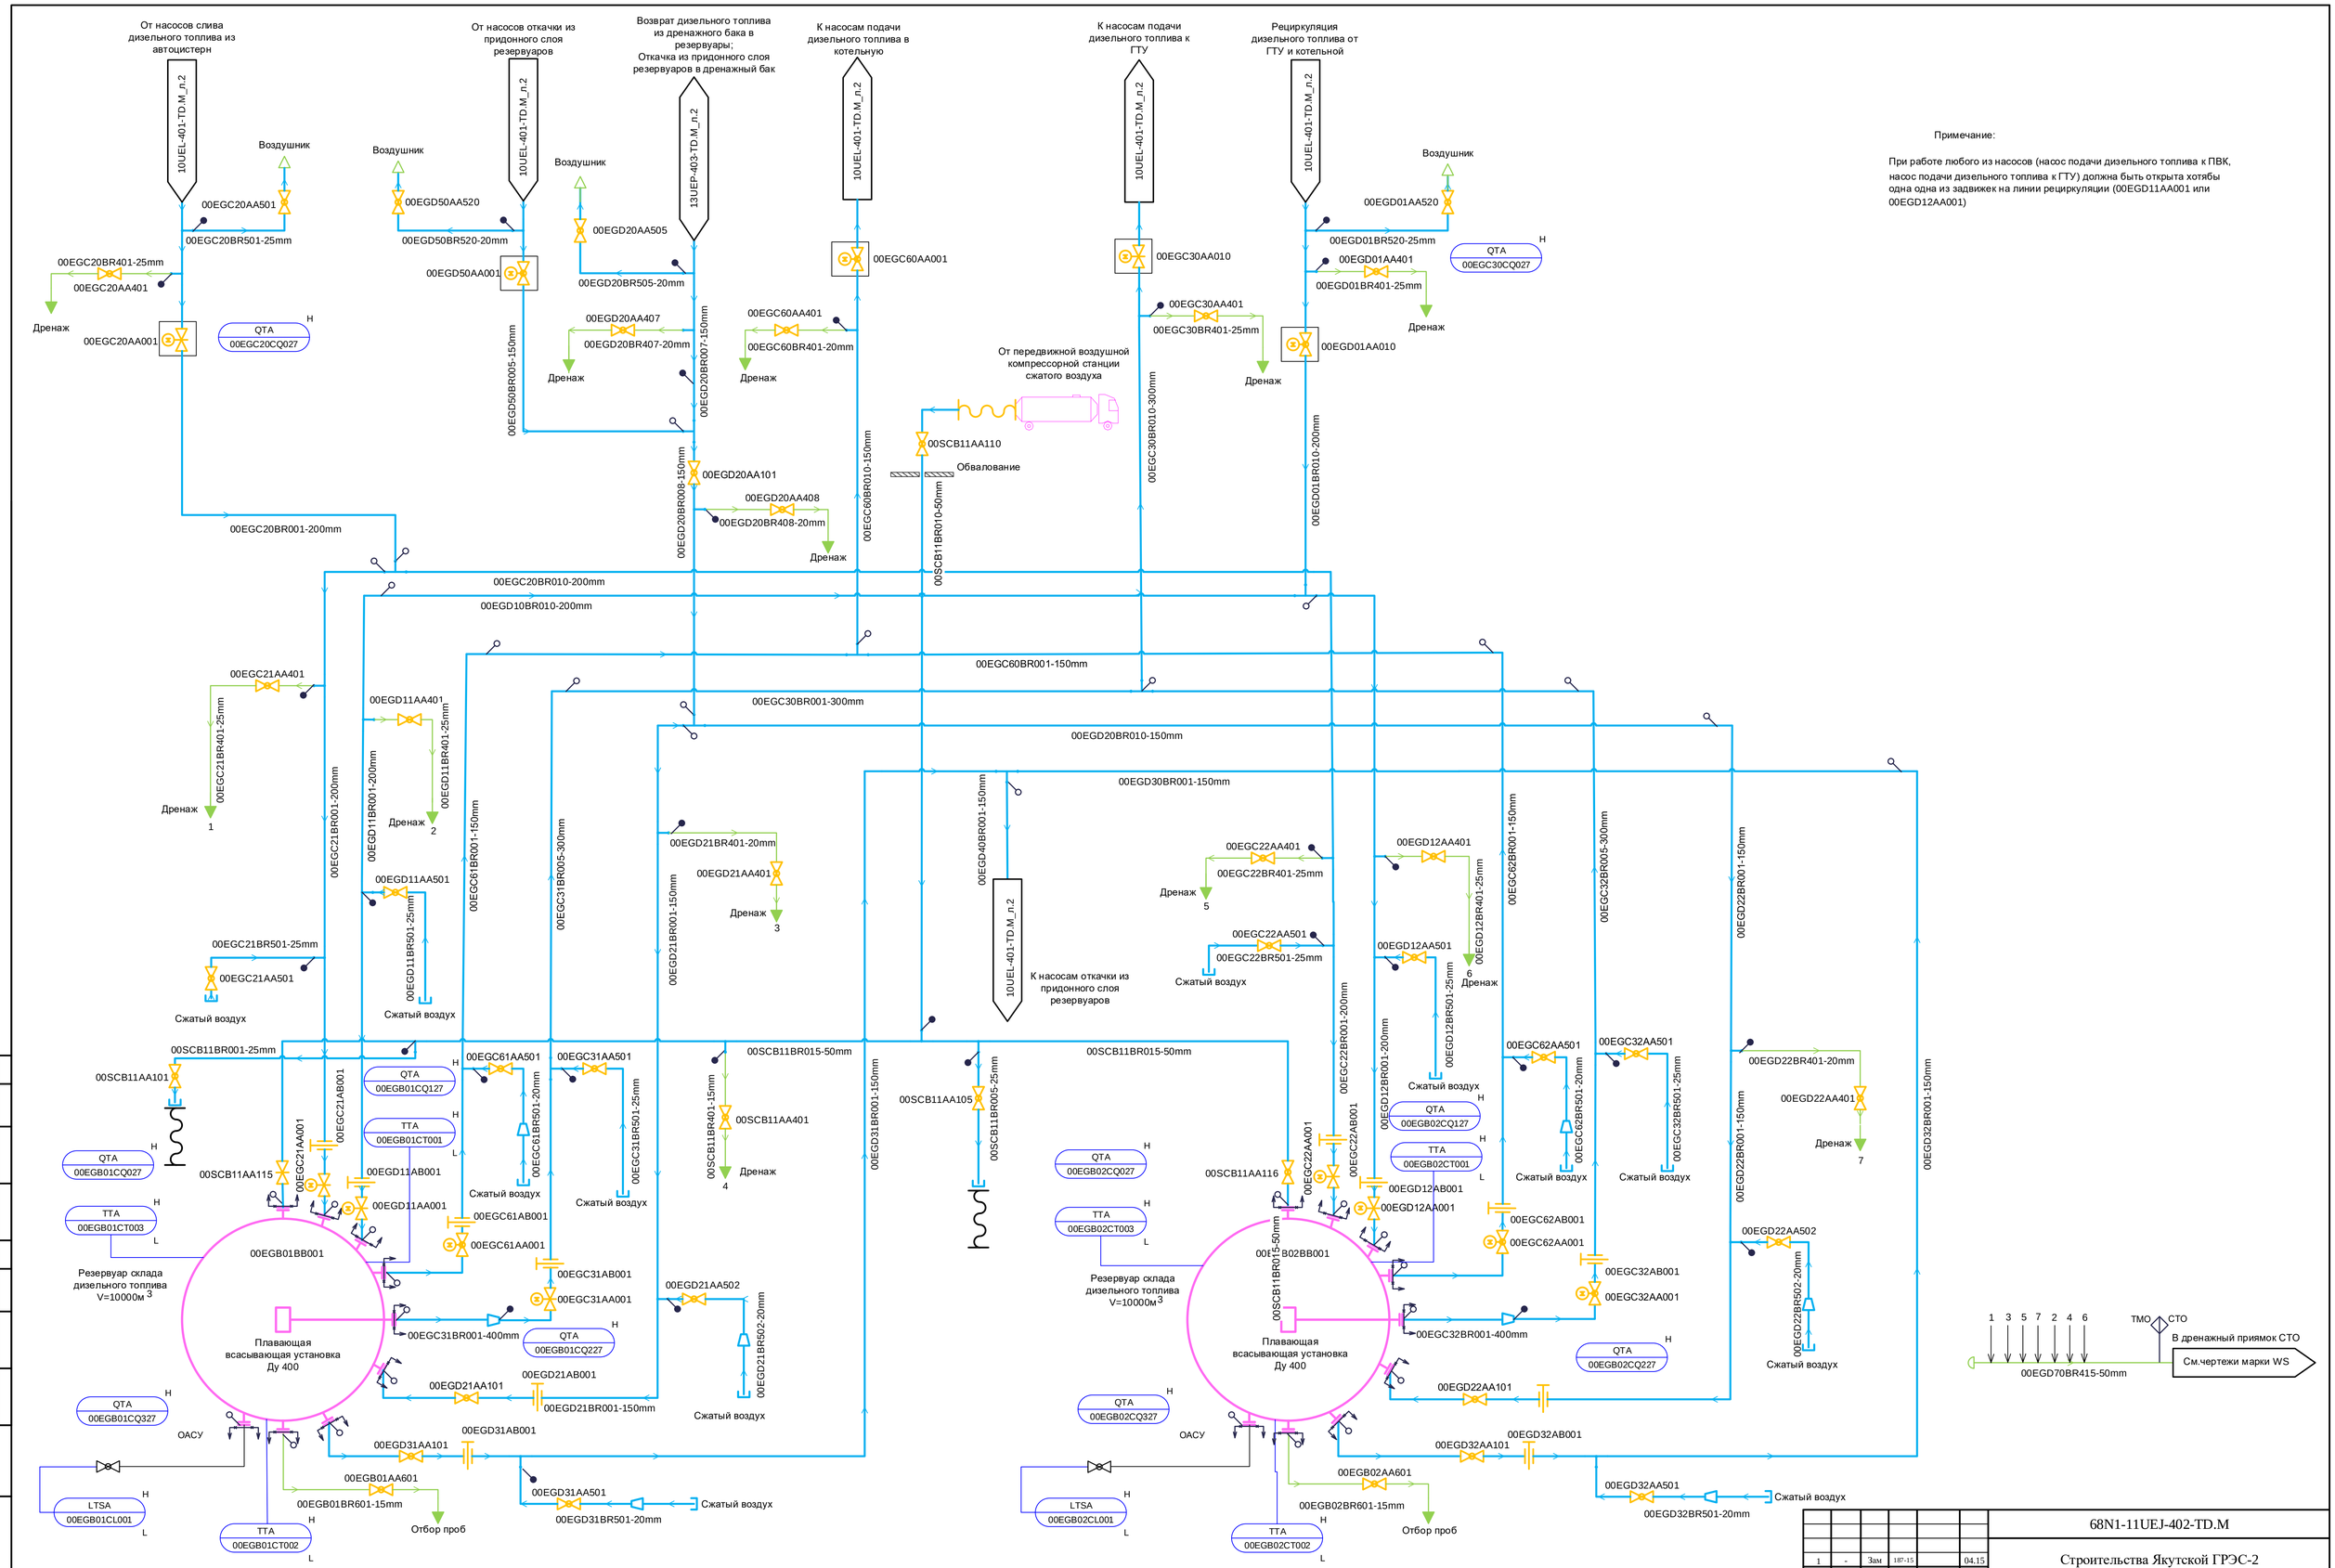

Примечание:

При работе любого из насосов (насос подачи дизельного топлива к ПВК, насос подачи дизельного топлива к ГТУ) должна быть открыта хотябы одна одна из задвижек на линии рециркуляции (00EGD11AA001 или 00EGD12AA001)

1	-	Зам	187-15		04.15	68N1-11UEJ-402-TD.M
Изм.	Кол.уч	Лист	№ док.	Подп.	Дата	Строительства Якутской ГРЭС-2

Разработал	Полянская	Хозяйство дизельного топлива PI-Диаграмма трубопроводов обвязки резервуаров склада дизельного топлива	Стадия: Р; Лист: 2; Листов:
Проверил	Бобров		
Гл.спец.	Стапура		
Н.контр.	Гридчина	PI-диаграмма трубопроводов обвязки резервуаров склада дизельного топлива. Система EGB, EGC, EGD	АКЦИОНЕРНОЕ ОБЩЕСТВО ИНСТИТУТ ТЕПЛОЭЛЕКТРОПРОЕКТ г. МОСКВА

Согласовано

Взам. инв. №

Подпись и дата

Инв. № подл.

Формат А1