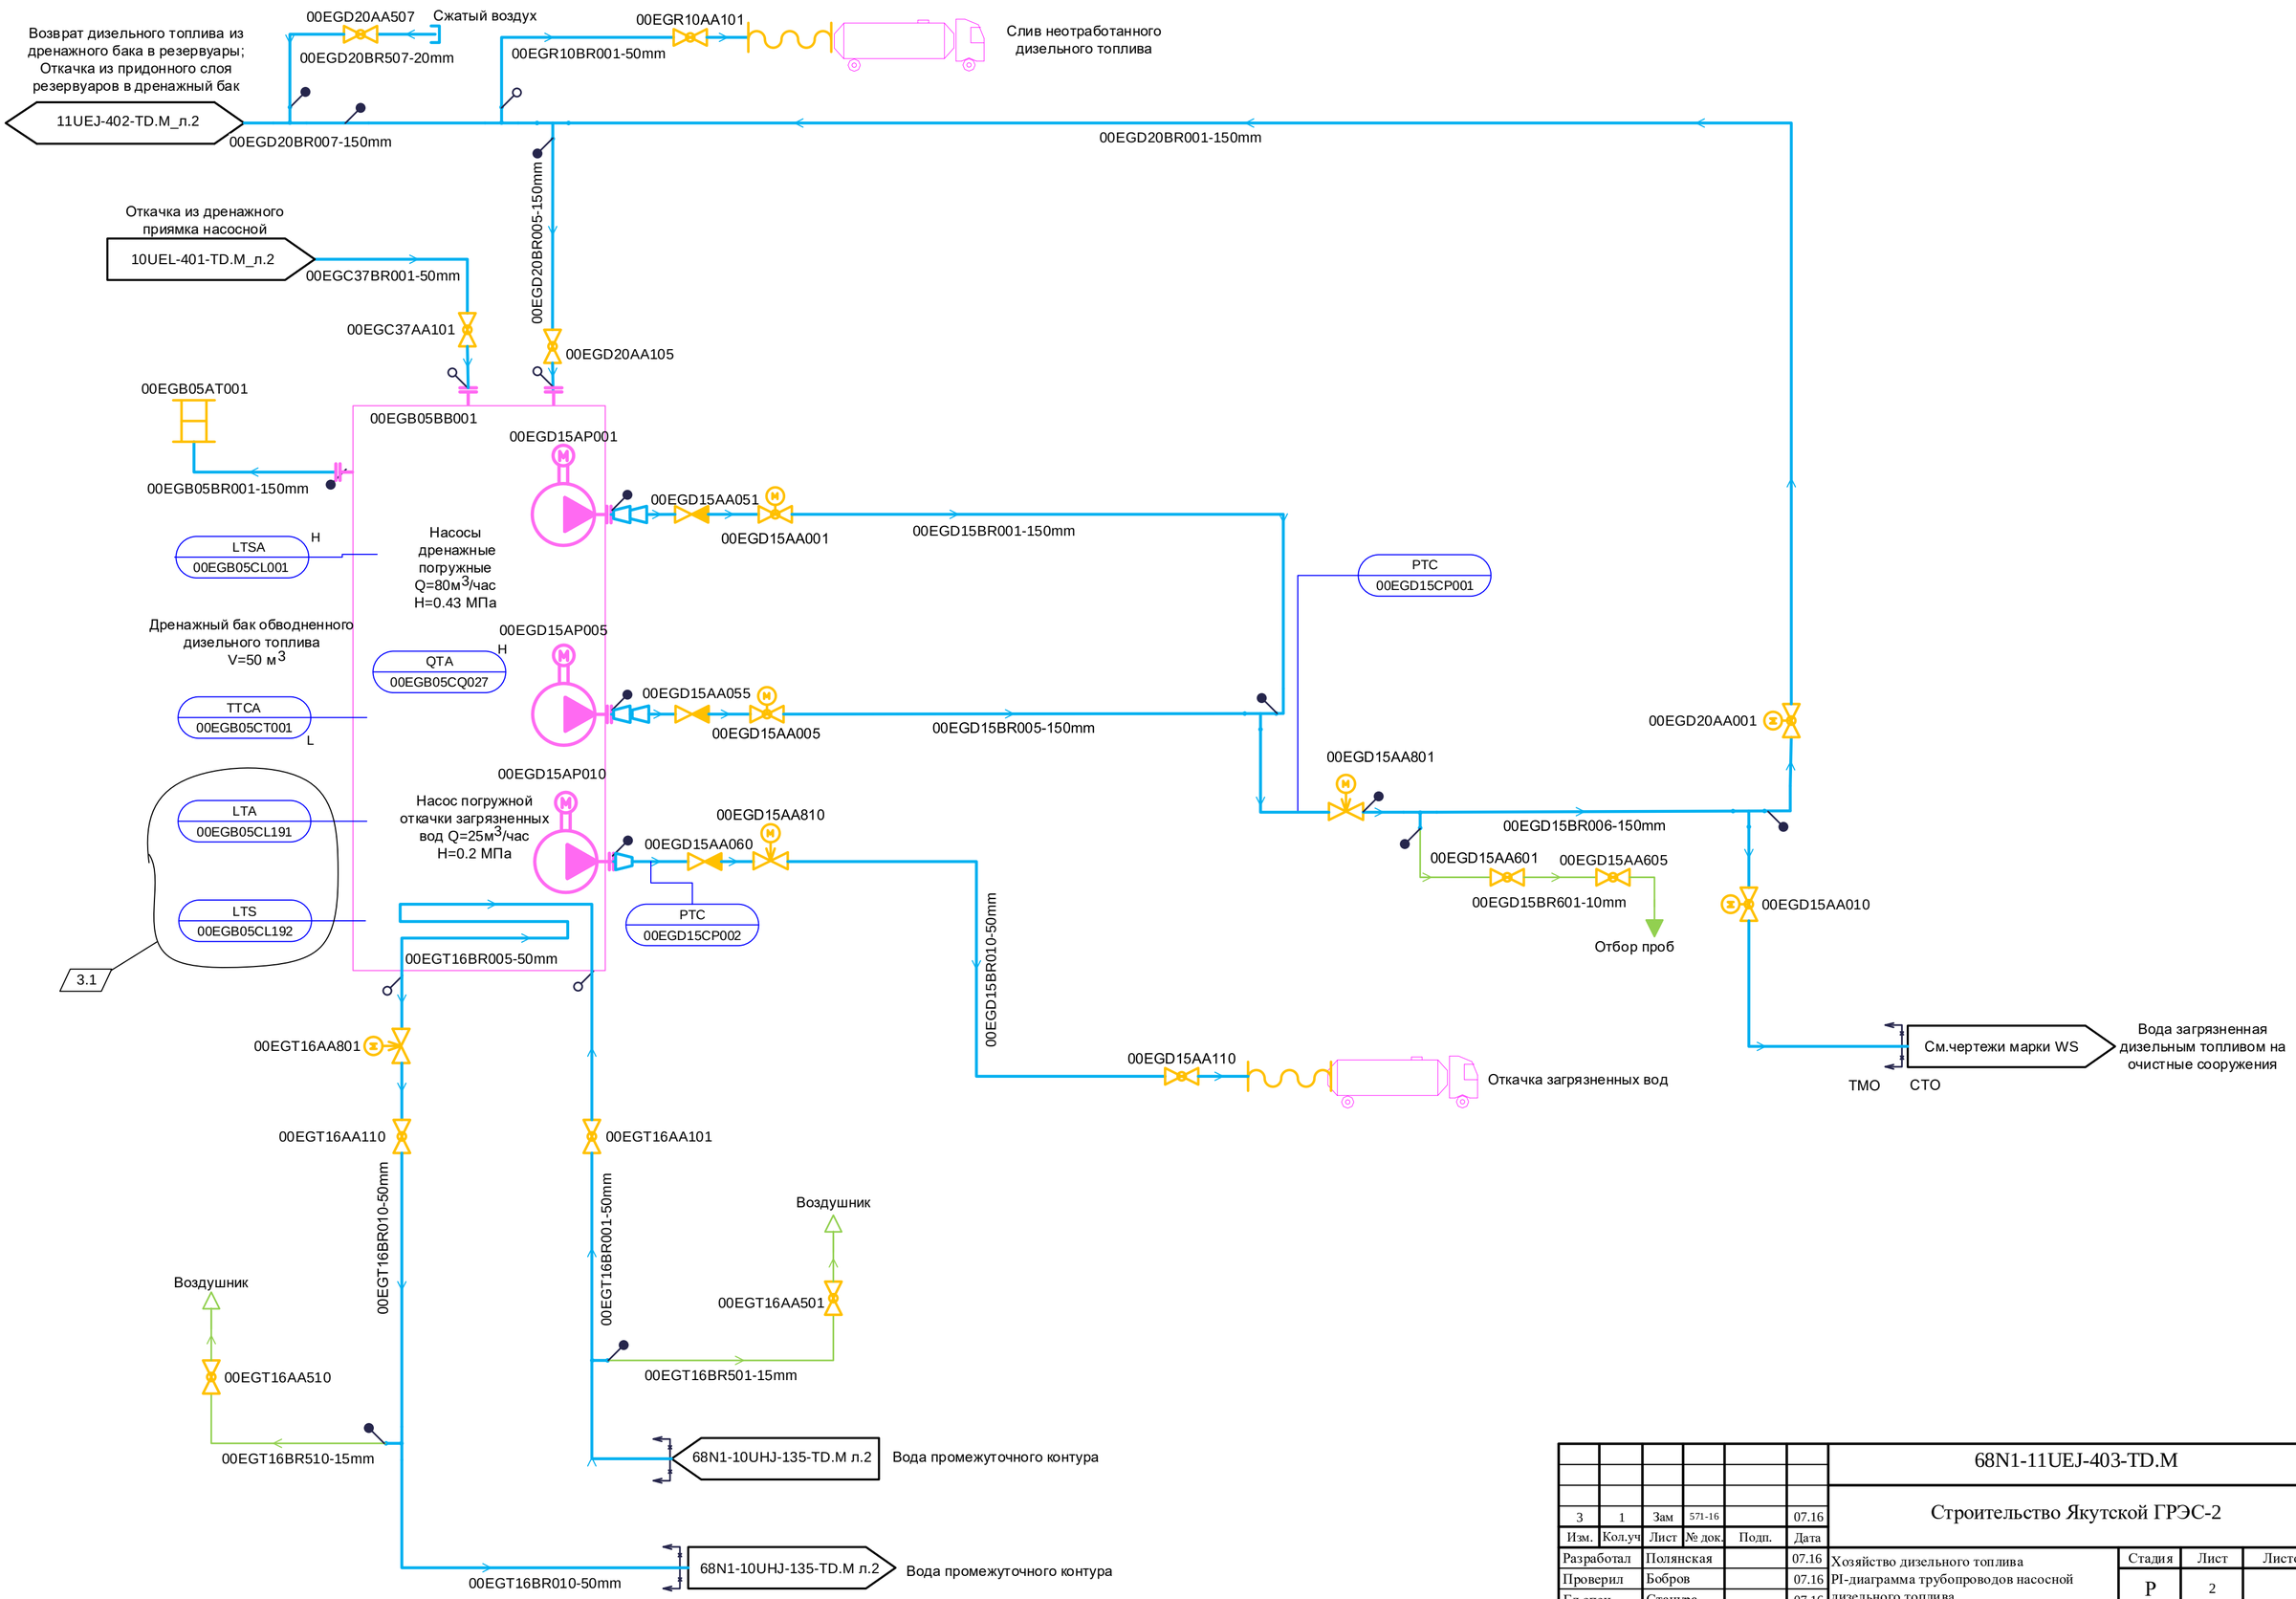

3	1	Зам	571-16		07.16	
Изм.	Кол.уч	Лист	№ док.	Подп.	Дата	
Разработал		Полянская			07.16	Хозяйство дизельного топлива PI-диаграмма трубопроводов насосной дизельного топлива
Проверил		Бобров			07.16	
Гл.спец		Стацура			07.16	
Н. контр.		Зеленина			07.16	PI-Диаграмма трубопроводов обвязки дренажного бака обводненного дизельного топлива. Система EGB, EGC, EGD

68N1-11UEJ-403-TD.M

Строительство Якутской ГРЭС-2

Стадия	Лист	Листов
Р	2	

АКЦИОНЕРНОЕ ОБЩЕСТВО ИНСТИТУТ ТЕПЛОЭЛЕКТРОПРОЕКТ Г. МОСКВА

Согласовано

ОАСУ

Взам. инв. №

Подпись и дата

Инв. № подл.

Формат А2