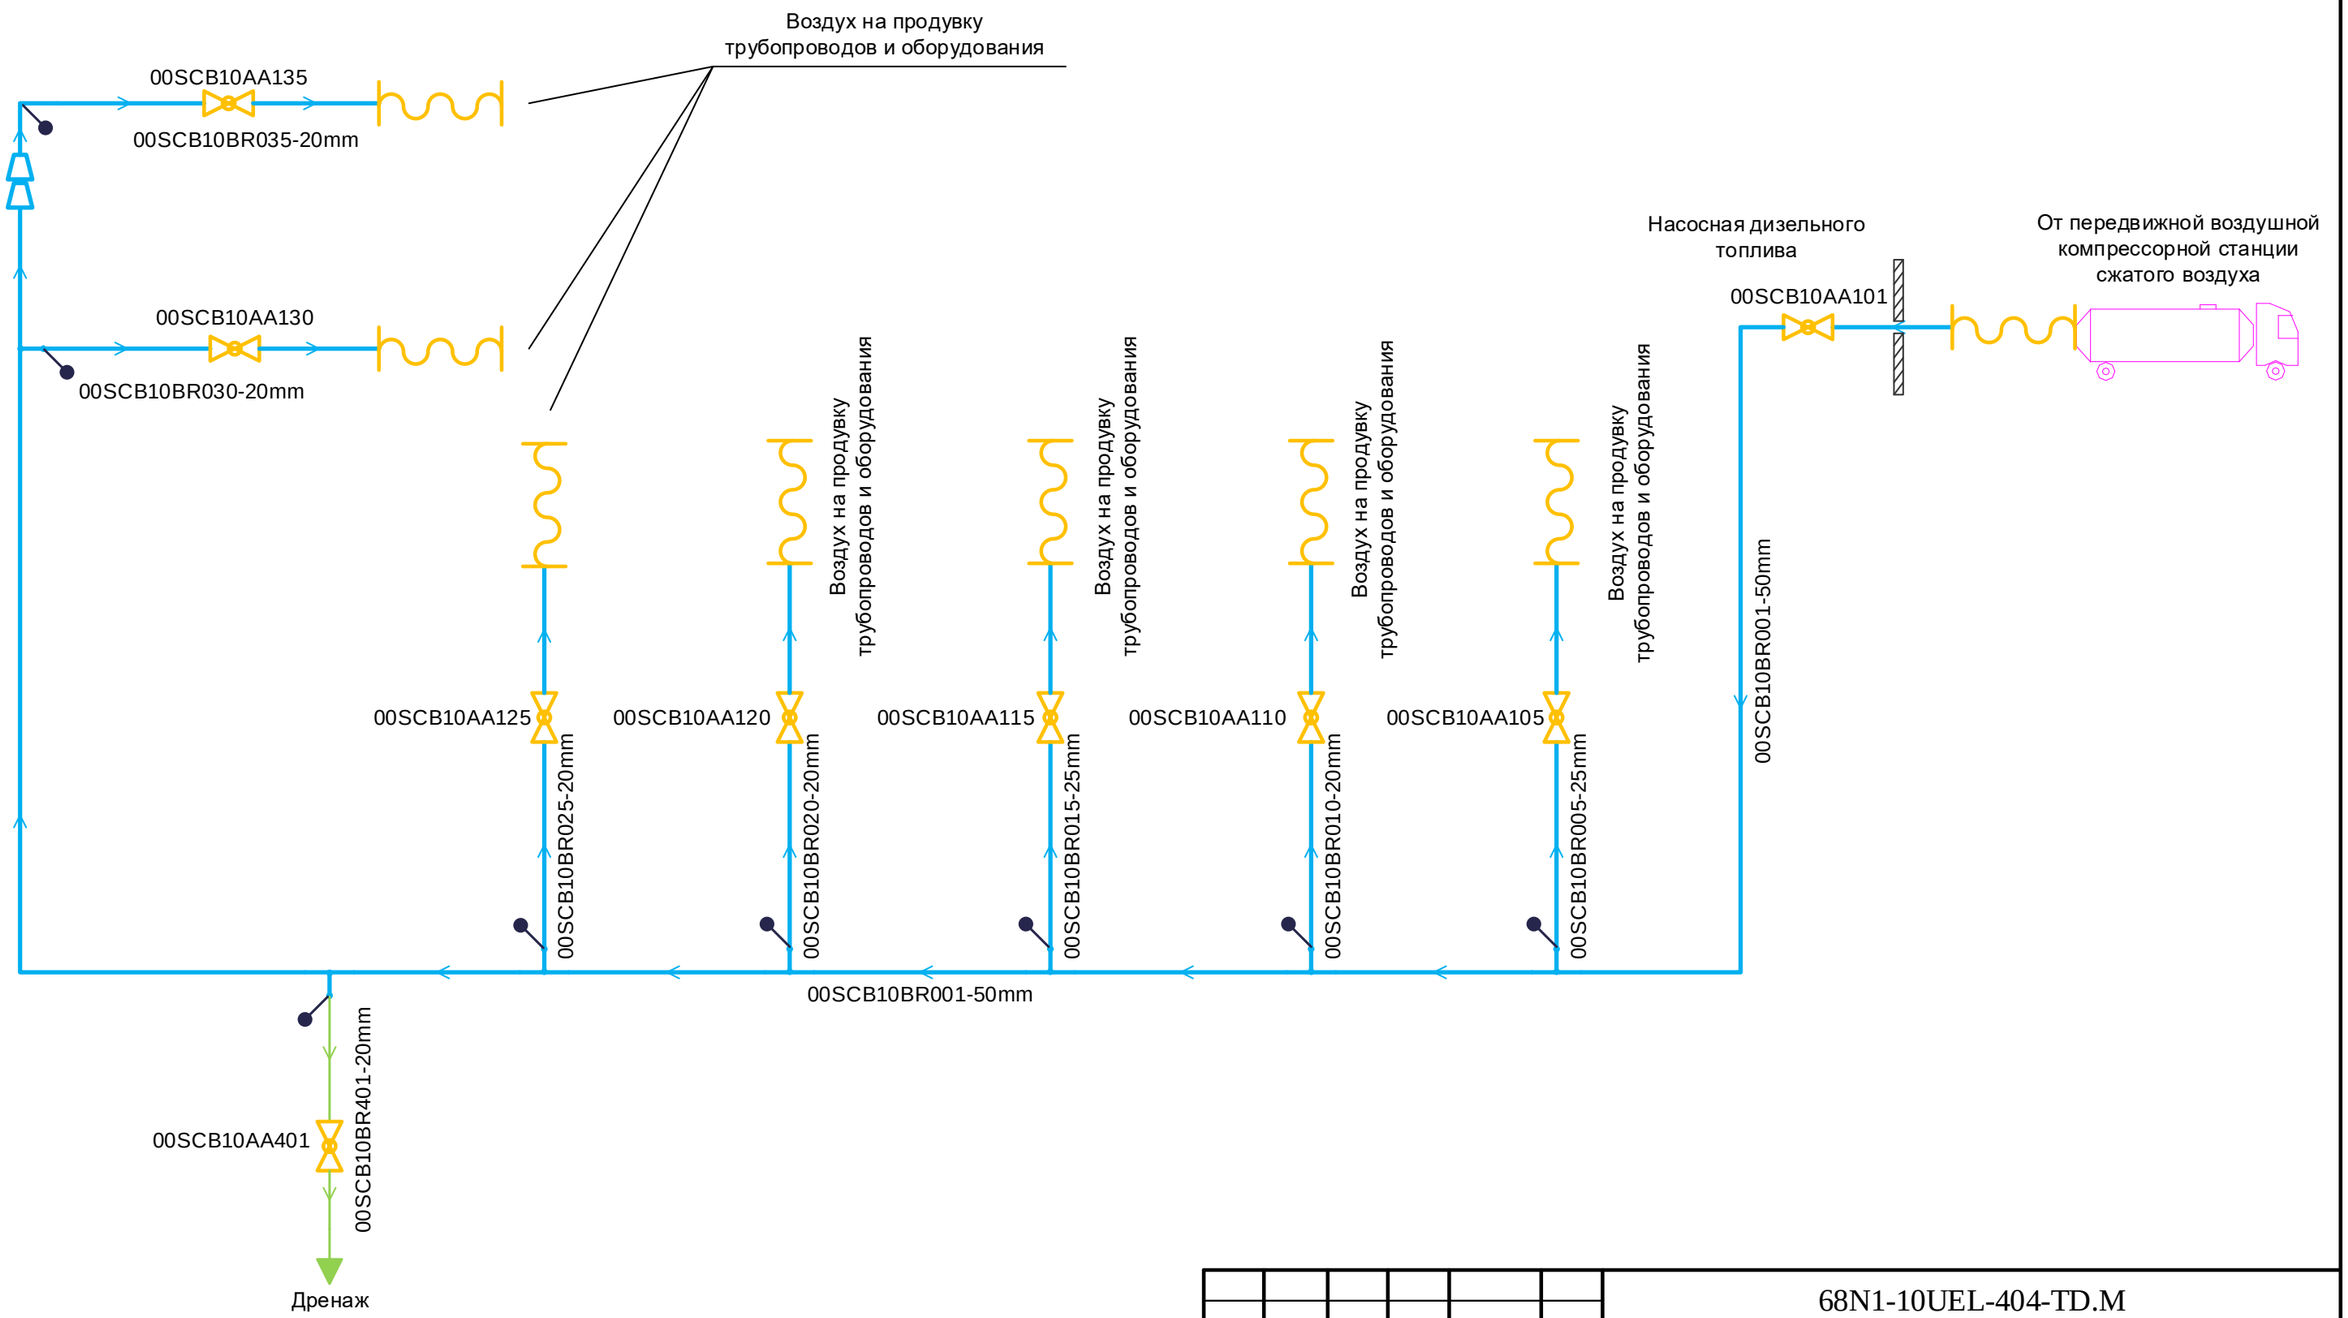

Согласовано

Взам. инв. №

Подпись и дата

Инв. № подл.

Изм.	Кол.уч	Лист	№ док.	Подп.	Дата
Разработал		Полянская			
Проверил		Стацура			
Н. контр.		Астраханцев			

68N1-10UEL-404-TD.M

Строительство Якутской ГРЭС-2

Хозяйство дизельного топлива
PI-диаграмма трубопроводов сжатого воздуха насосной дизельного топлива

Стадия	Лист	Листов
Р	2	

PI-диаграмма трубопроводов сжатого воздуха насосной дизельного топлива. Система SCB

ОТКРЫТОЕ АКЦИОНЕРНОЕ ОБЩЕСТВО ИНСТИТУТ ТЕПЛОЭЛЕКТРОПРОЕКТ МОСКВА

Формат А3