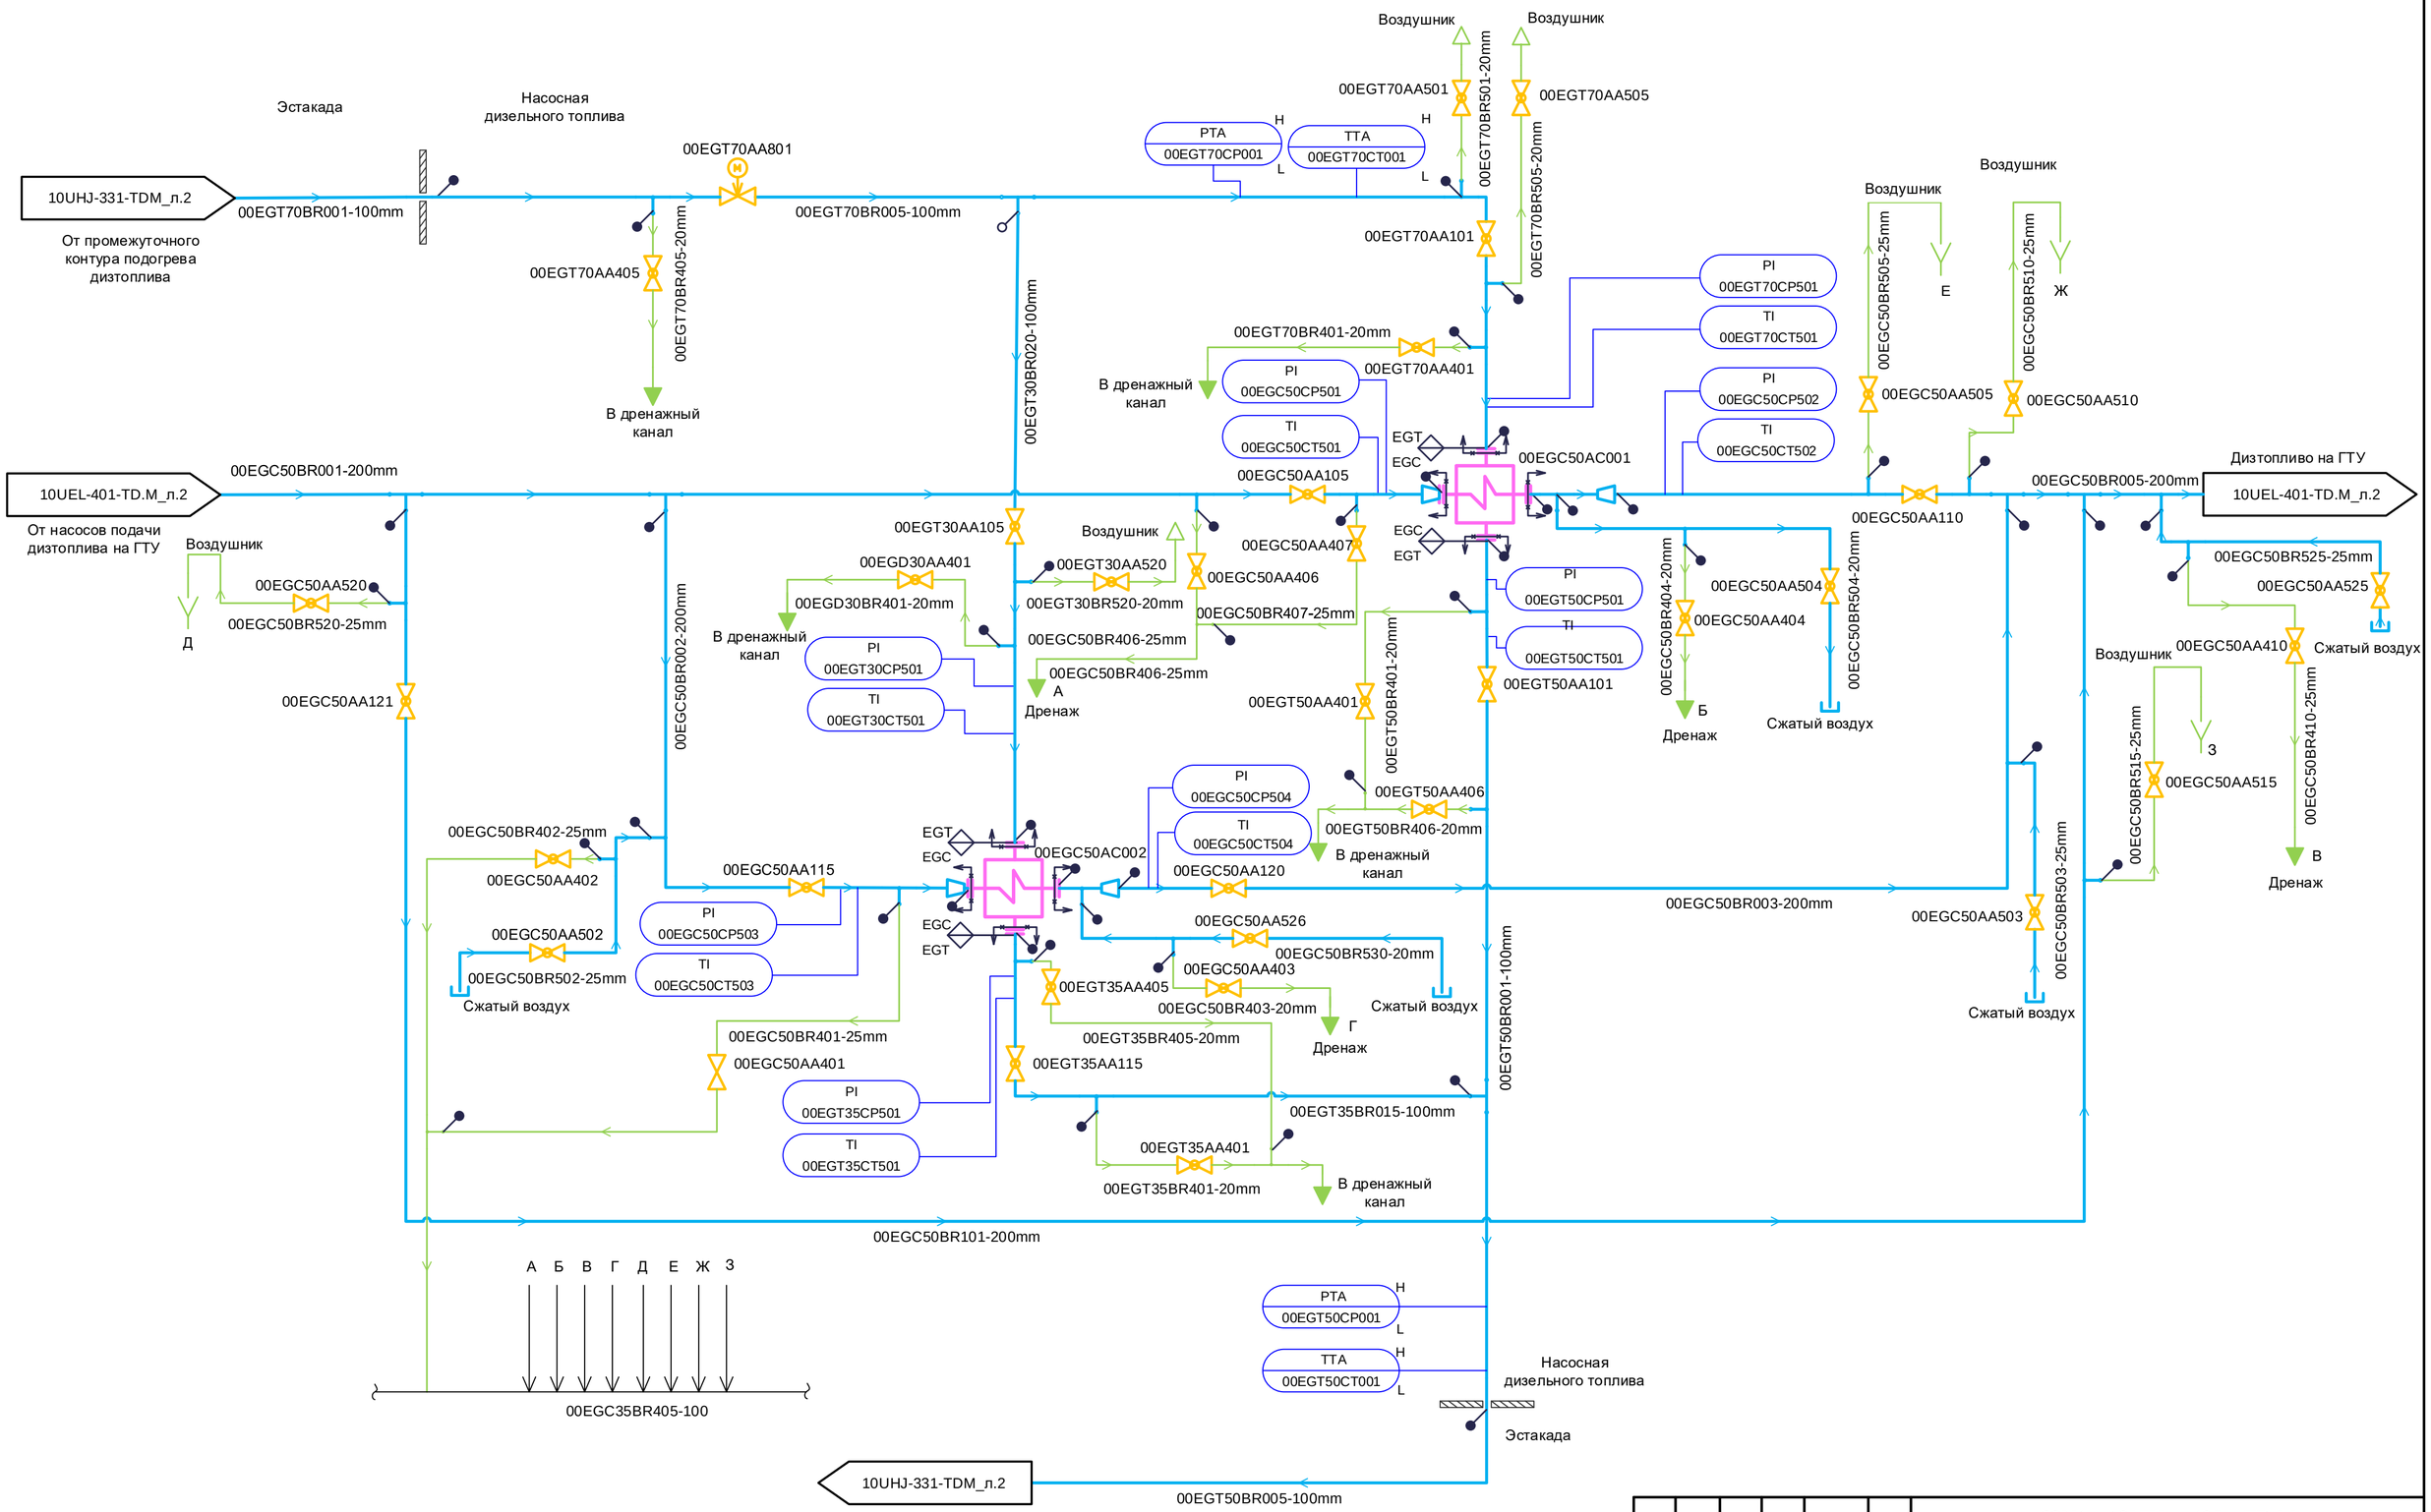

1	-	Зам	187-15			
Изм.	Кол.уч	Лист	№ док.	Подп.	Дата	
Разработал		Полянская				
Проверил		Бобров				
Гл.спец.		Стацура				
Н. контр.		Астраханцев				

68N1 – 10UEL – 405 – TD.M

Строительство Якутской ГРЭС-2

Хозяйство дизельного топлива
PI-диаграмма трубопроводов подогрева дизельного топлива

Стадия	Лист	Листов
Р	2	

PI-диаграмма трубопроводов подогрева дизельного топлива. Система EGC, EGT.

АКЦИОНЕРНОЕ ОБЩЕСТВО ИНСТИТУТ ТЕПЛОЭЛЕКТРОПРОЕКТ г. МОСКВА

Согласовано
ОАСУ Матяш

Взам. инв. №
Подпись и дата
Инв. № подл.

Формат А2