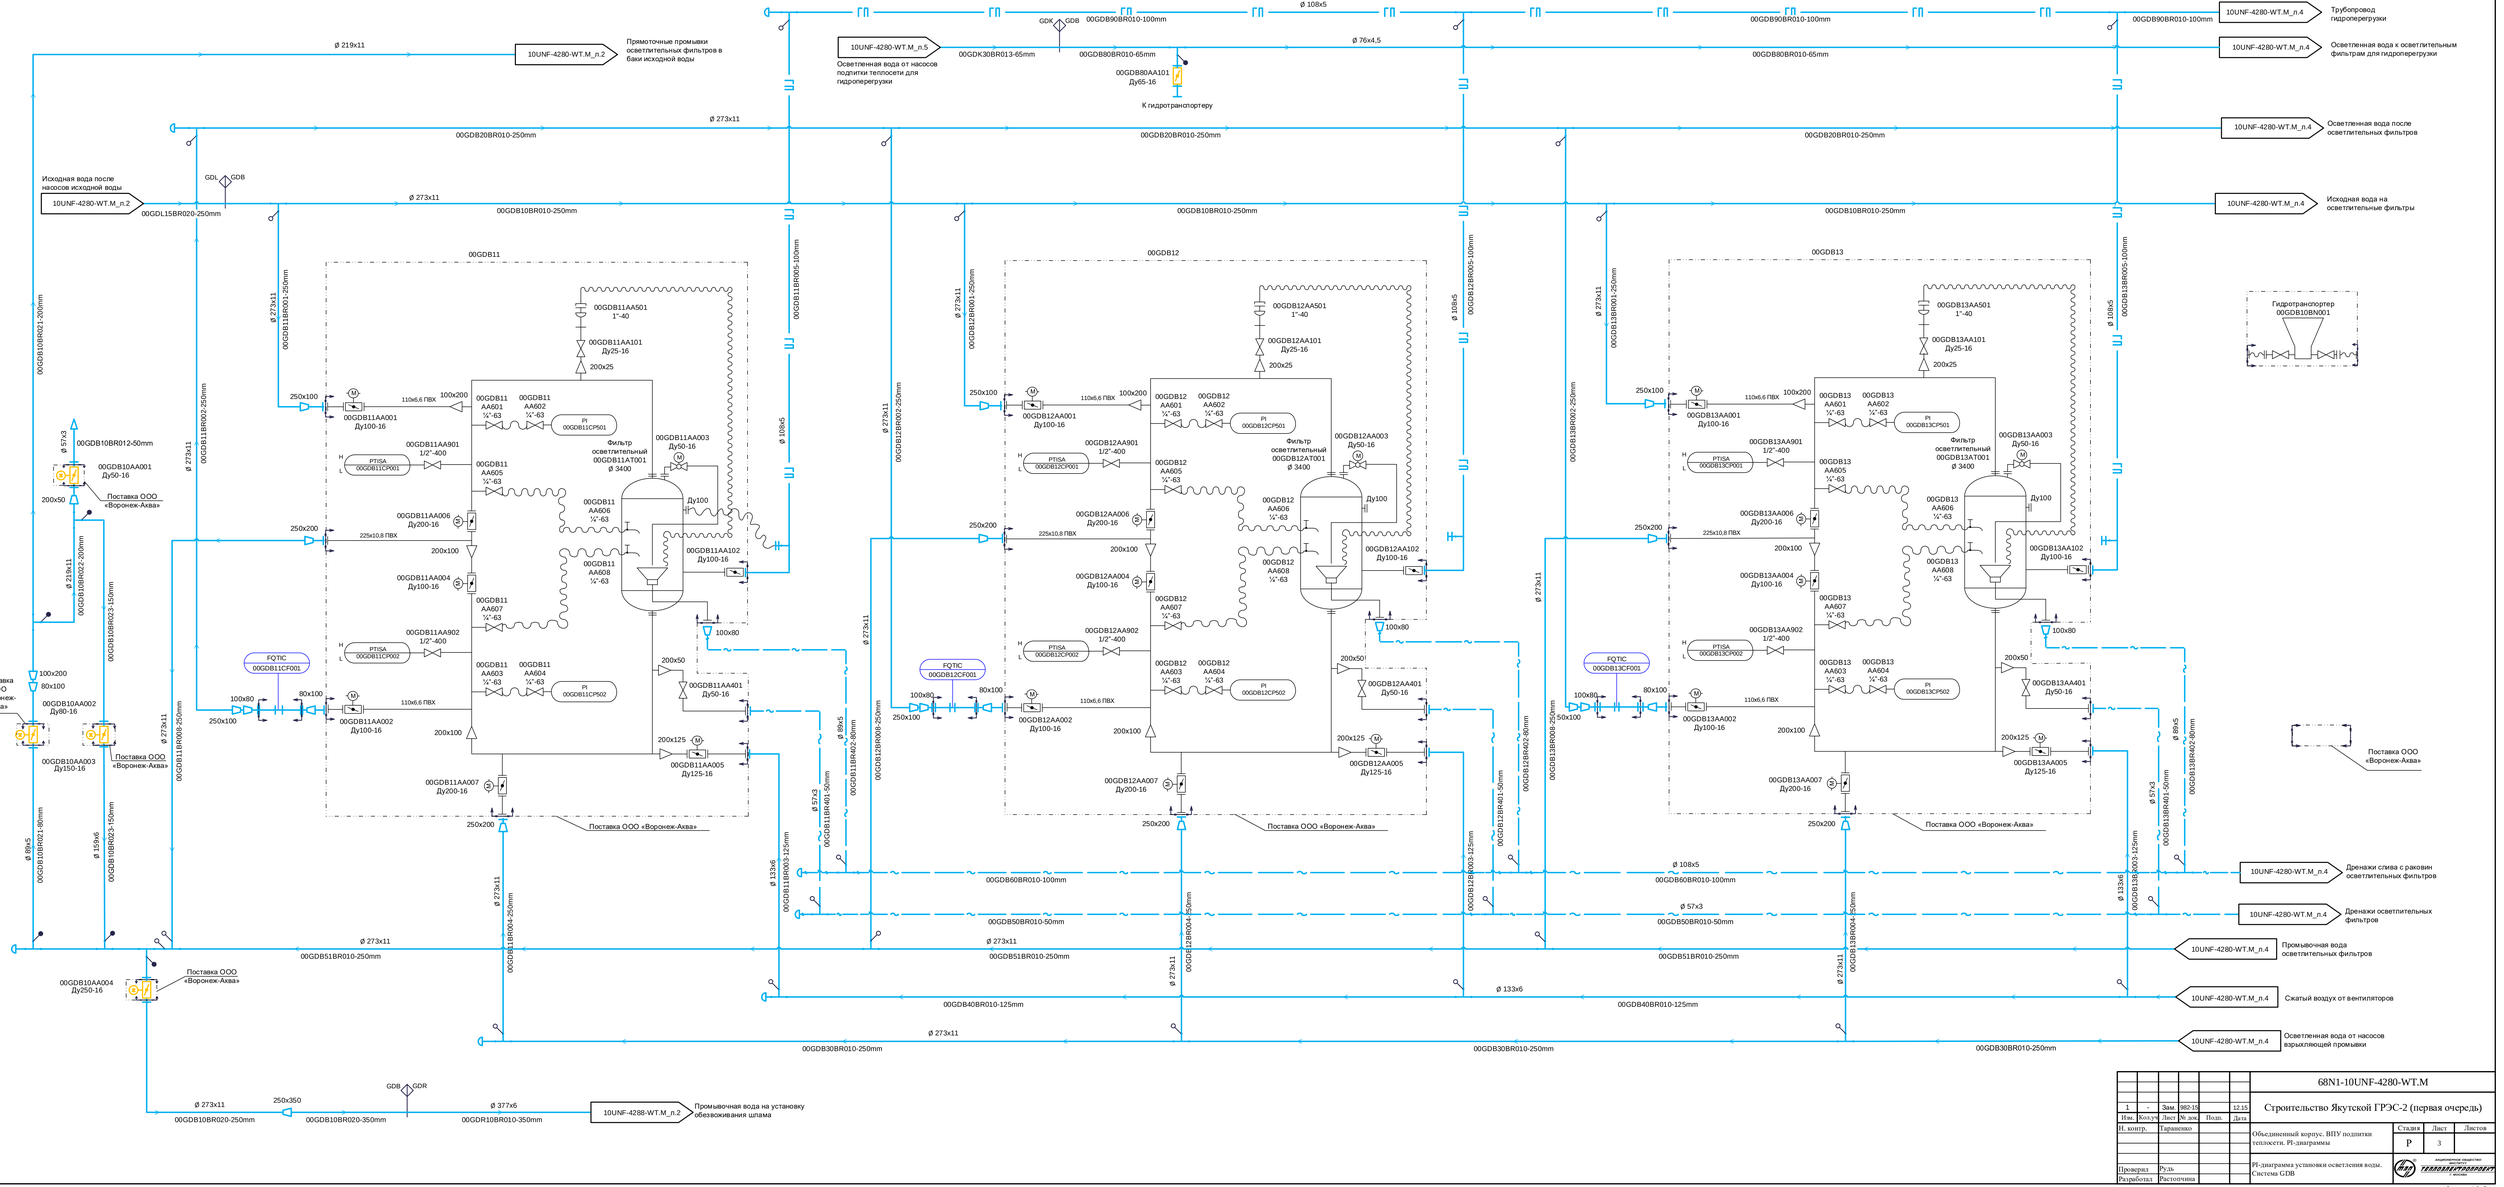

1	-	Зам.	982-15		12.15	68N1-10UNF-4280-WT.M
Изм.	Кол.уч.	Лист	№ док.	Подп.	Дата	Строительство Якутской ГРЭС-2 (первая очередь)
Н. контр.		Гаравенко				Объединенный корпус. ВПУ подпитки теплосети. PI-диаграммы
Проверил		Рудь				PI-диаграмма установки осветления воды. Система GDB
Разработал		Расточина				

Стадия	Лист	Листов
Р	3	

ТЕХНОПРОМЫШЛЕННОЕ ЛИЗИНГ

Согласовано

Взам. инв. №

Подпись и дата

Инв. № подл.

Формат А2х3