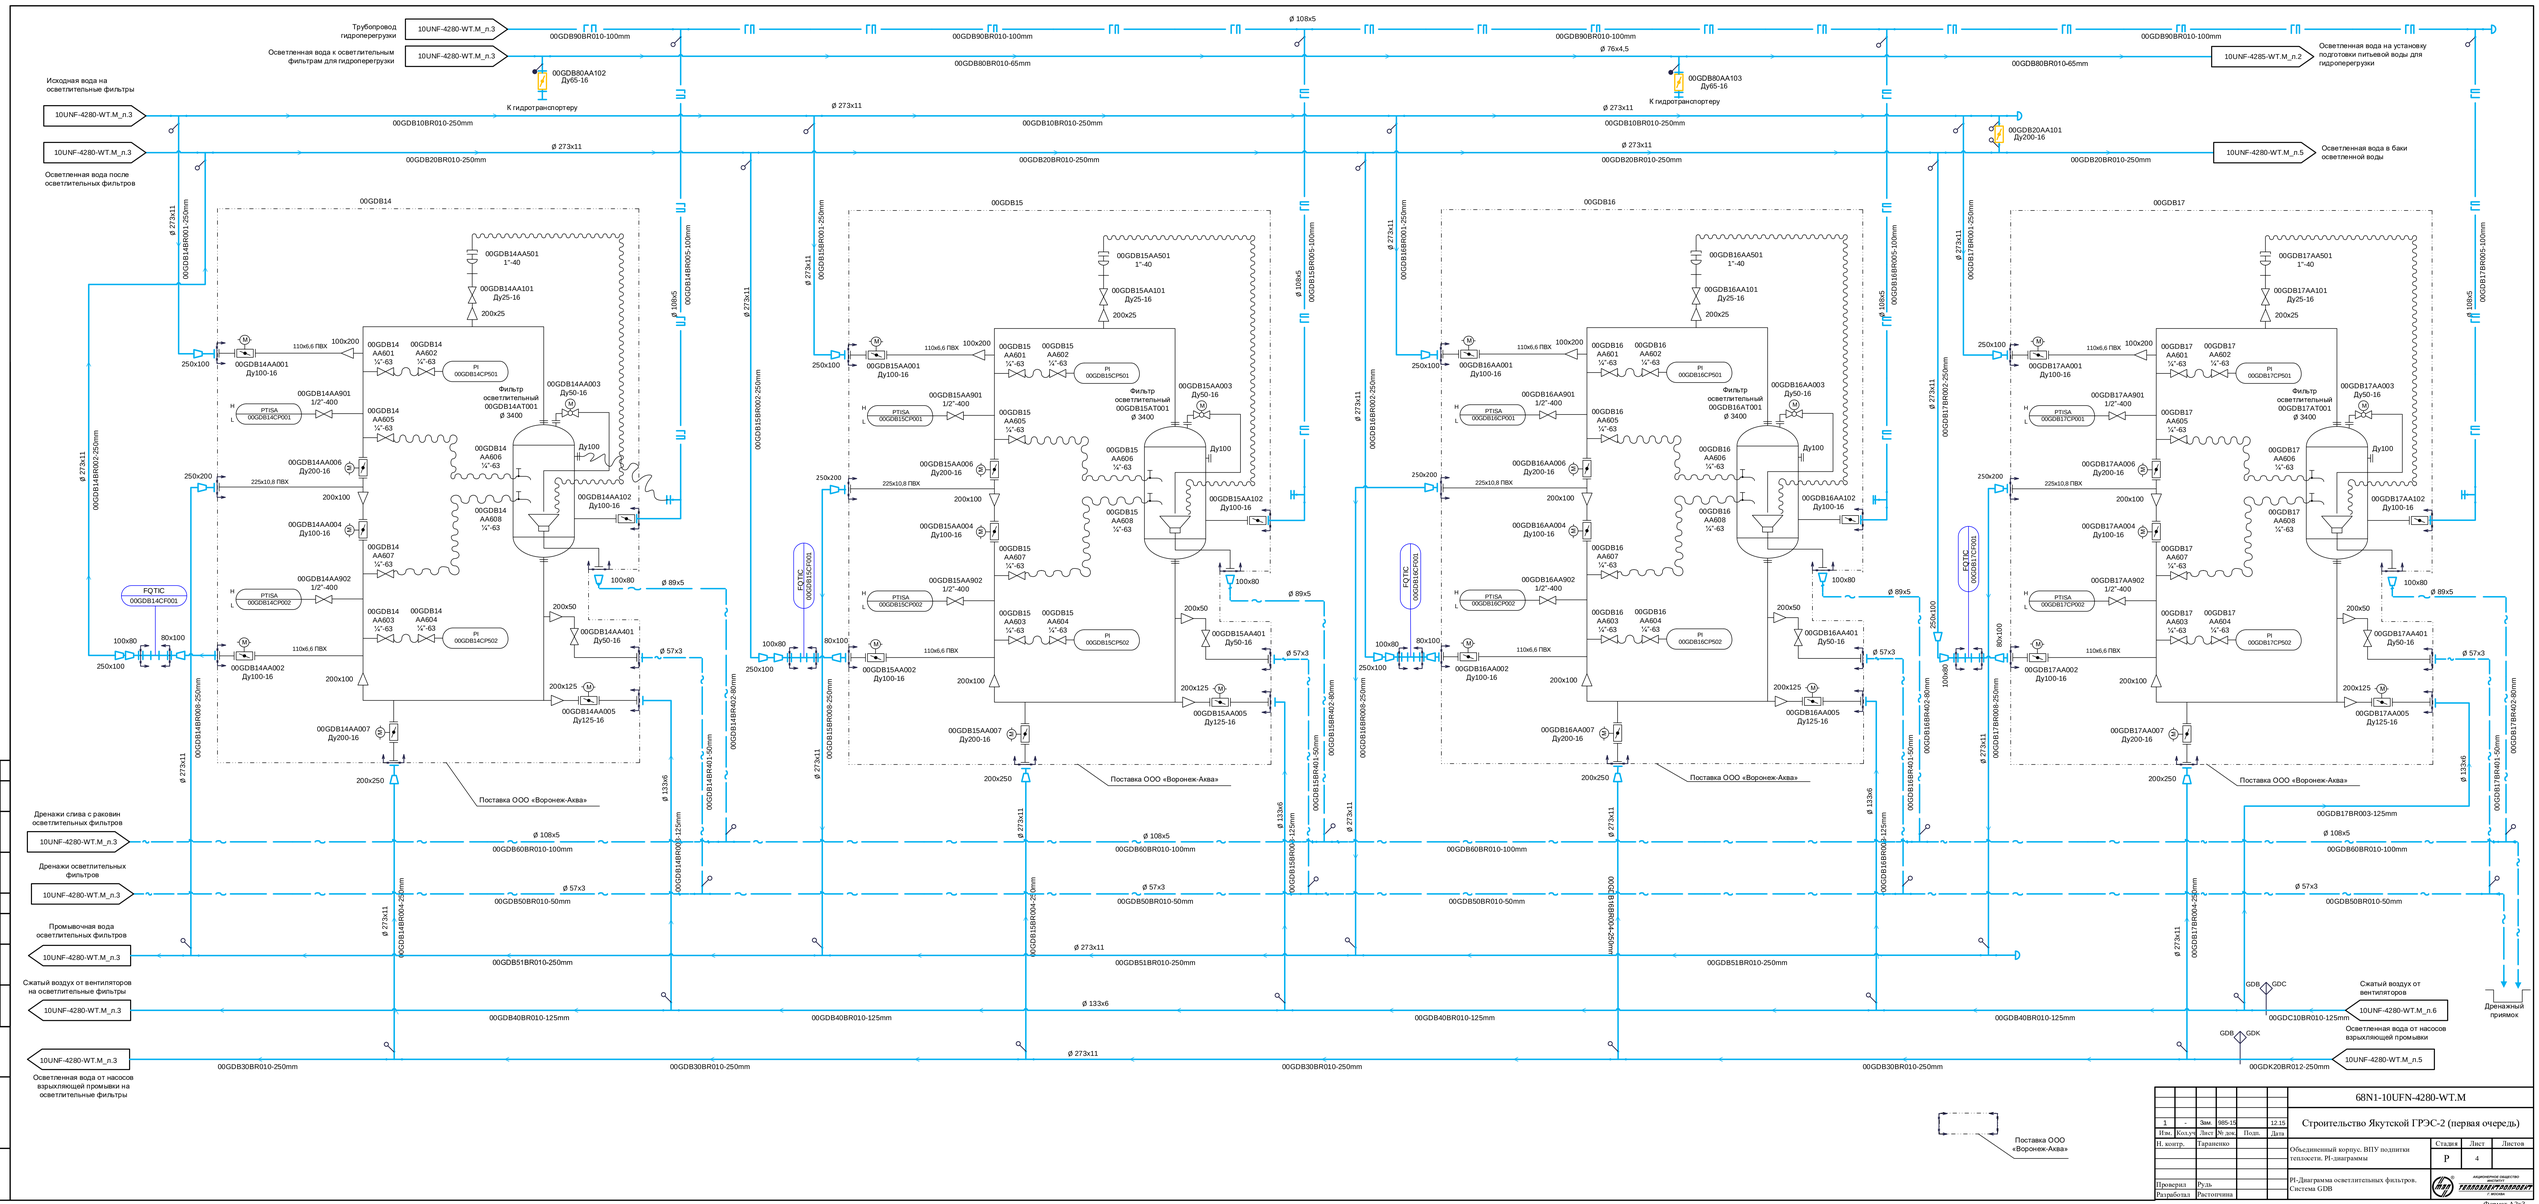

1	-	Зам.	985-15		12.15	68N1-10UFN-4280-WT.M
Изм.	Кол.уч.	Лист	№ док.	Подп.	Дата	Строительство Якутской ГРЭС-2 (первая очередь)
Н. контр.		Гаранекко				Объединенный корпус. ВПУ подпитки теплосети. PI-диаграммы
Проверил		Рузь				PI-Диаграмма осветлительных фильтров. Система GDB
Разработал		Расточтина				

Стадия	Лист	Листов
Р	4	

АКЦИОНЕРНОЕ ОБЩЕСТВО «ТЕХЭНЕРГОПРОГРЕСС»

Согласовано

Взам. инв. №

Подпись и дата

Инв. № подл.

Формат А2х3