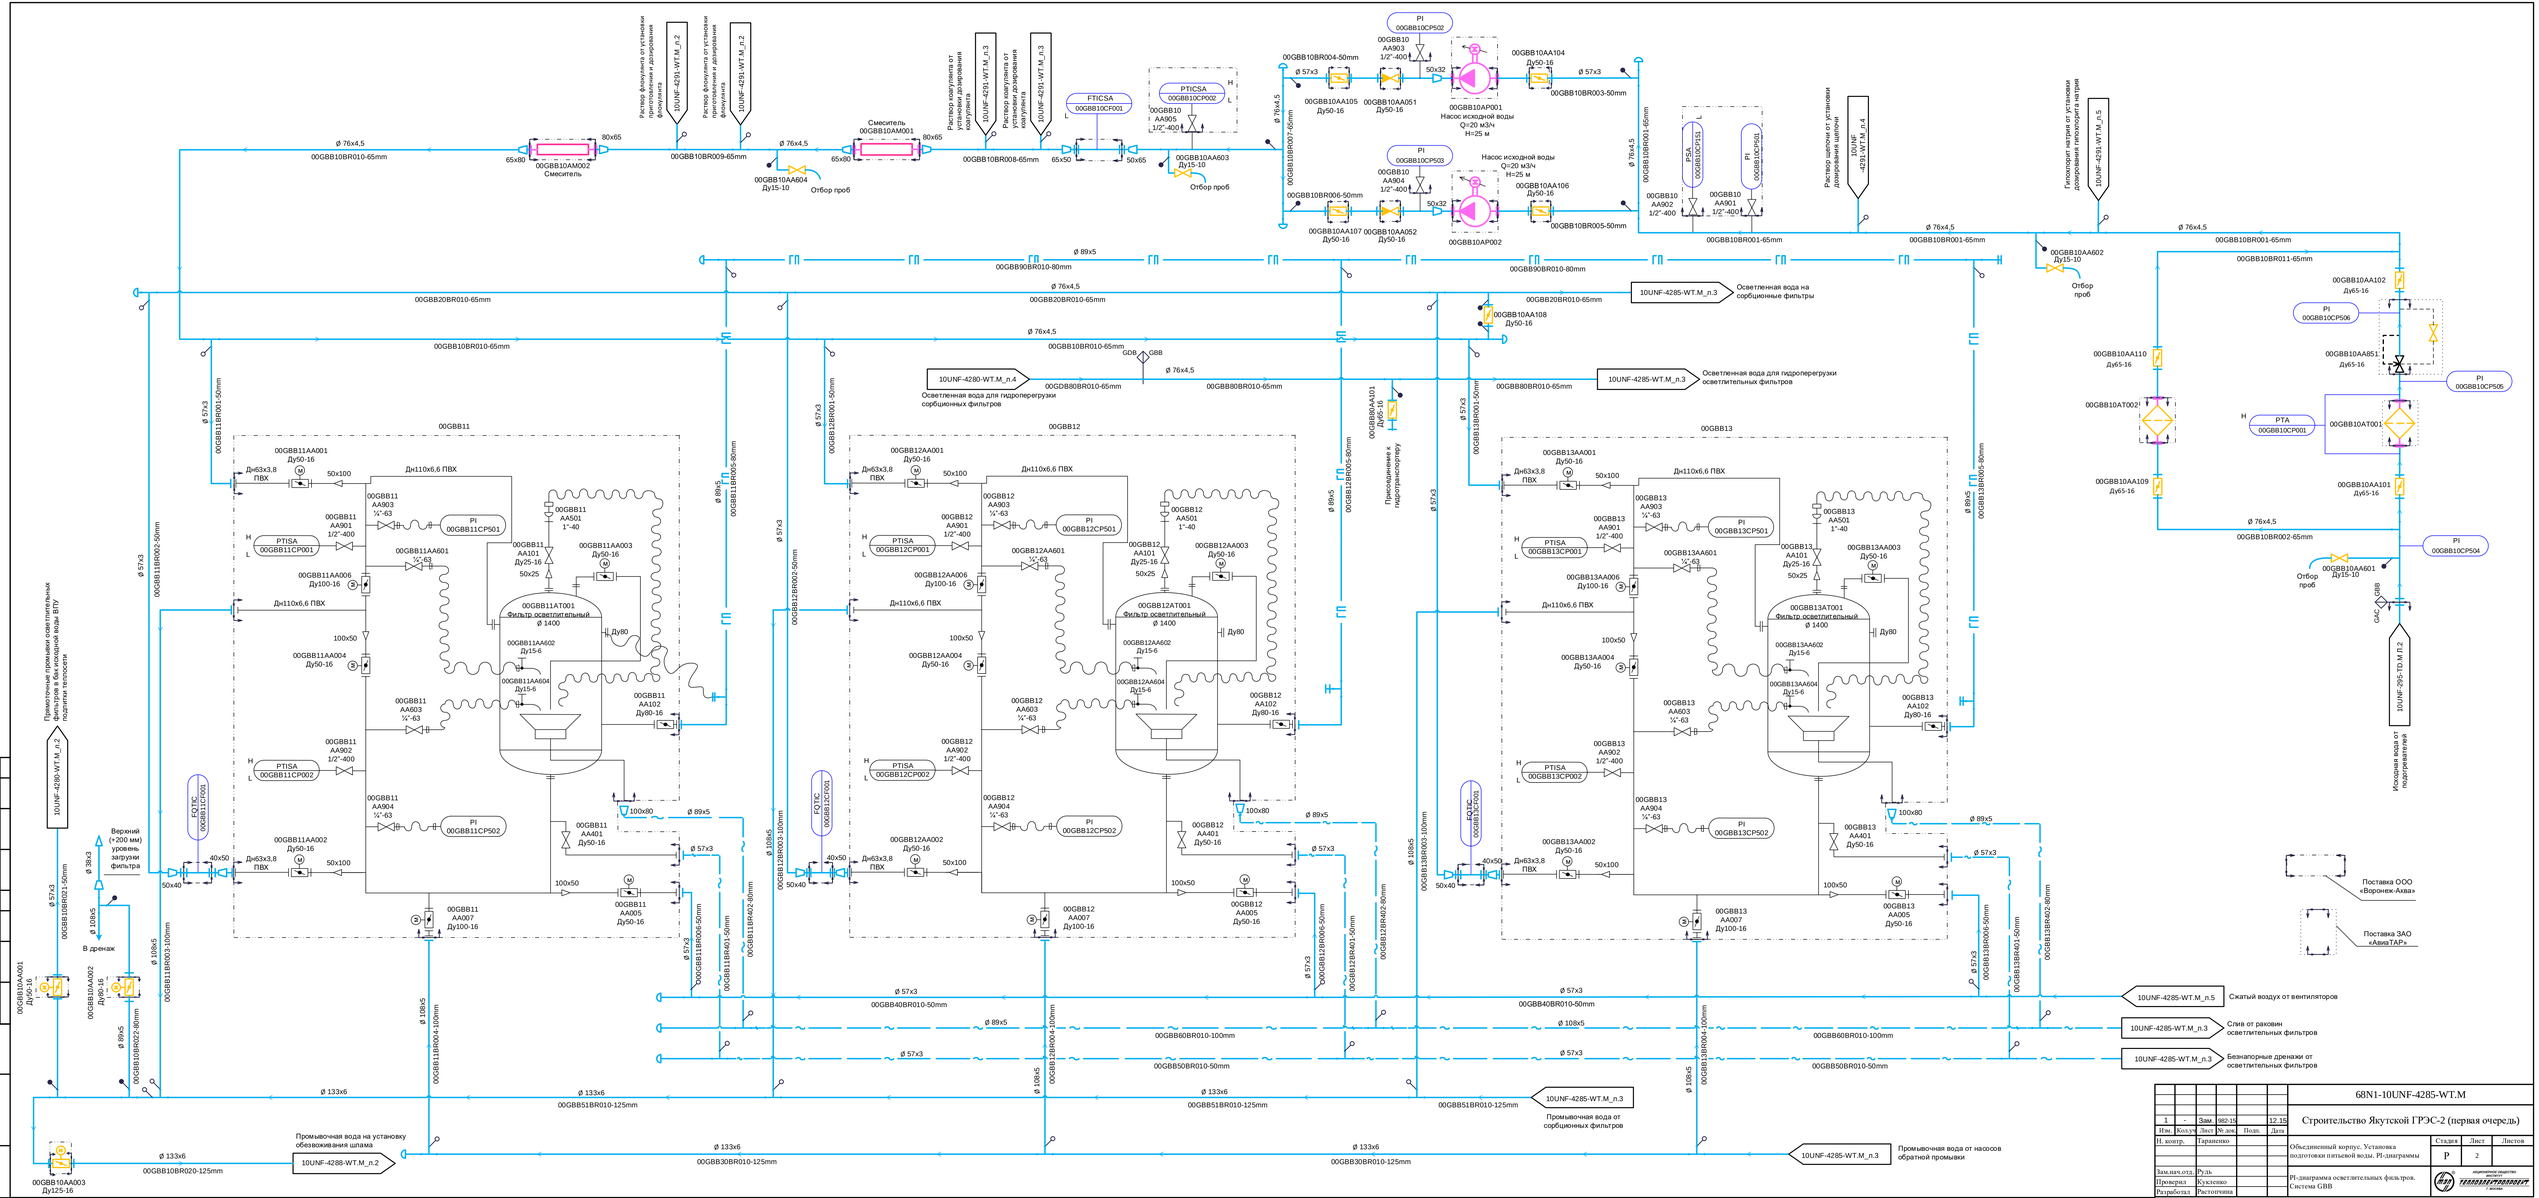

1	-	Зам.	882-15		12.15	
Изм.	Кол.уч.	Лист	№ док.	Подп.	Дата	

68N1-10UNF-4285-WT.M

Строительство Якутской ГРЭС-2 (первая очередь)

Объединенный корпус. Установка водоотводки питьевой воды. PI-диаграммы

Стадия	Лист	Листов
Р	2	

Н. контр.	Тараненко	
Зам.нач.отд.	Рудь	
Проверил	Кухленко	
Разработал	Ристочкина	

PI-диаграмма осветлительных фильтров. Система GBB

АКЦИОНЕРНОЕ ОБЩЕСТВО «ТЕХЭКСПРОМ»

Согласовано: ОАО"Гидроэнергопроект"

Взам. инв. №

Подпись и дата

Инв. № подл.

Формат А2х3