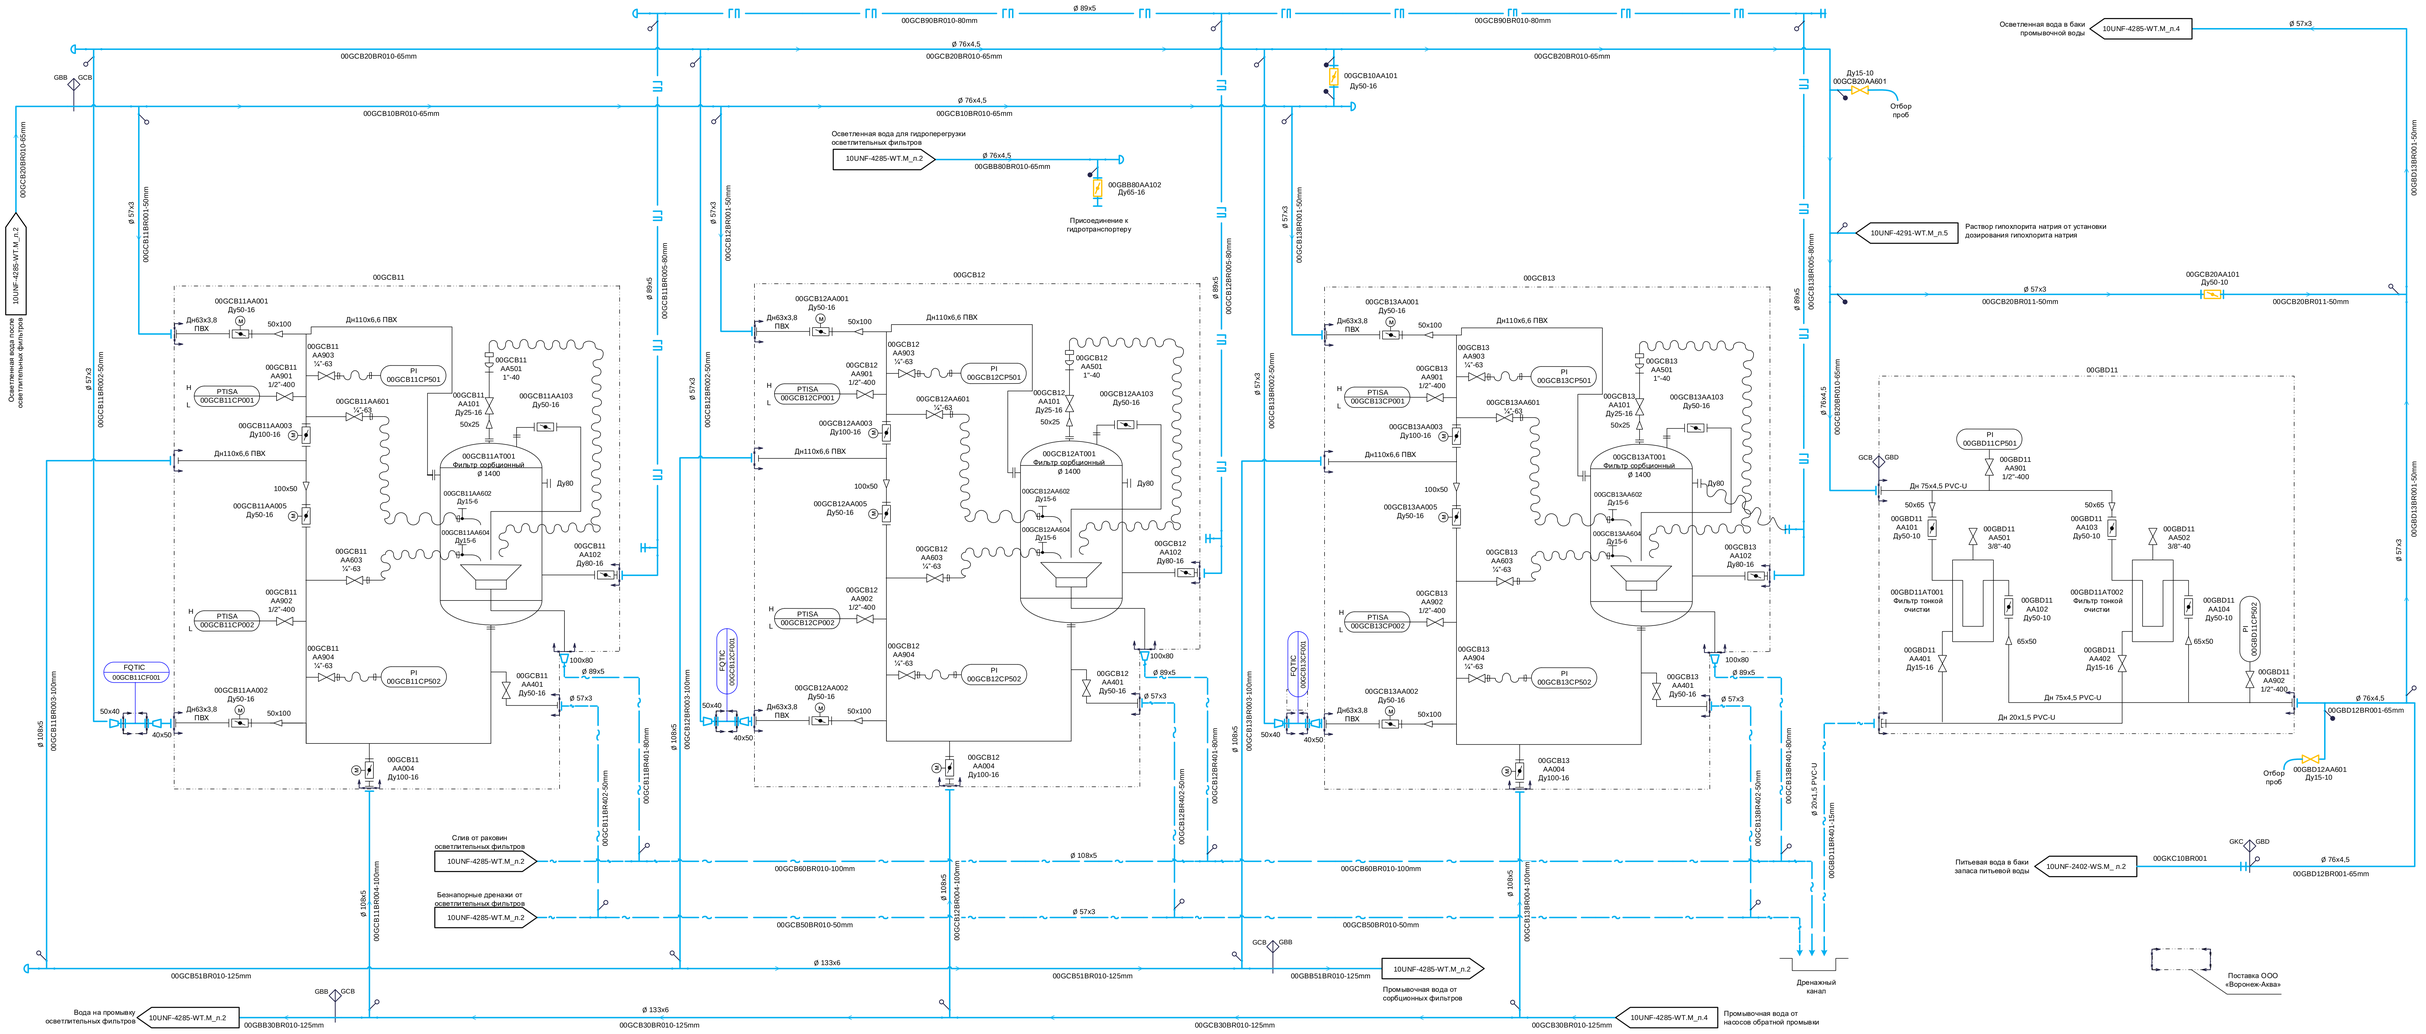

						68N1-10UNF-4285-WT.M
1	-	Зам.	682-15		12.15	Строительство Якутской ГРЭС-2 (первая очередь)
Изм.	Кол.уч.	Лист	№ док.	Подп.	Дата	
Н. контр.	Гаранскио					Объединенный корпус. Установка водоотвода питьевой воды. PI-диаграммы
Зам.нач.отд.	Рудь					PI-диаграмма сорбционных фильтров и фильтров тонкой очистки. Системы GCB, GBD
Проверил	Кусленко					
Разработал	Рыстогина					

Стадия	Лист	Листов
Р	3	

ГЕНЕРИРУЮЩАЯ КОМПАНИЯ РОСТЕХ
ТЕПЛОЭЛЕКТРОПРОЕКТ
ВОРОНЕЖ

Формат А2х3

Согласовано

Взам. инв. №

Подпись и дата

Инв. № подл.