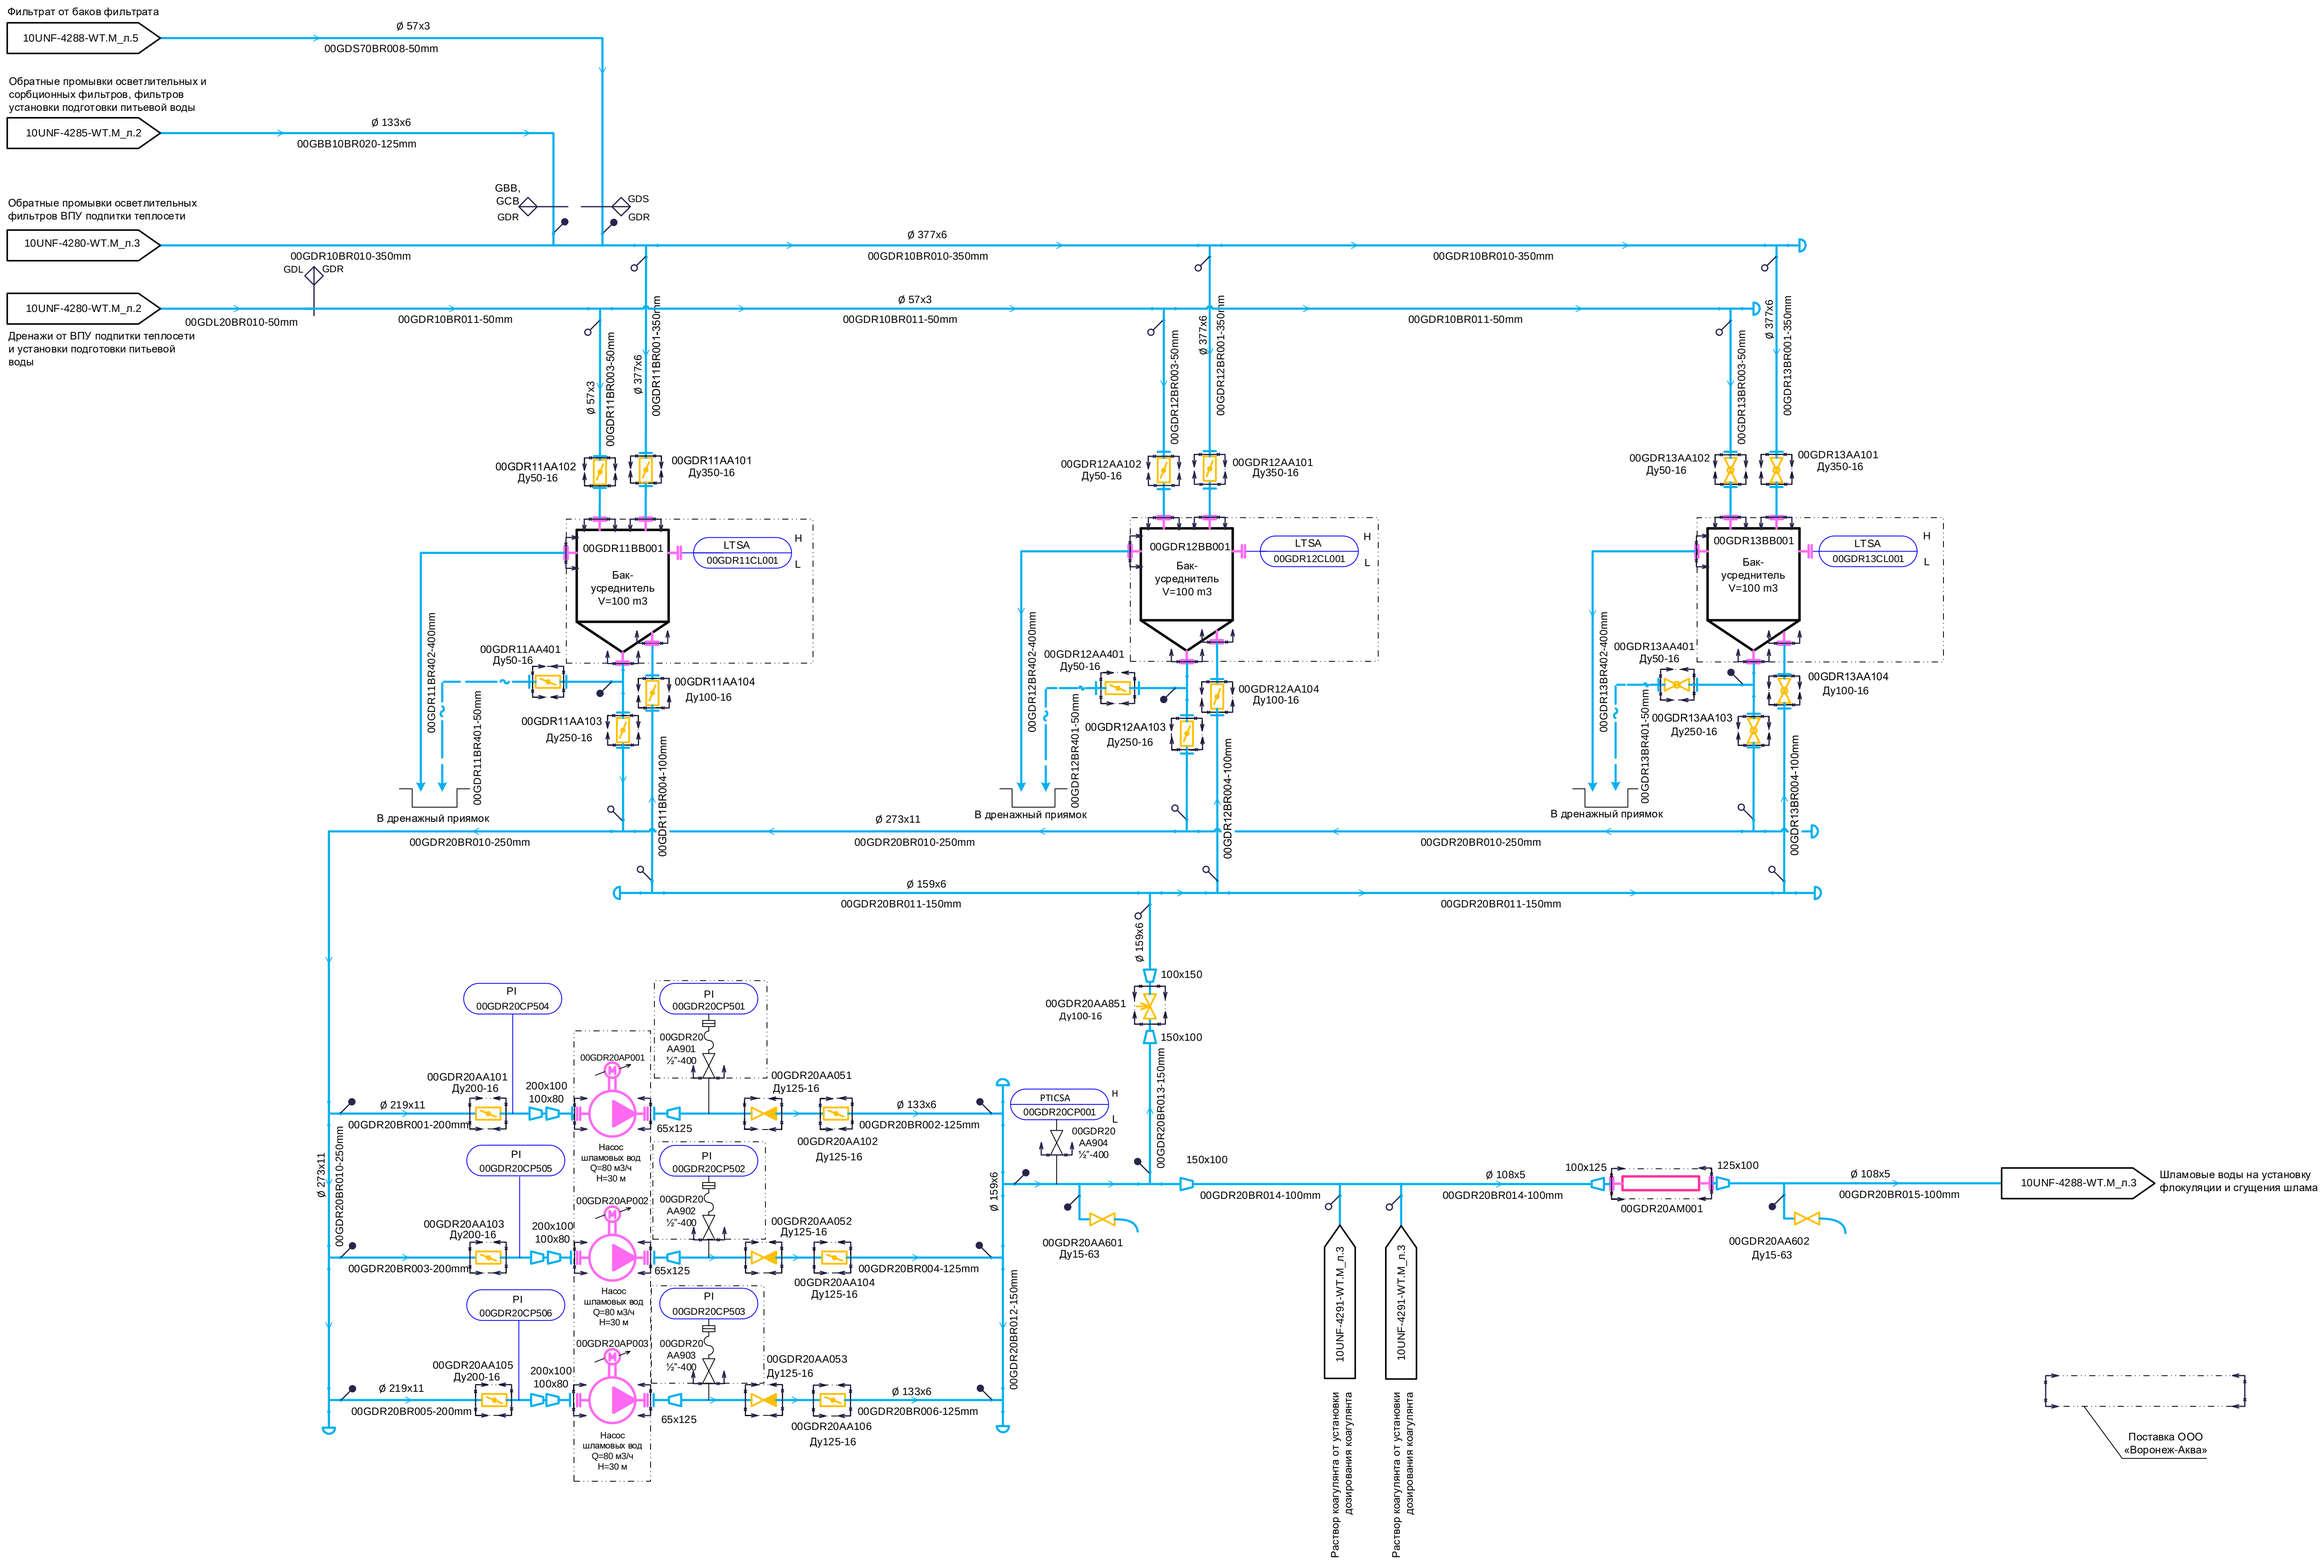

1	-	Зам.	983-15		12.15	68N1-10UNF-4288-WT.M
Изм.	Кол.уч	Лист	№ док.	Подп.	Дата	Строительство Якутской ГРЭС-2 (первая очередь)
Н. контр.		Тараненко				Установка обезвоживания шлама. PI-диаграммы
						Стадия: Р; Лист: 2; Листов:
Проверил		Рудь				PI-диаграмма баков-усреднителей. Система GDR
Разработал		Растопчина				АКЦИОНЕРНОЕ ОБЩЕСТВО ИНСТИТУТ ТЕПЛОЭЛЕКТРОПРОЕКТ г. МОСКВА

Согласовано: ОАСУ Гушинская

Взам. инв. №

Подпись и дата

Инв. № подл.

Формат А1