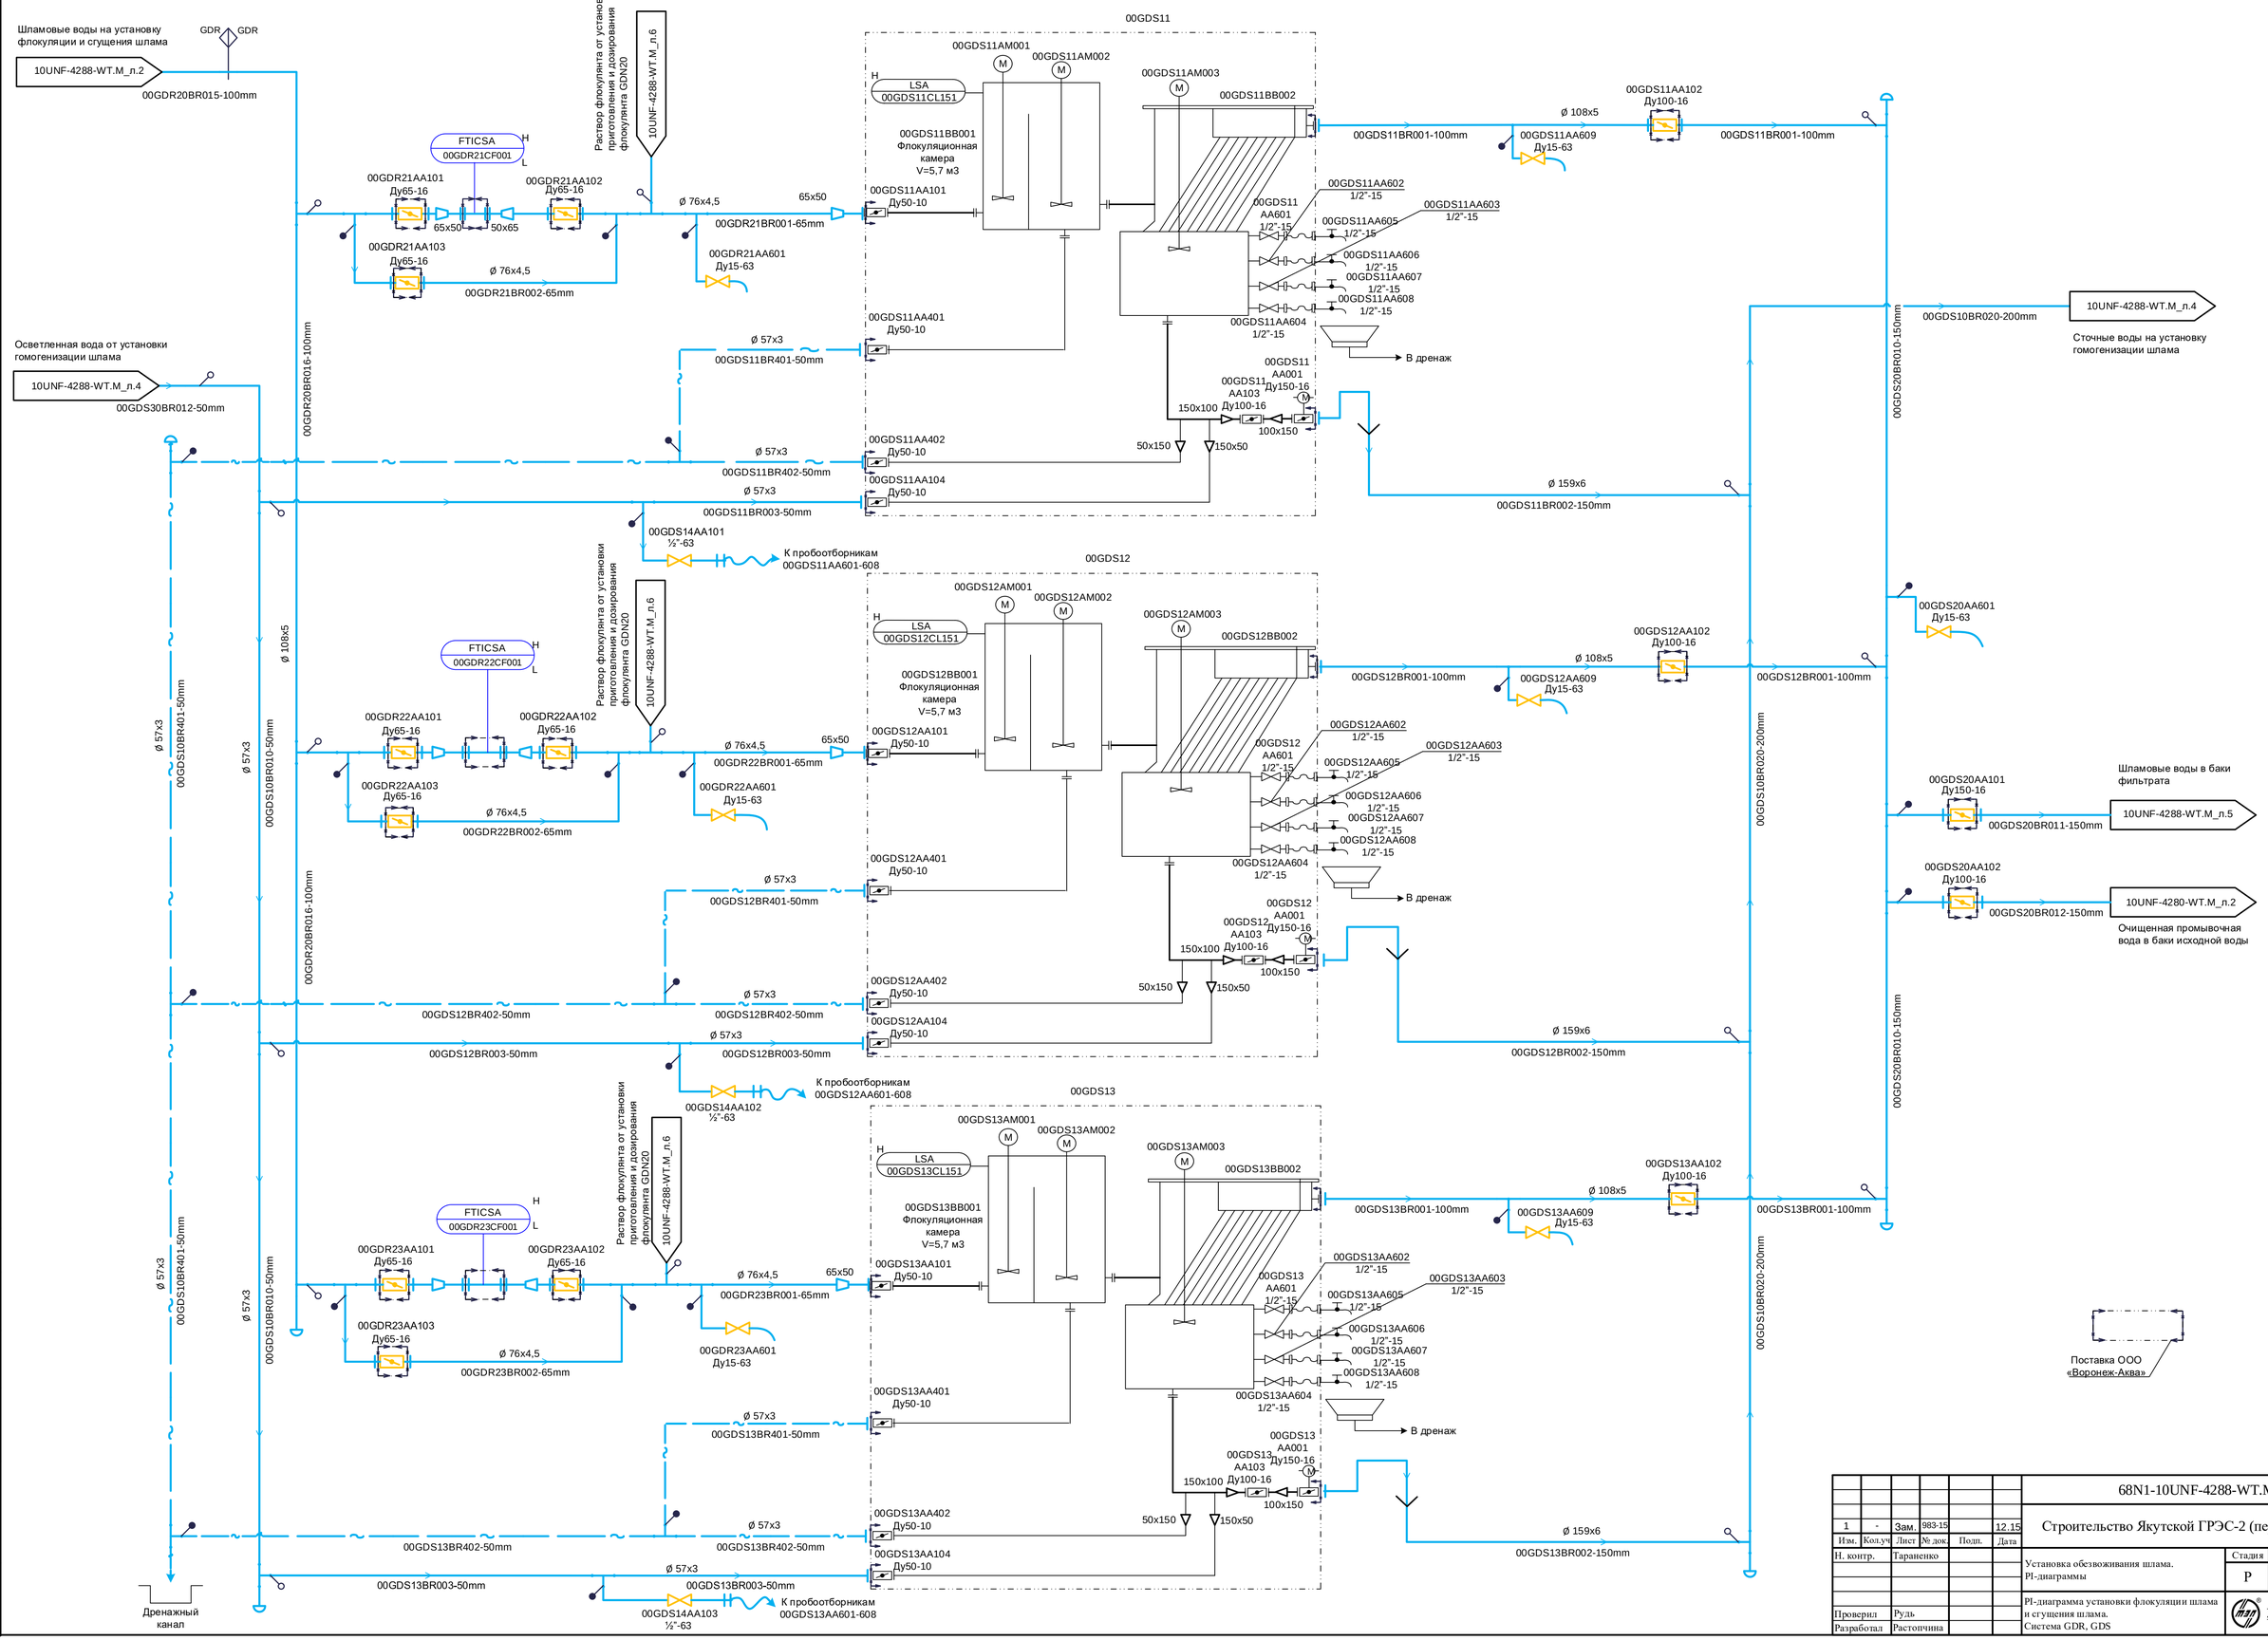

						68N1-10UNF-4288-WT.M
1	-	Зам.	983-15		12.15	Строительство Якутской ГРЭС-2 (первая очередь)
Изм.	Кол.уч	Лист	№ док.	Подп.	Дата	
Н. контр.		Тараненко				Установка обезвоживания шлама. PI-диаграммы
Проверил		Рудь				PI-диаграмма установки флокуляции шлама и сгущения шлама. Система GDR, GDS
Разработал		Растопчина				

Стадия	Лист	Листов
Р	3	

АКЦИОНЕРНОЕ ОБЩЕСТВО ИНСТИТУТ ТЕПЛОЭЛЕКТРОПРОЕКТ г. МОСКВА

Согласовано: ОАСУ Гушинская

Взам. инв. № | Подпись и дата | Инв. № подл.

Формат А1