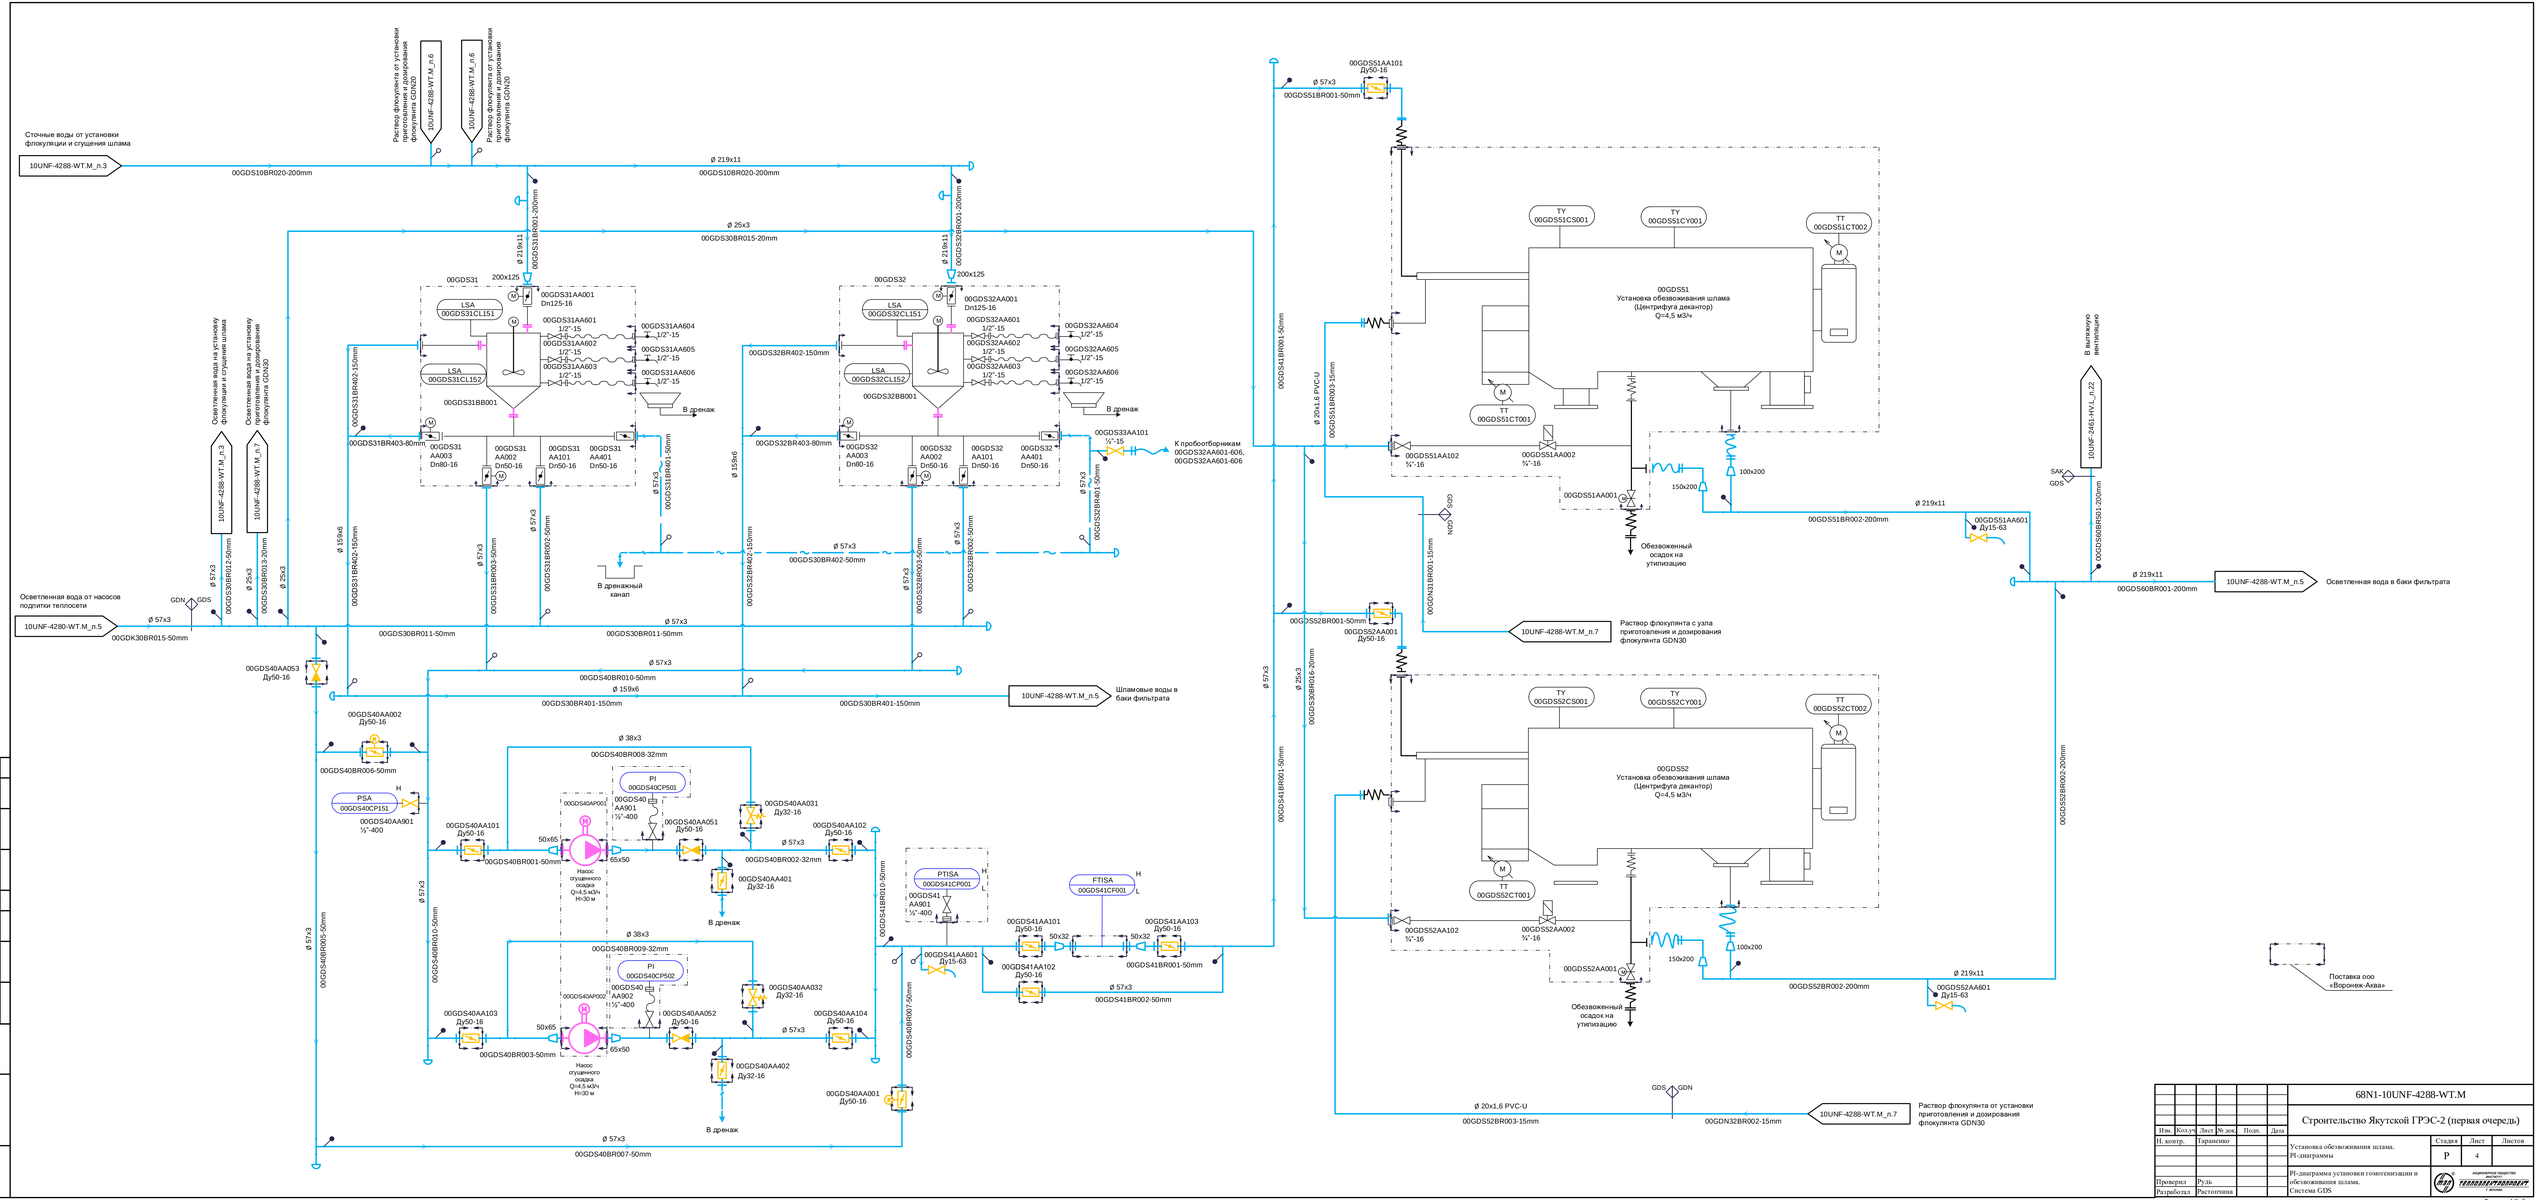

							68N1-10UNF-4288-WT.M
							Строительство Якутской ГРЭС-2 (первая очередь)
Изм.	Кол.уч.	Лист	№ док.	Подп.	Дата		
Н. контр.	Тараненко					Установка обезвоживания шлама. PI-диаграммы	Стадия: Р; Лист: 4; Листов:
Проверил	Рузь					PI-диаграмма установки гомогенизации и обезвоживания шлама. Система GDS	НЕФТЕГАЗСТРОЙ ИНЖИНИРИНГ
Разработал	Расточтина						

Согласовано

Взам. инв. №

Подпись и дата

Инв. № подл.

Формат А2х3