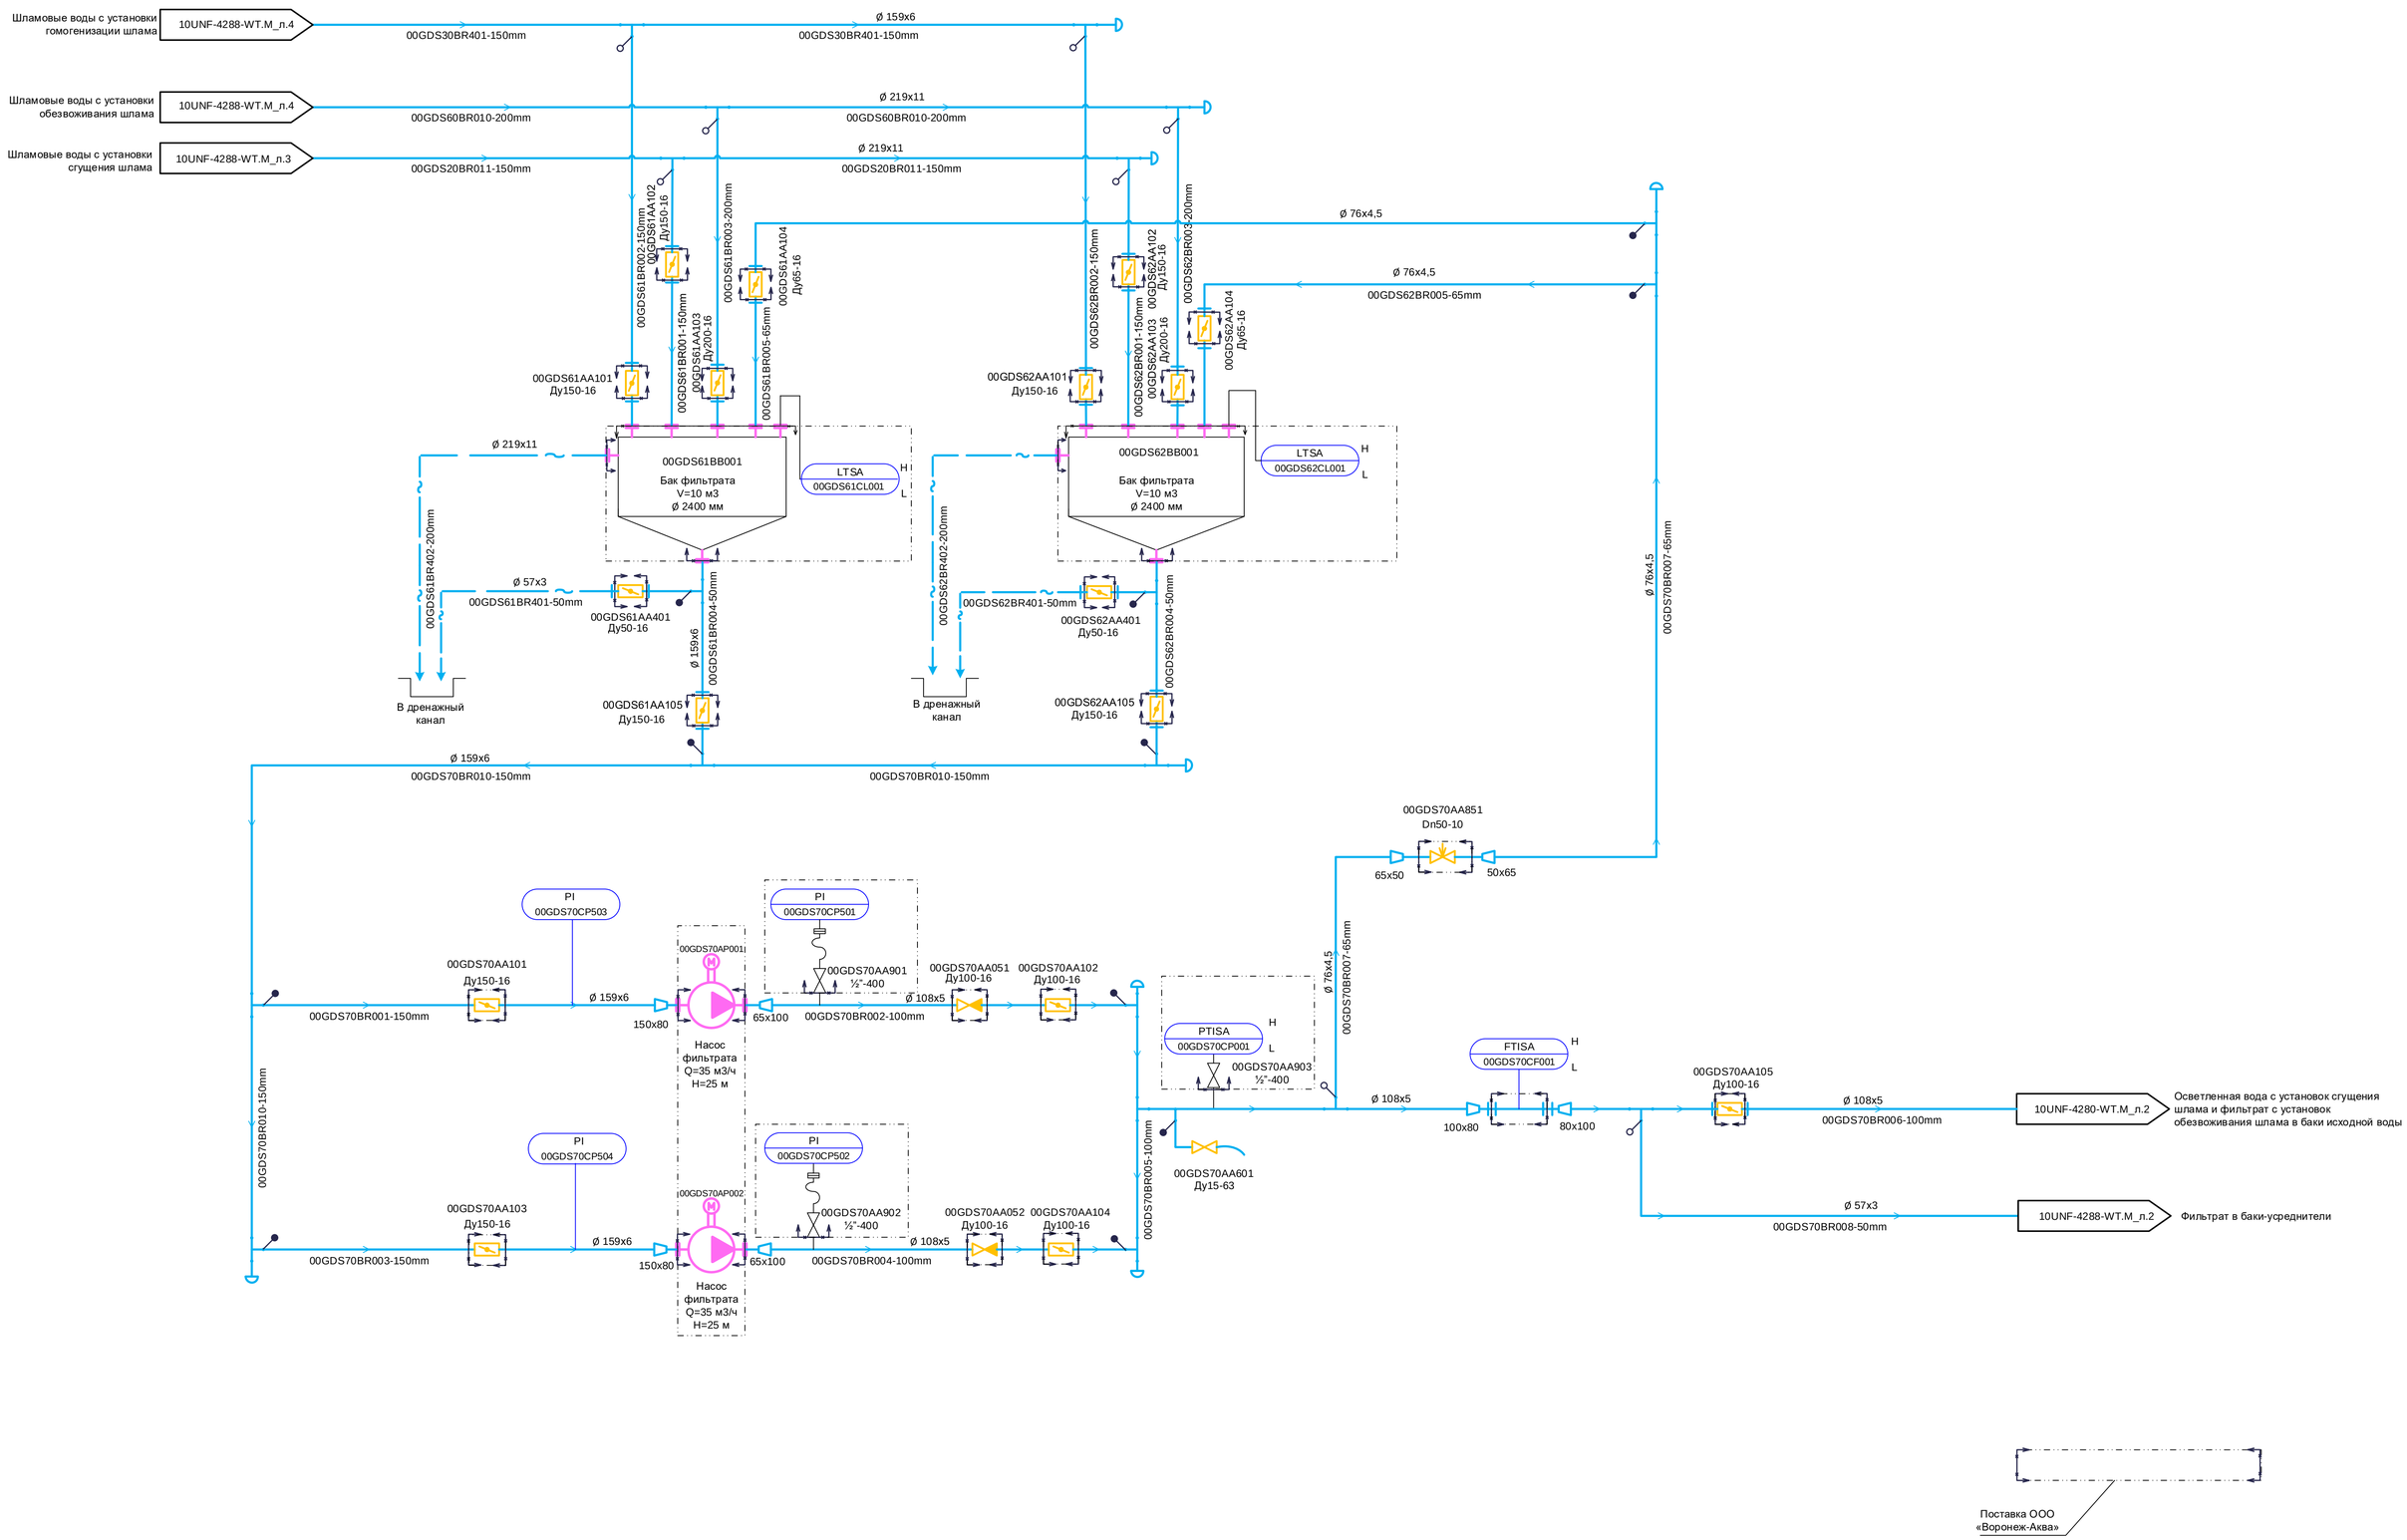

Изм.	Кол.уч	Лист	№ док.	Подп.	Дата
1	-	Зам.	983-15		12.15

68N1-10UNF-4288-WT.M

Строительство Якутской ГРЭС-2 (первая очередь)

Н. контр.	Тараненко	
Проверил	Рудь	
Разработал	Растопчина	

Установка обезвоживания шлама.
PI-диаграммы

PI-диаграмма баков фильтрата. Система GDS

Стадия	Лист	Листов
Р	5	

АКЦИОНЕРНОЕ ОБЩЕСТВО ИНСТИТУТ ТЕПЛОЭЛЕКТРОПРОЕКТ г. МОСКВА

Согласовано

Взам. инв. №

Подпись и дата

Инв. № подл.

Формат А1