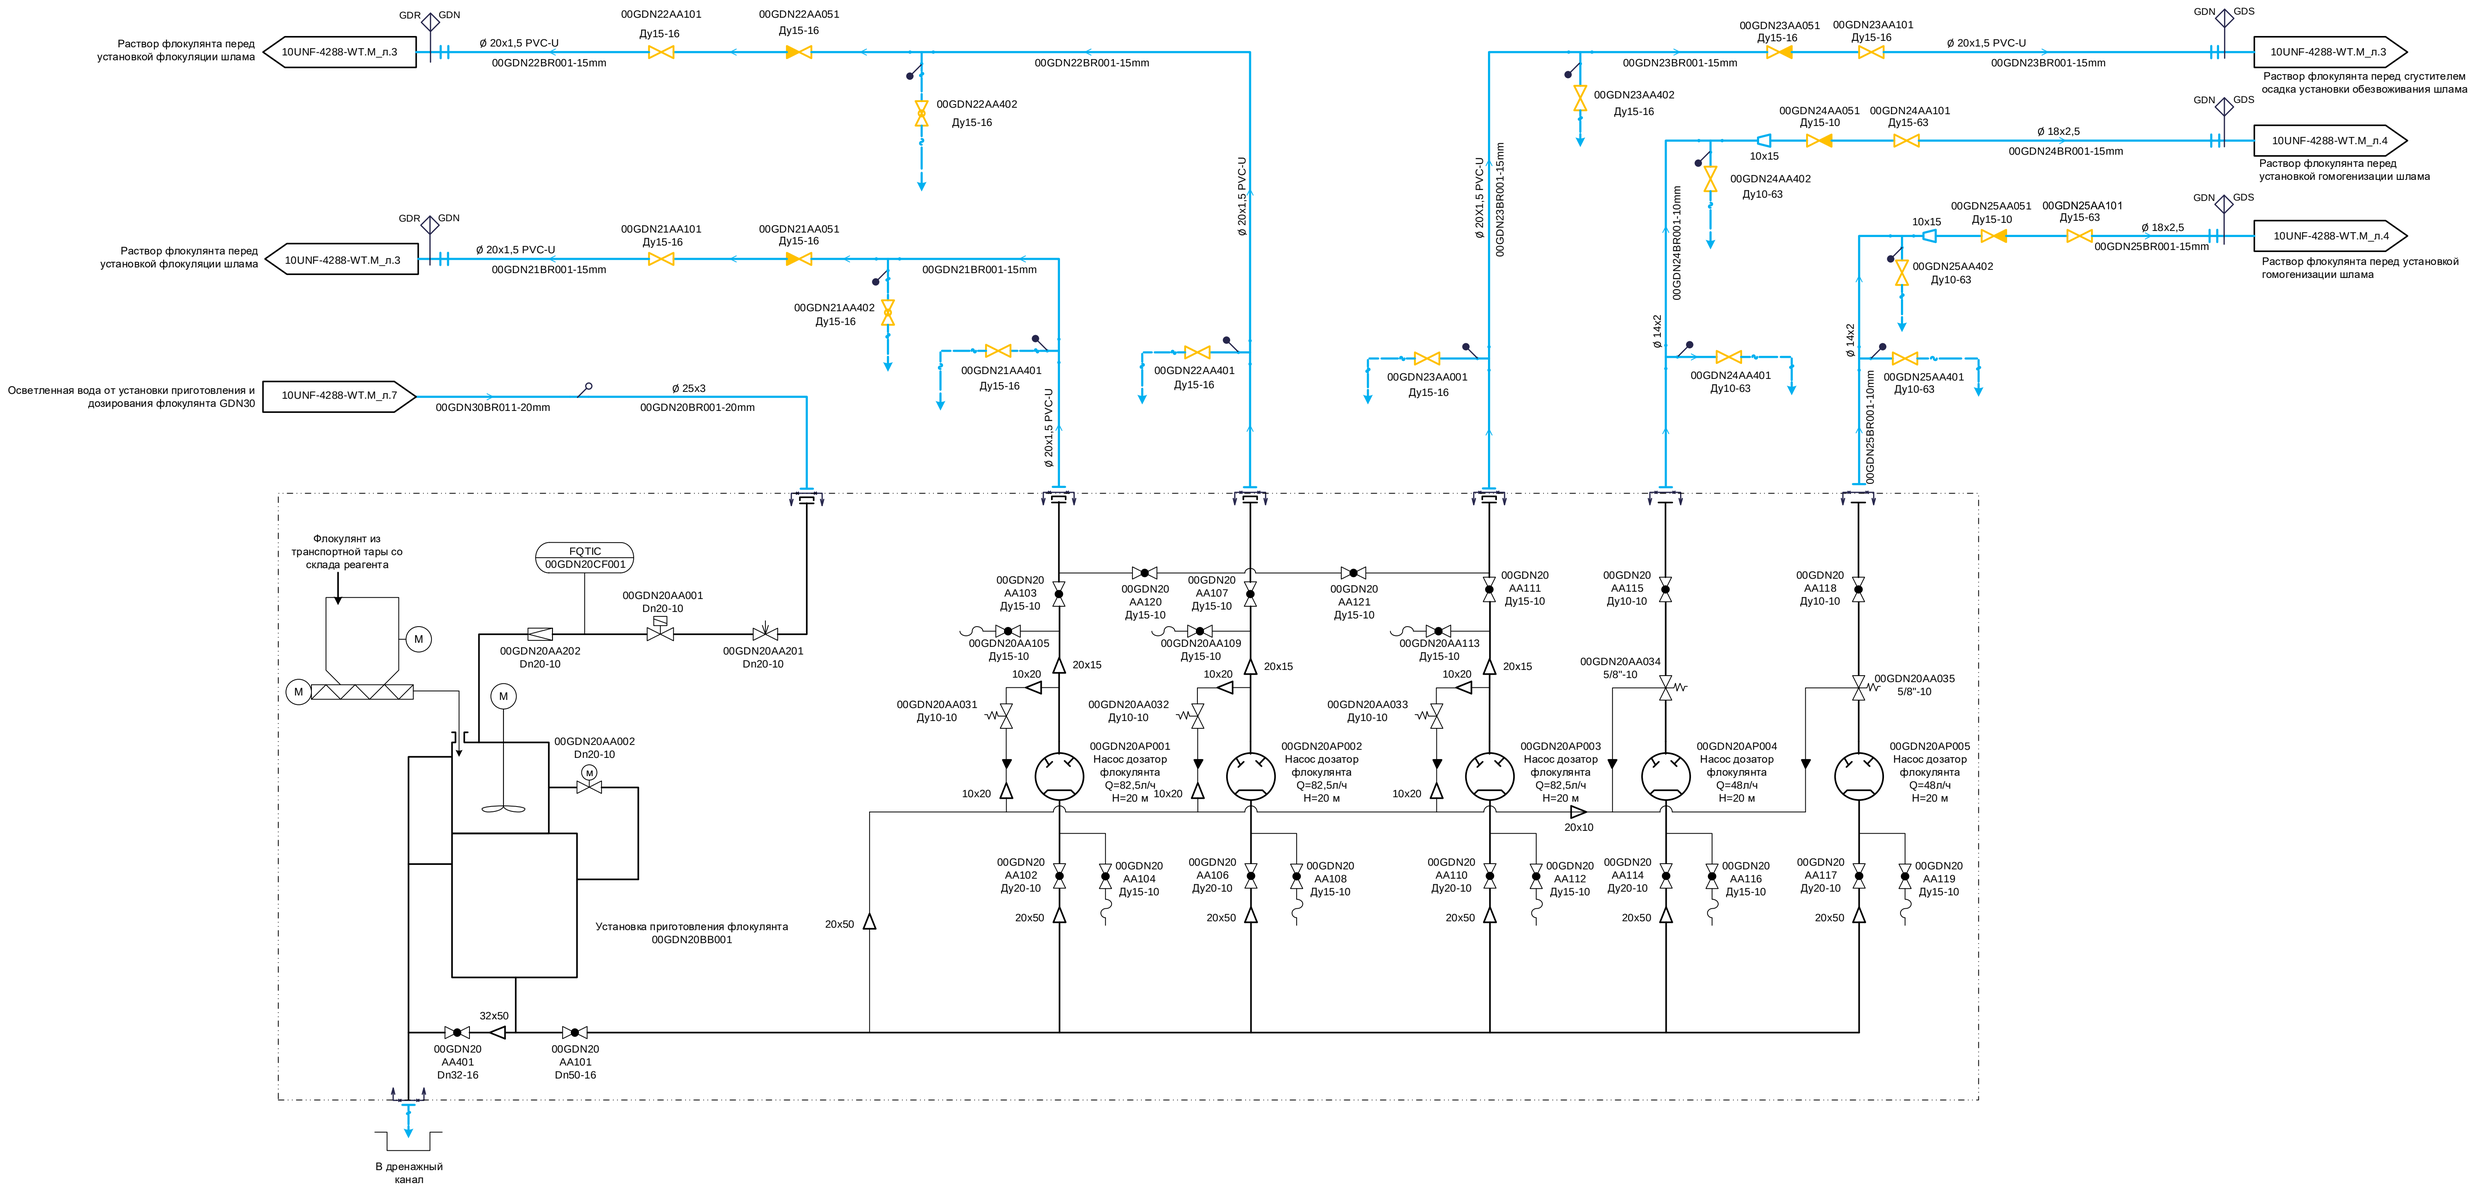

						68N1-10UNF-4288-WT.M			
						Строительство Якутской ГРЭС-2 (первая очередь)			
Изм.	Кол.уч	Лист	№ док.	Подп.	Дата				
Н. контр.		Тараненко				Установка обезвоживания шлама. PI-диаграммы	Стадия	Лист	Листов
							Р	6	
Проверил		Рудь				PI-диаграмма установки приготовления и дозирования флокулянта. Система GDN 20	АКЦИОНЕРНОЕ ОБЩЕСТВО ТЕПЛОЭЛЕКТРОПРОЕКТ г. МОСКВА		
Разработал		Растопчина							

Согласовано

Взам. инв. №

Подпись и дата

Инв. № подл.

Формат А1