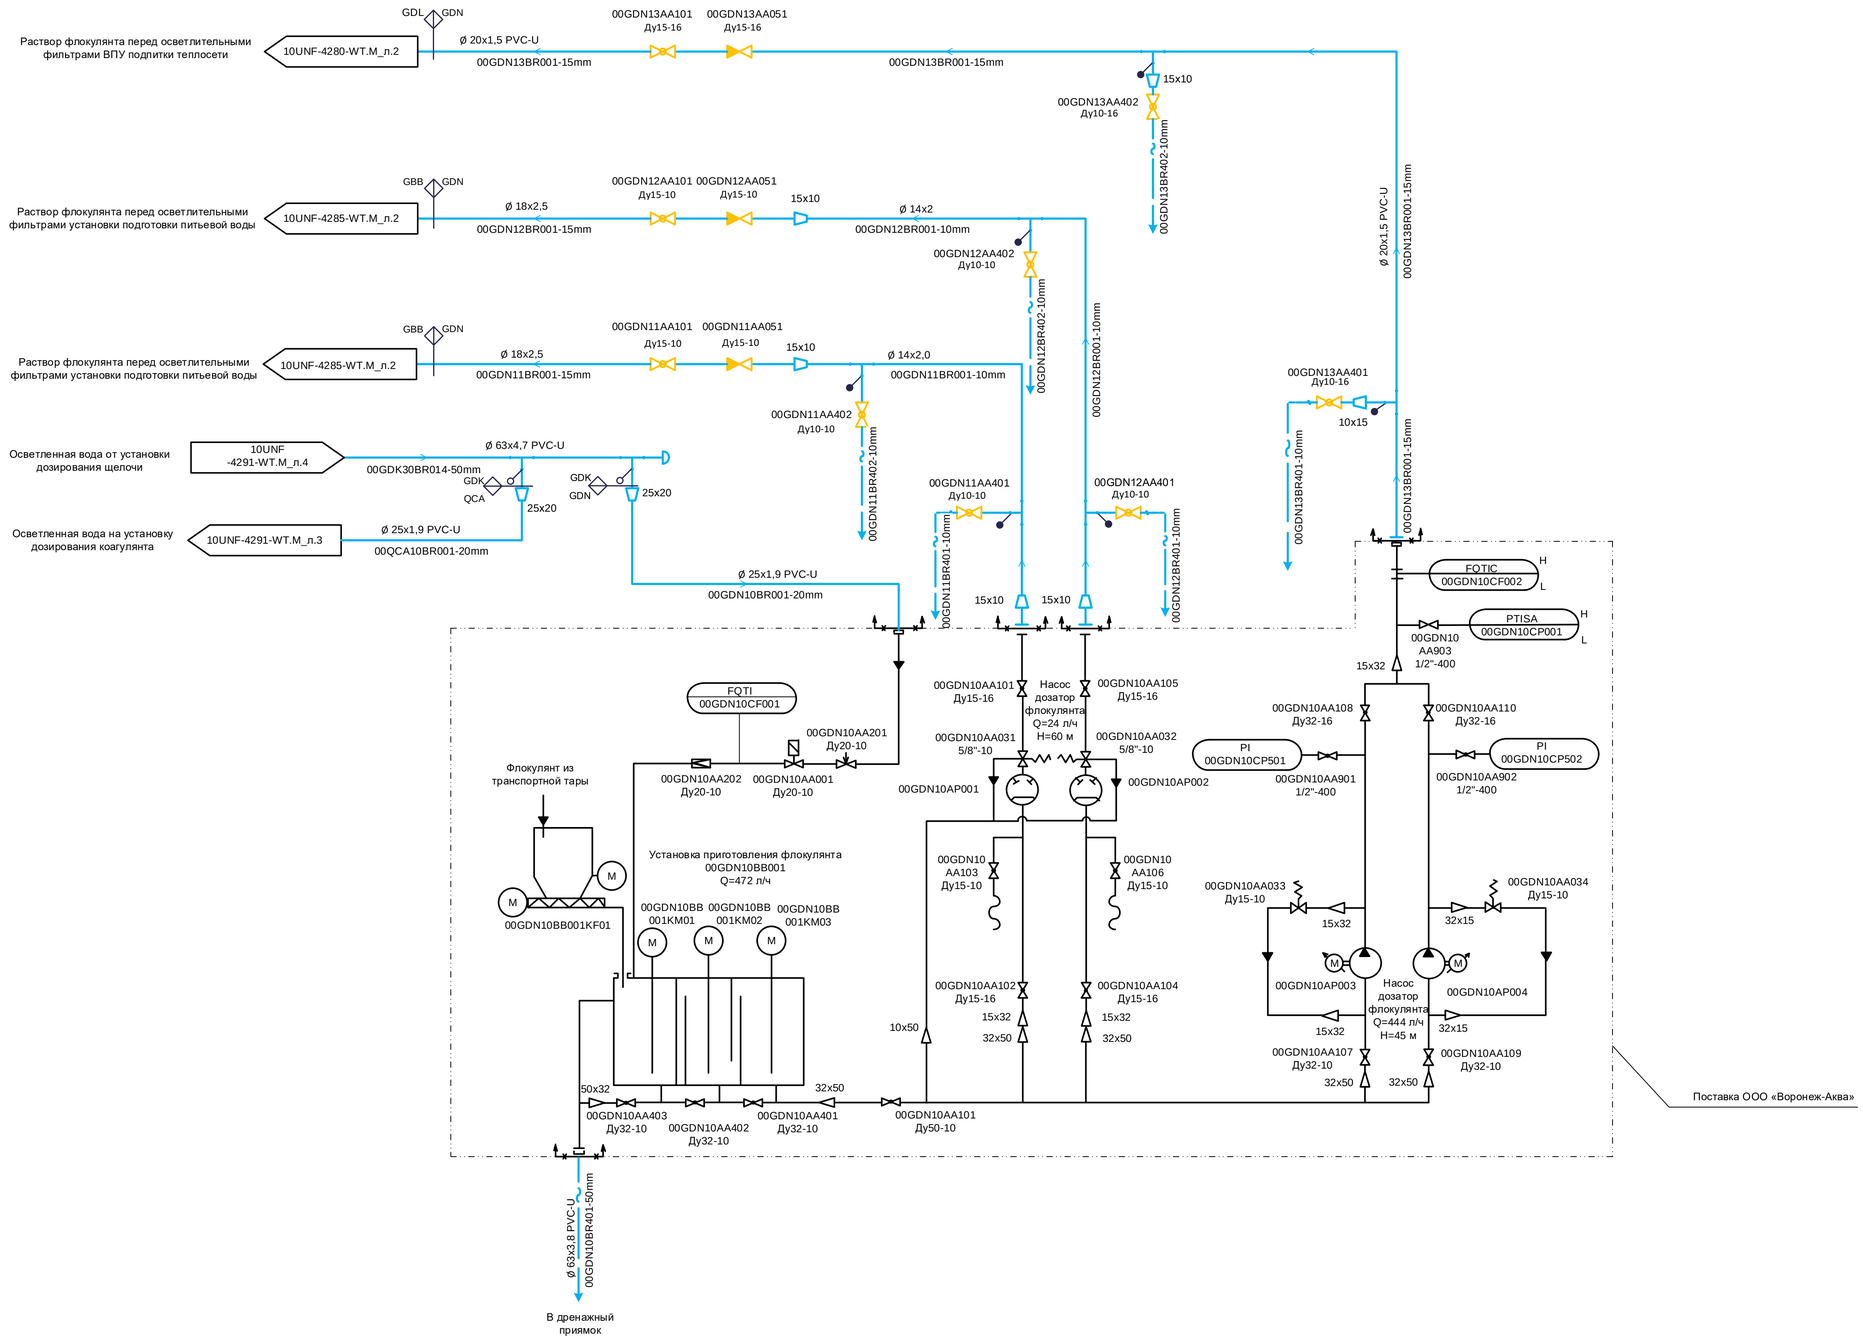

Изм.	Кол.уч	Лист	№ док.	Подп.	Дата	68N1-10UNF-4291-WT.M
						Строительство Якутской ГРЭС-2 (первая очередь)
Н. контр.		Тараненко				Объединенный корпус. Склад химических реагентов. PI-диаграммы
Проверил		Рудь				PI-диаграмма установки приготовления и дозирования флокулянта. Система GDN
Разработал		Растопчина				

Стадия	Лист	Листов
Р	2	

АКЦИОНЕРНОЕ ОБЩЕСТВО ИНСТИТУТ ТЕПЛОЭЛЕКТРОПРОЕКТ Г. МОСКВА

Согласовано

Взам. инв. №

Подпись и дата

Инв. № подл.

Формат А1