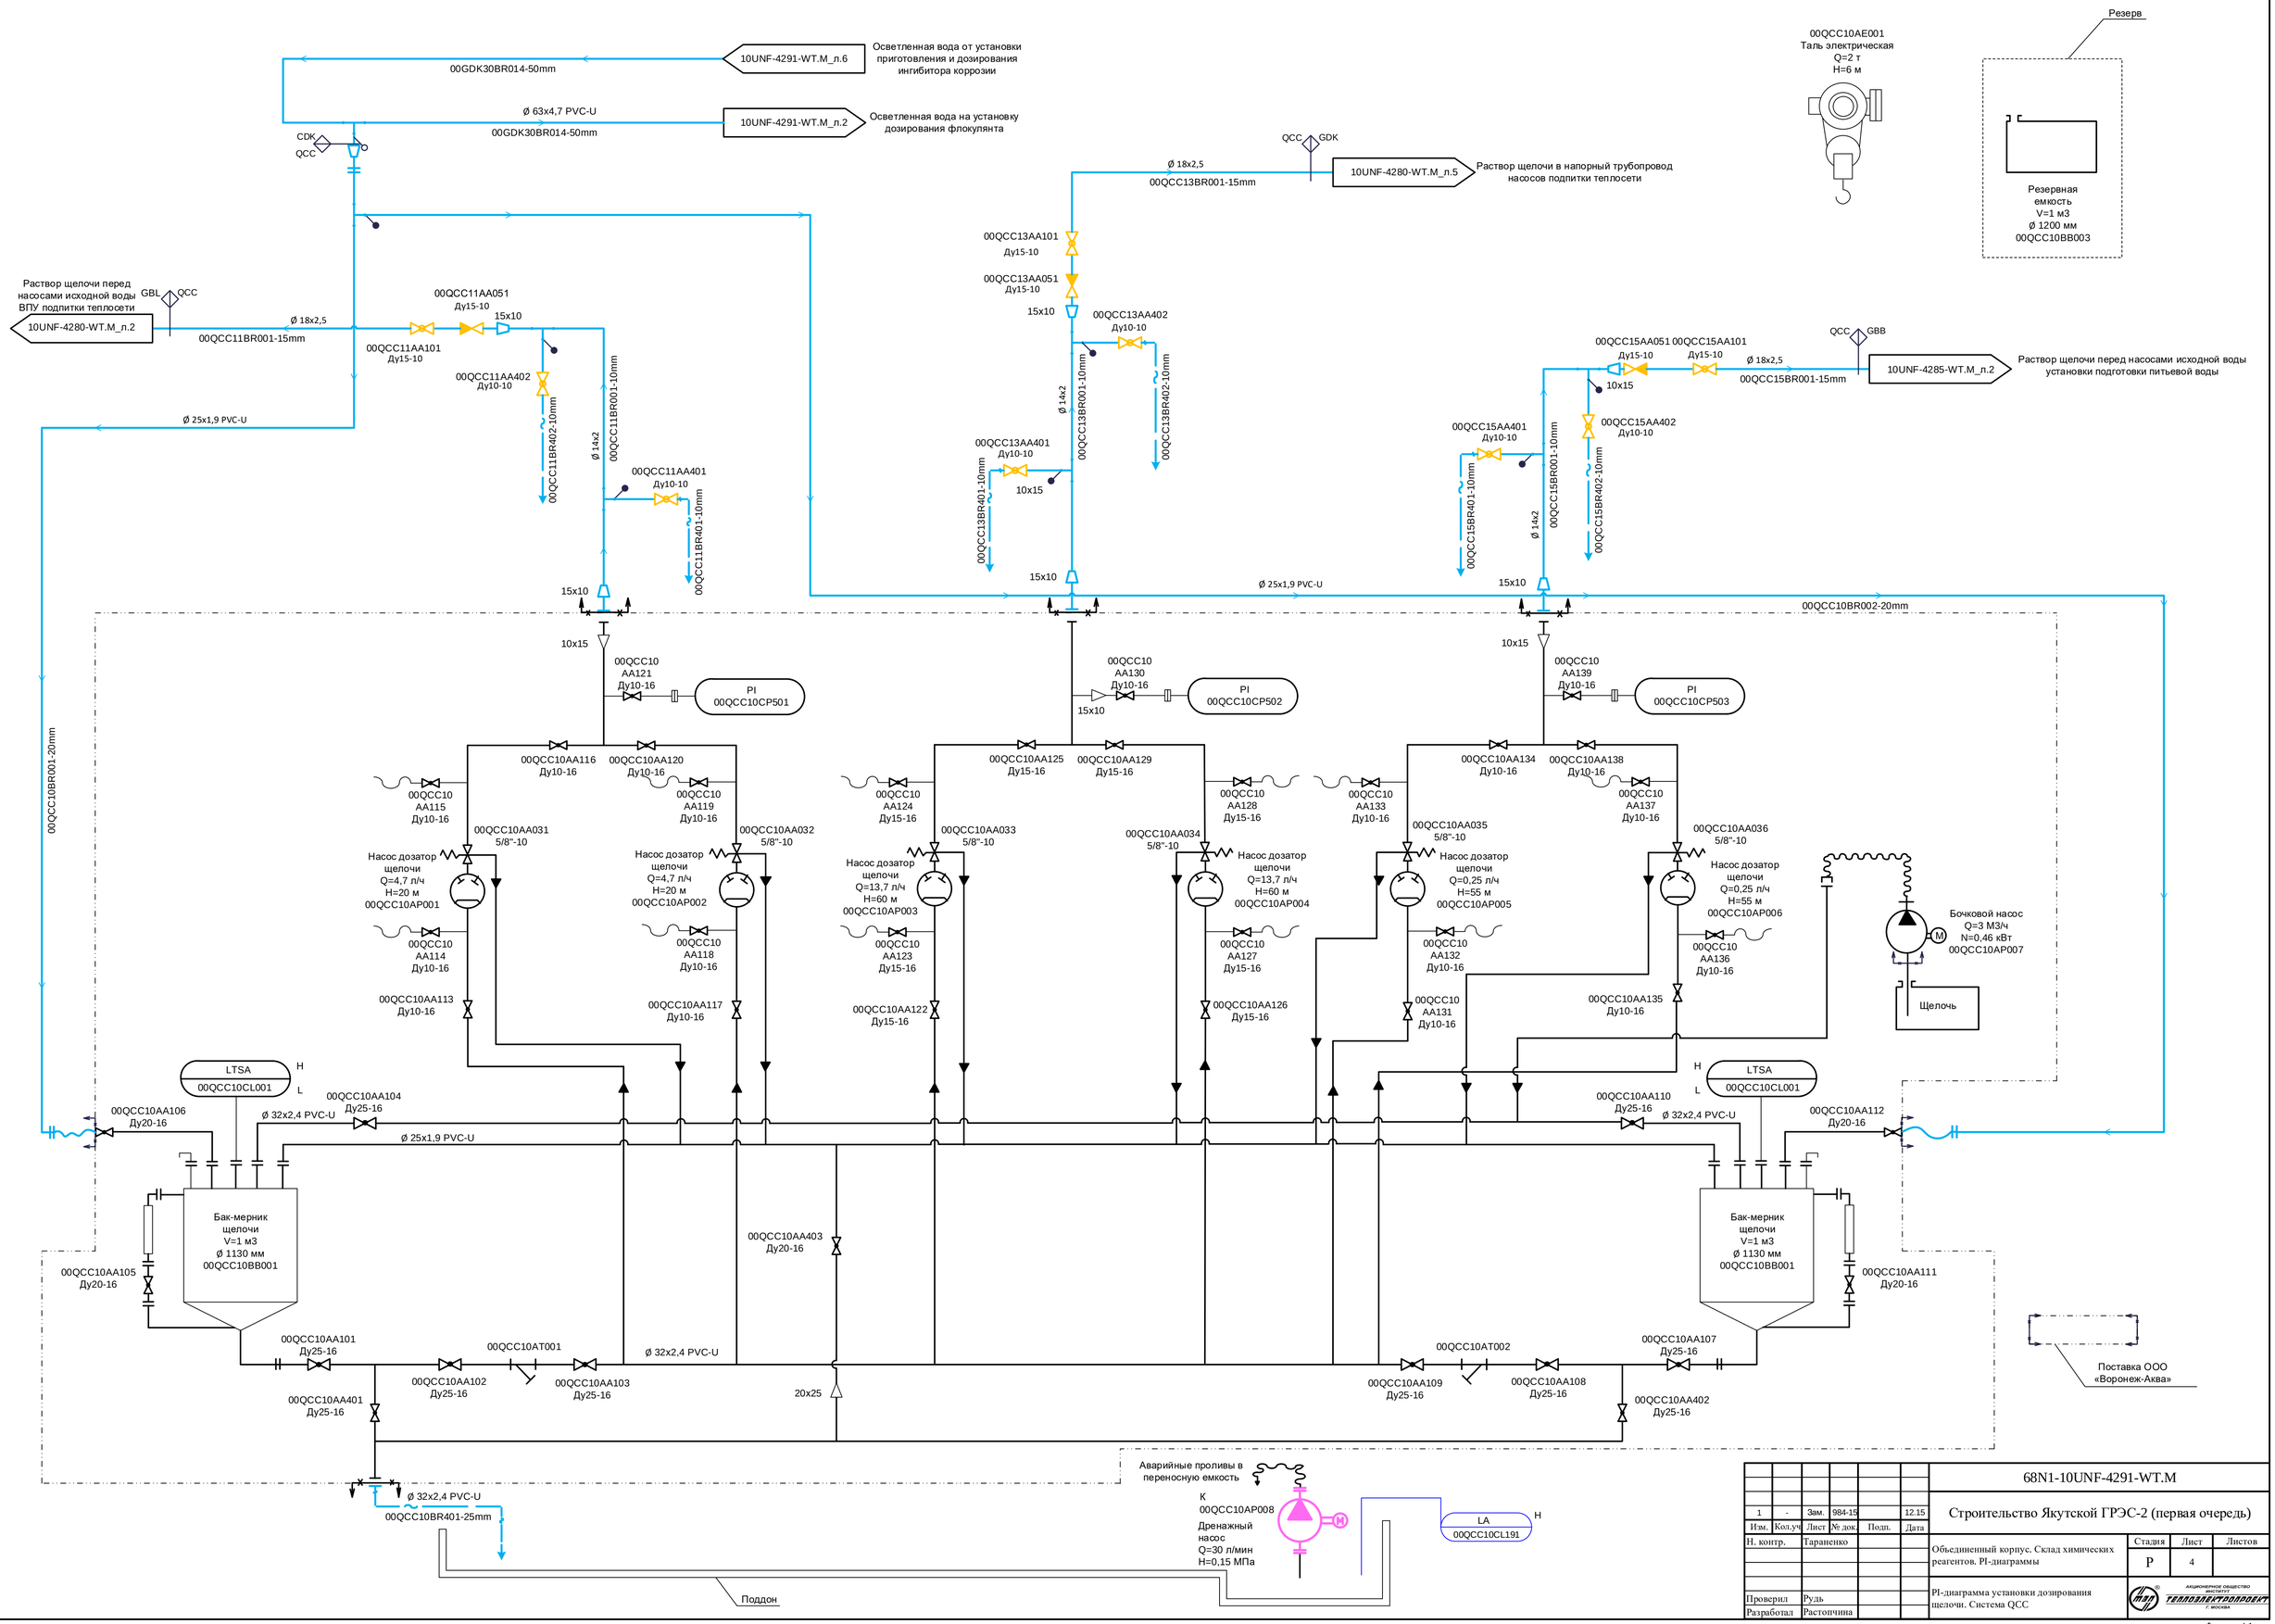

1	-	Зам.	984-15		12.15	
Изм.	Кол.уч	Лист	№ док.	Подп.	Дата	
Н. контр.		Тараненко				
Проверил		Рудь				
Разработал		Растопчина				

68N1-10UNF-4291-WT.M

Строительство Якутской ГРЭС-2 (первая очередь)

Объединенный корпус. Склад химических реагентов. PI-диаграммы

Стадия	Лист	Листов
Р	4	

PI-диаграмма установки дозирования щелочи. Система QCC

АКЦИОНЕРНОЕ ОБЩЕСТВО ИНСТИТУТ ТЕПЛОЭЛЕКТРОПРОЕКТ г. МОСКВА

Согласовано
ОАСУ Туашиская

Взам. инв. №

Подпись и дата

Инв. № подл.

Формат А1