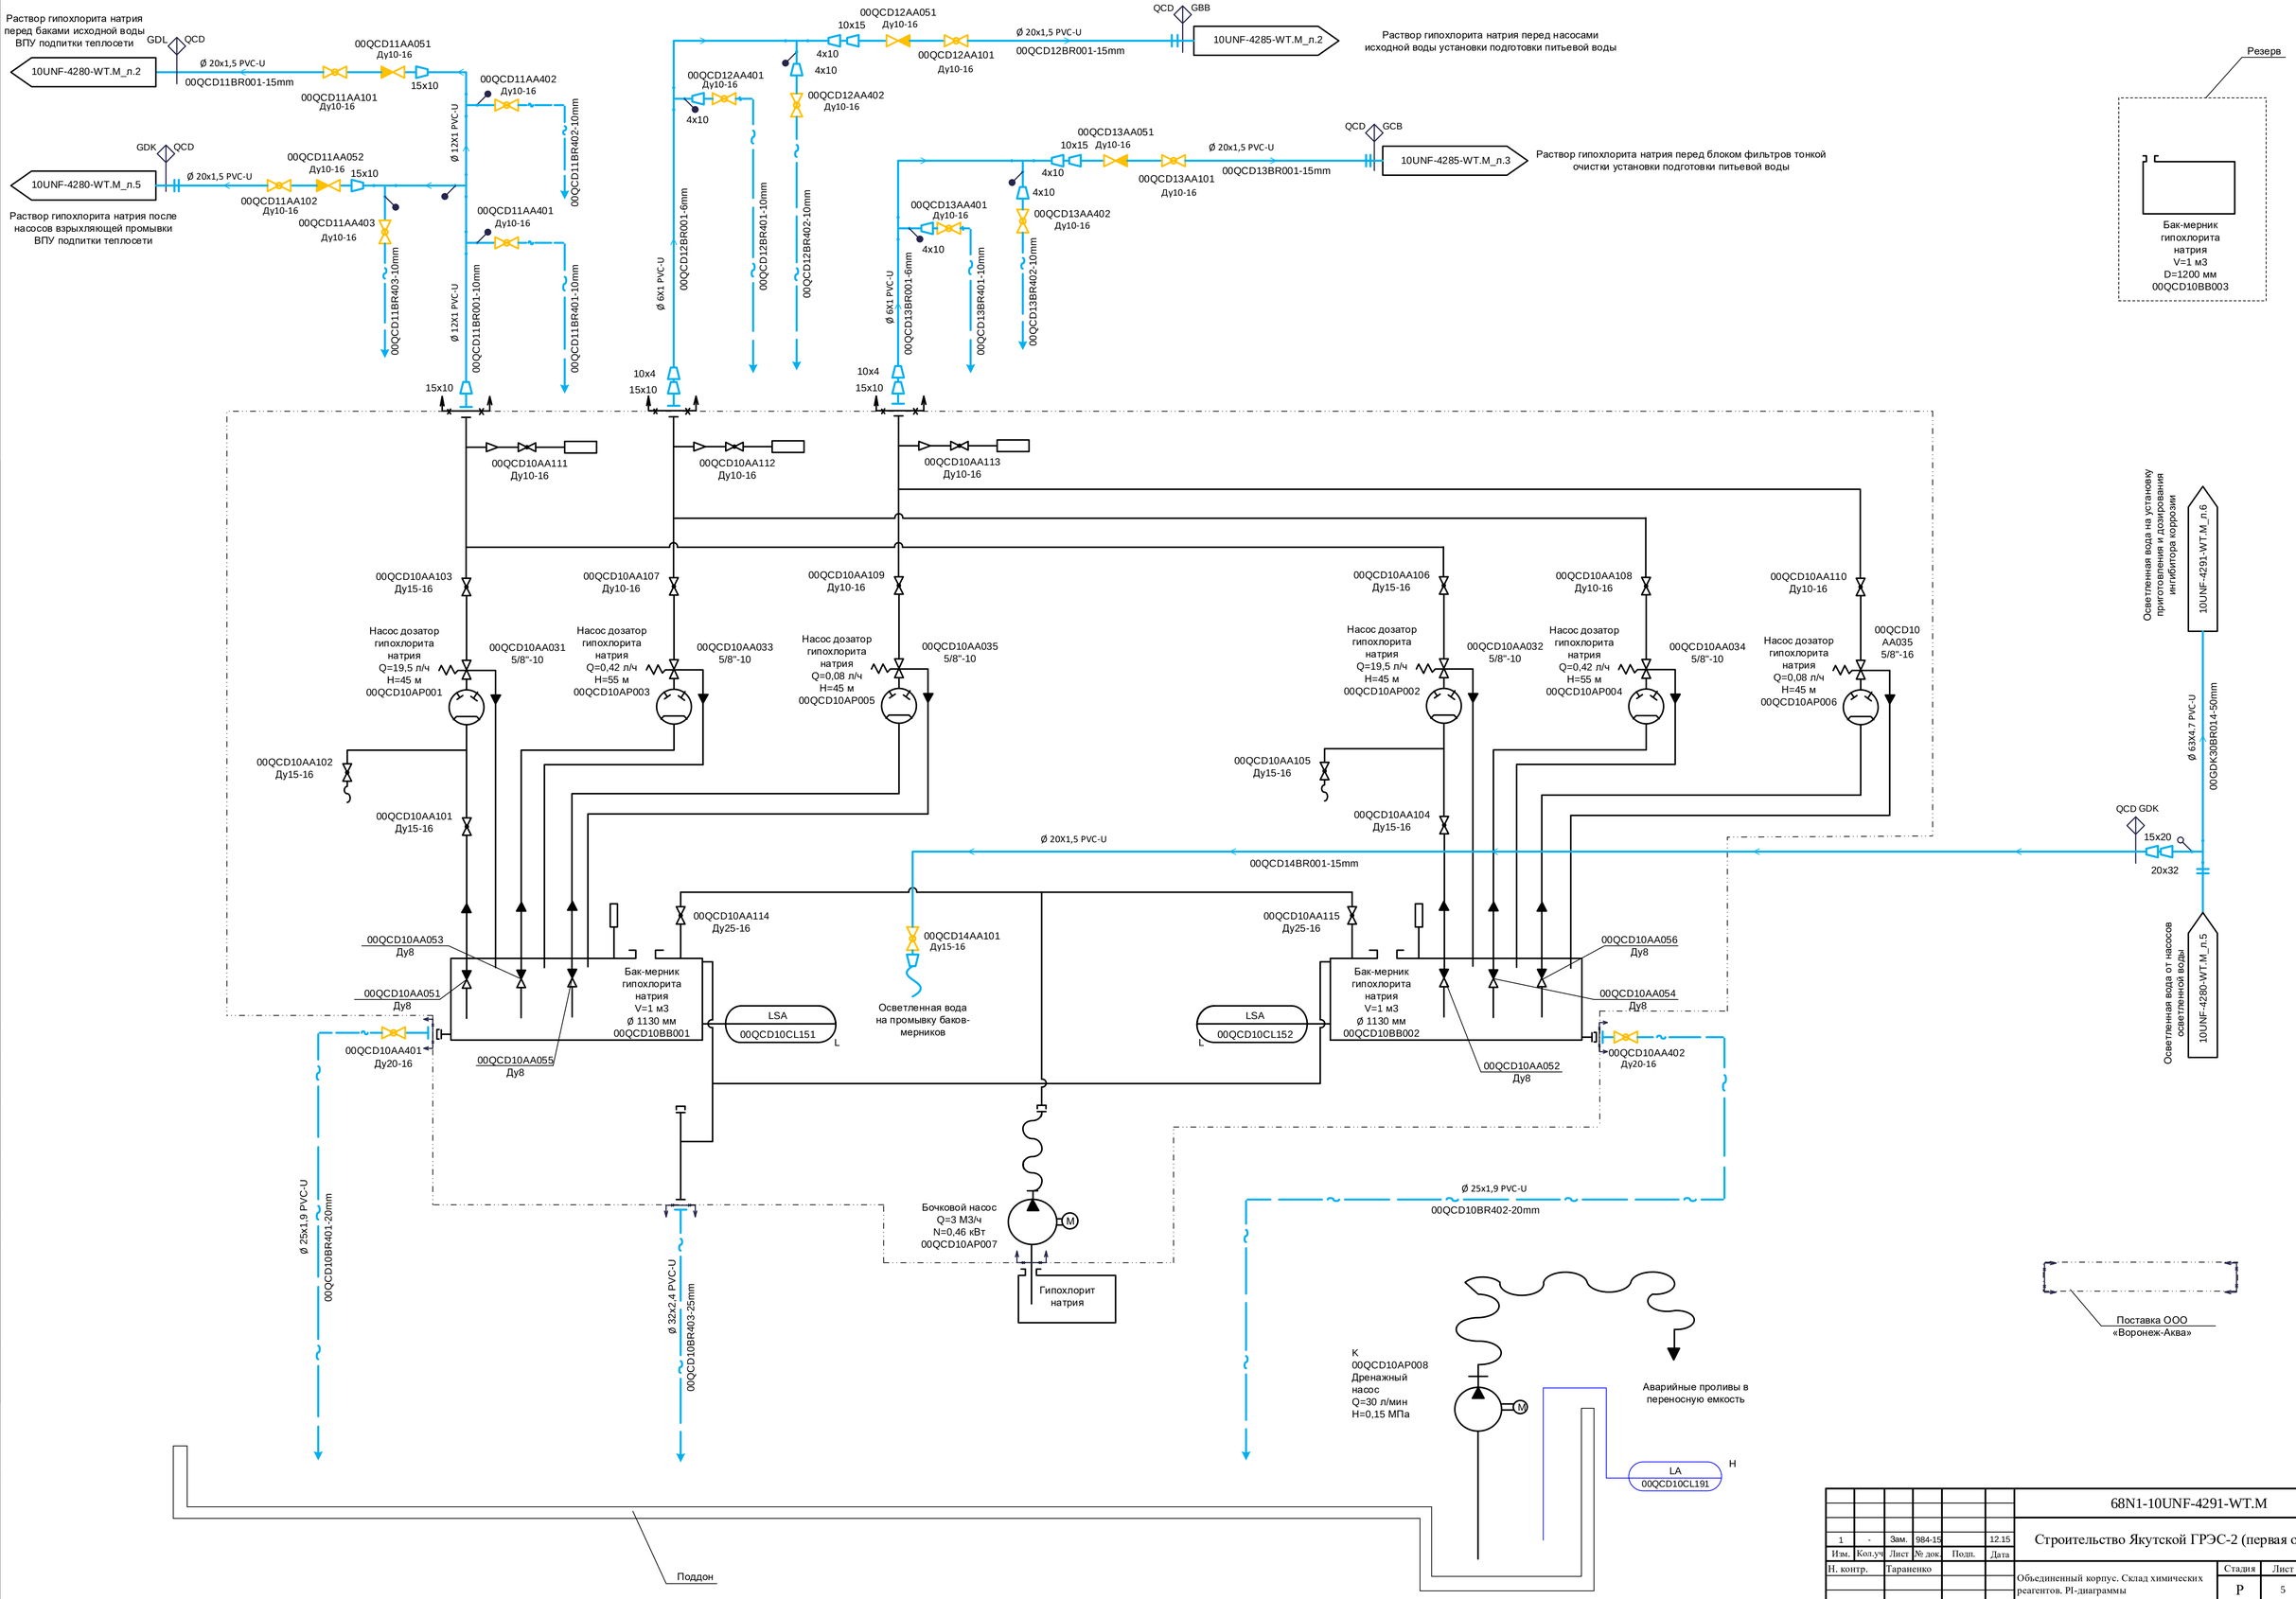

						68N1-10UNF-4291-WT.M
1	-	Зам.	984-15		12.15	Строительство Якутской ГРЭС-2 (первая очередь)
Изм.	Кол.уч	Лист	№ док.	Подп.	Дата	
Н. контр.		Тараненко				Объединенный корпус. Склад химических реагентов. PI-диаграммы
						Стадия: Р; Лист: 5; Листов:
Проверил		Рудь				PI-диаграмма установки дозирования гипохлорита натрия. Система QCD
Разработал		Растопчина				АКЦИОНЕРНОЕ ОБЩЕСТВО ИНСТИТУТ ТЕПЛОЭЛЕКТРОПРОЕКТ Г. МОСКВА

Согласовано
ОАСУ Тудинская

Взам. инв. №
Подпись и дата
Инв. № подл.

Формат А1