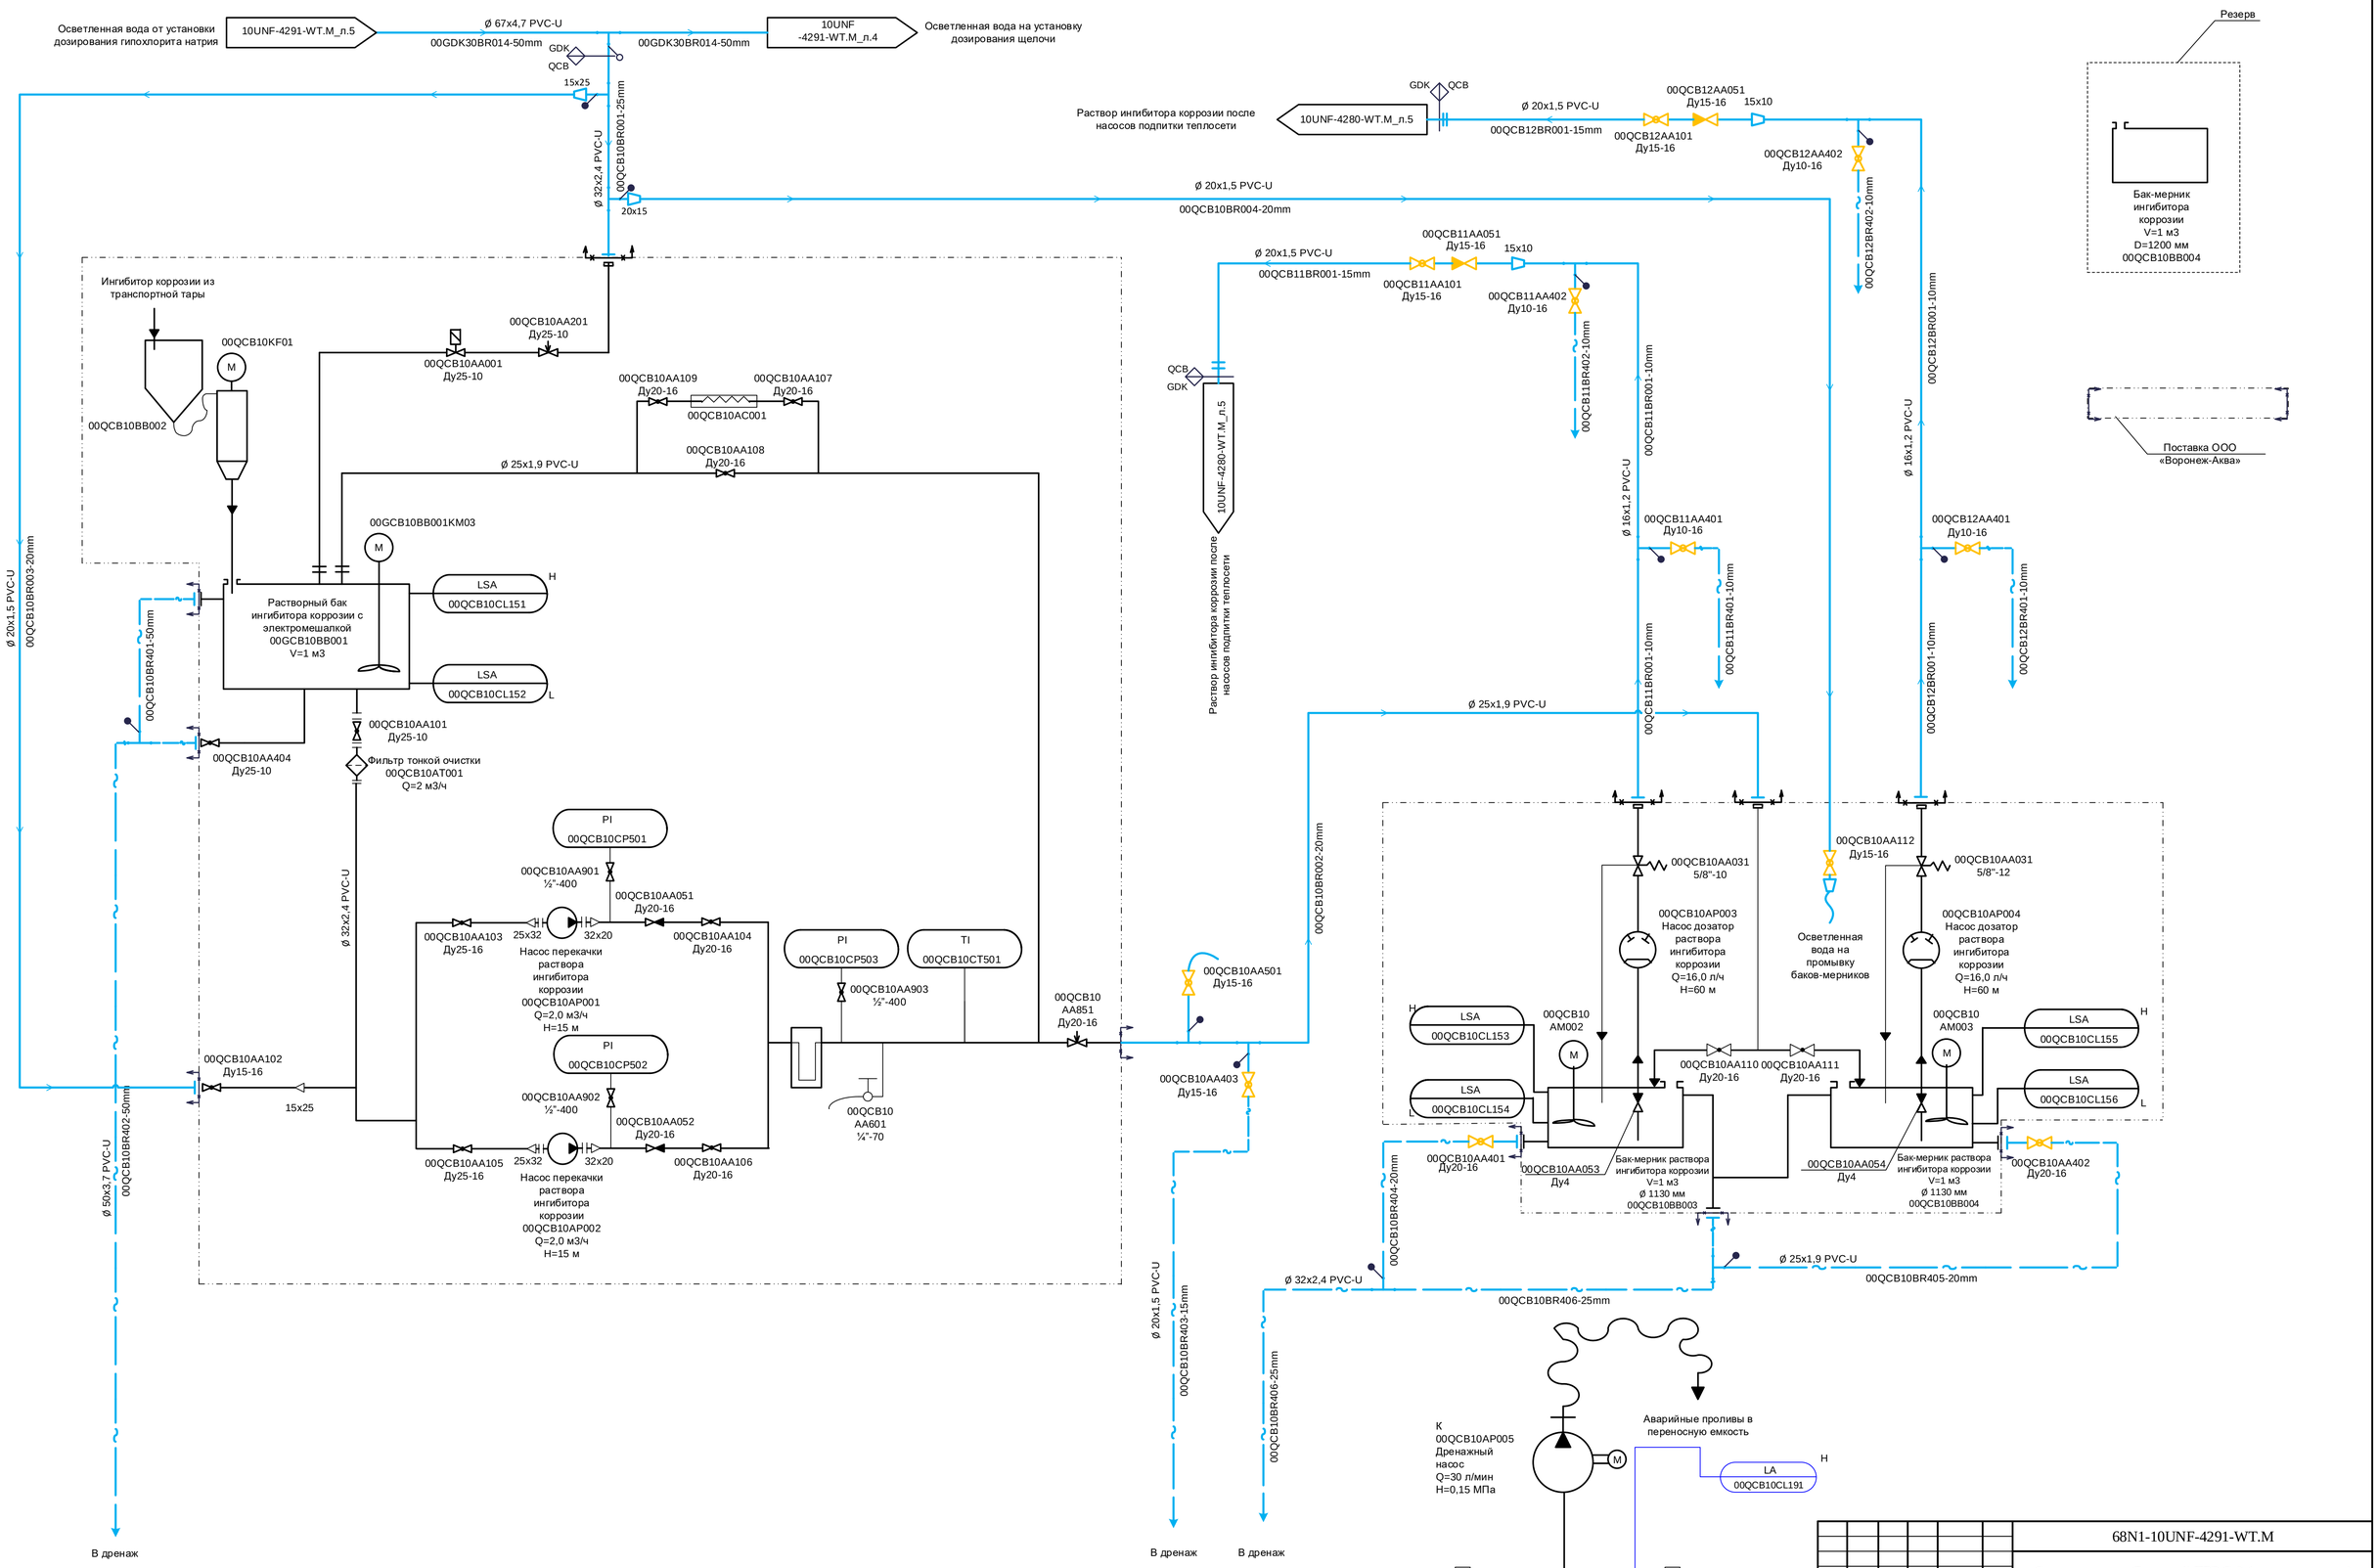

1	-	Зам.	984-15		12.15	68N1-10UNF-4291-WT.M	
Изм.	Кол.уч	Лист	№ док.	Подп.	Дата	Строительство Якутской ГРЭС-2 (первая очередь)	
Н. контр.		Тараненко				Объединенный корпус. Склад химических реагентов. PI-диаграммы	Стадия: Р; Лист: 6; Листов:
Проверил		Руде				PI-диаграмма установка приготовления и дозирования ингибитора коррозии и накипеобразования. Система QCB	АКЦИОНЕРНОЕ ОБЩЕСТВО ИНСТИТУТ ТЕПЛОЭЛЕКТРОПРОЕКТ г. МОСКВА
Разработал		Растопчина					

Согласовано: ОАСУ, Тудинская

Взам. инв. №

Подпись и дата

Инв. № подл.

Формат А1