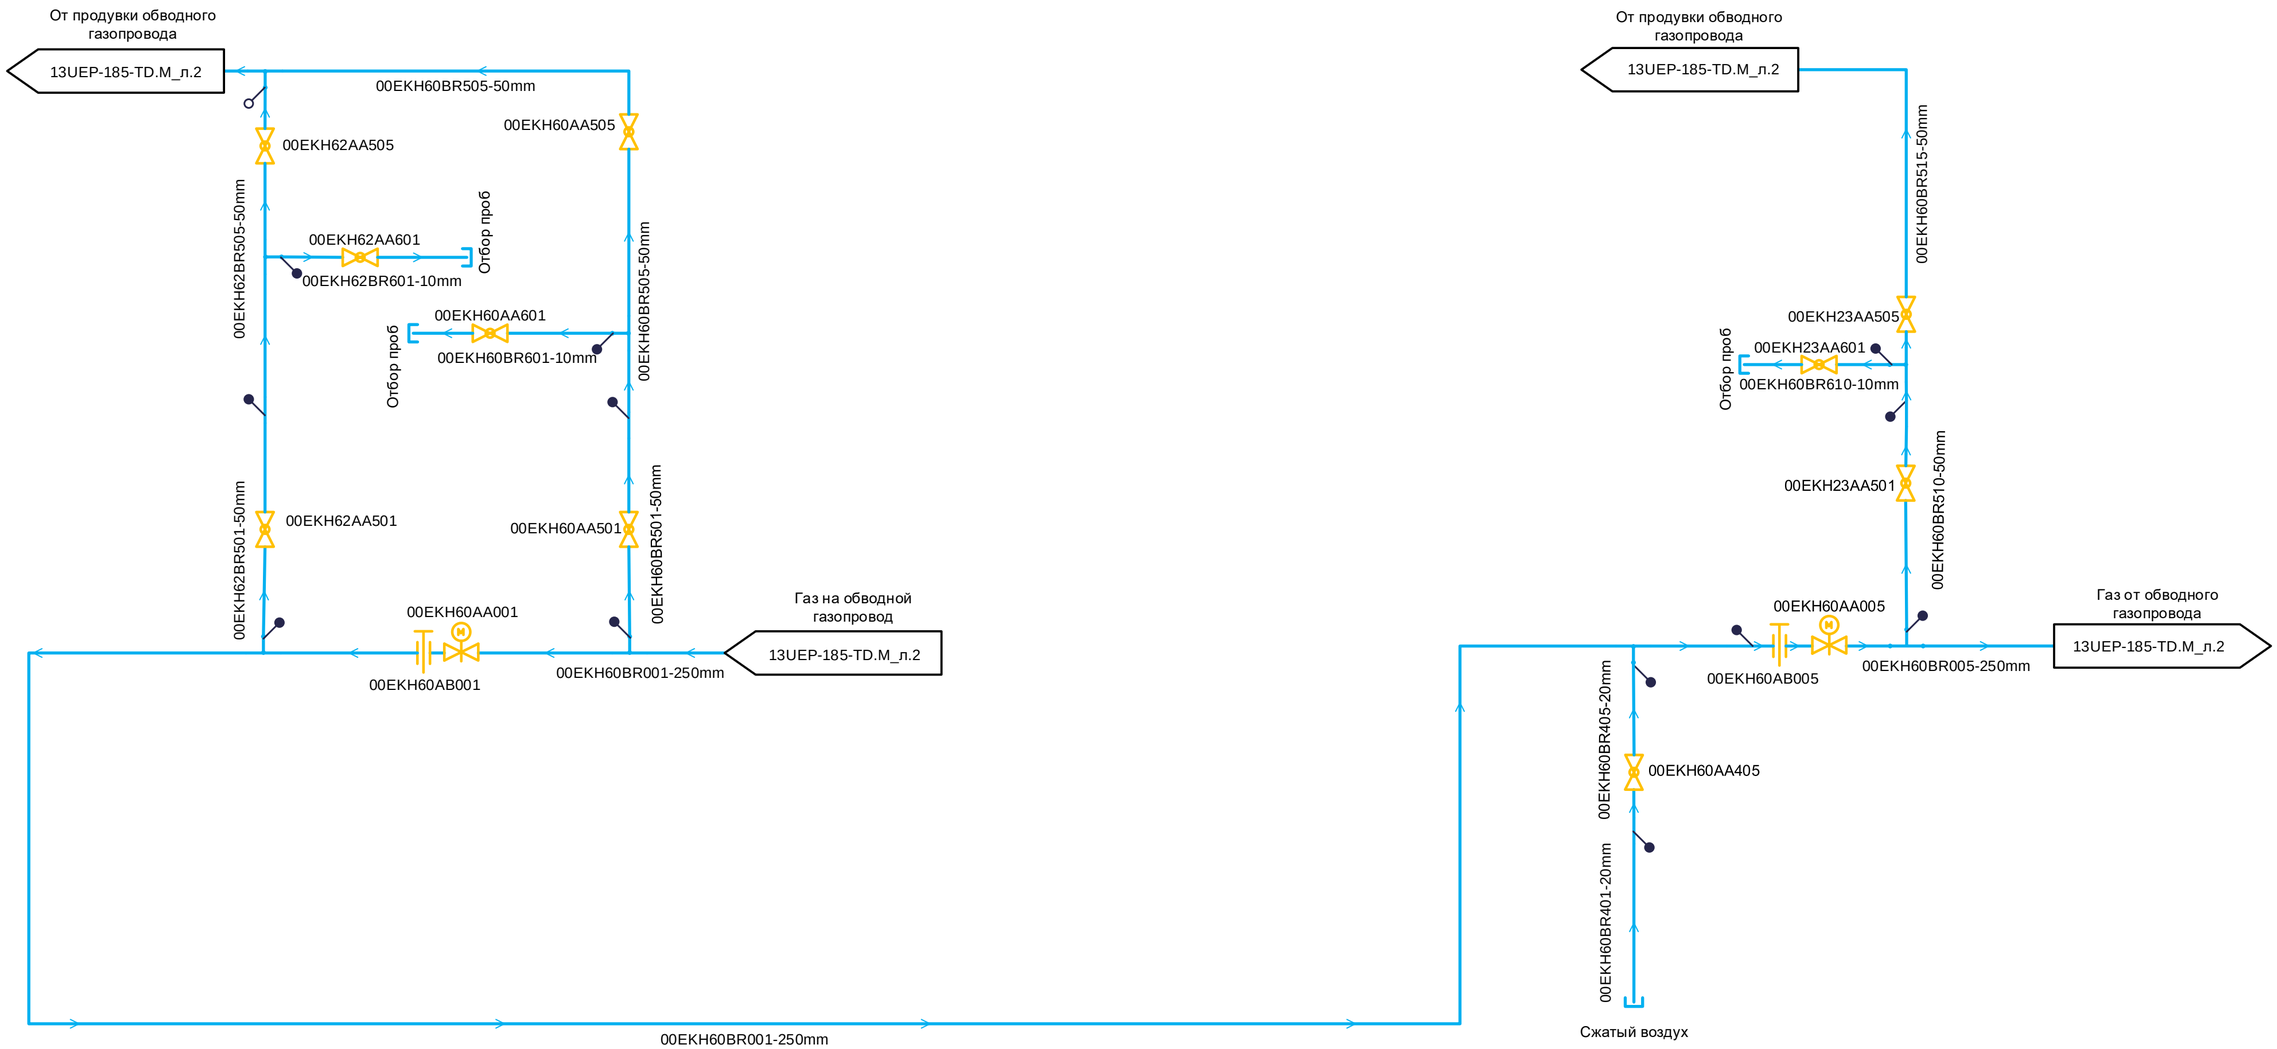

Согласовано

ОАСУ Светашева

Взам. инв. №

Подпись и дата

Инв. № подл.

Изм.	Кол.уч	Лист	№ док.	Подп.	Дата
Разработал		Полянская			
Проверил		Попова			
Гл.спец.		Стацура			
Н. контр.		Гридчина			

68N1-16UEP-5138-TD.M

Строительство Якутской ГРЭС-2

Инжиниринг ДКС и ППГ. Обводной газопровод. PI-диаграмма.

Стадия	Лист	Листов
Р	2	

PI-диаграмма обводного газопровода. Система ЕКН.

АКЦИОНЕРНОЕ ОБЩЕСТВО ИНСТИТУТ ТЕПЛОЭЛЕКТРОПРОЕКТ Г. МОСКВА

Формат А2