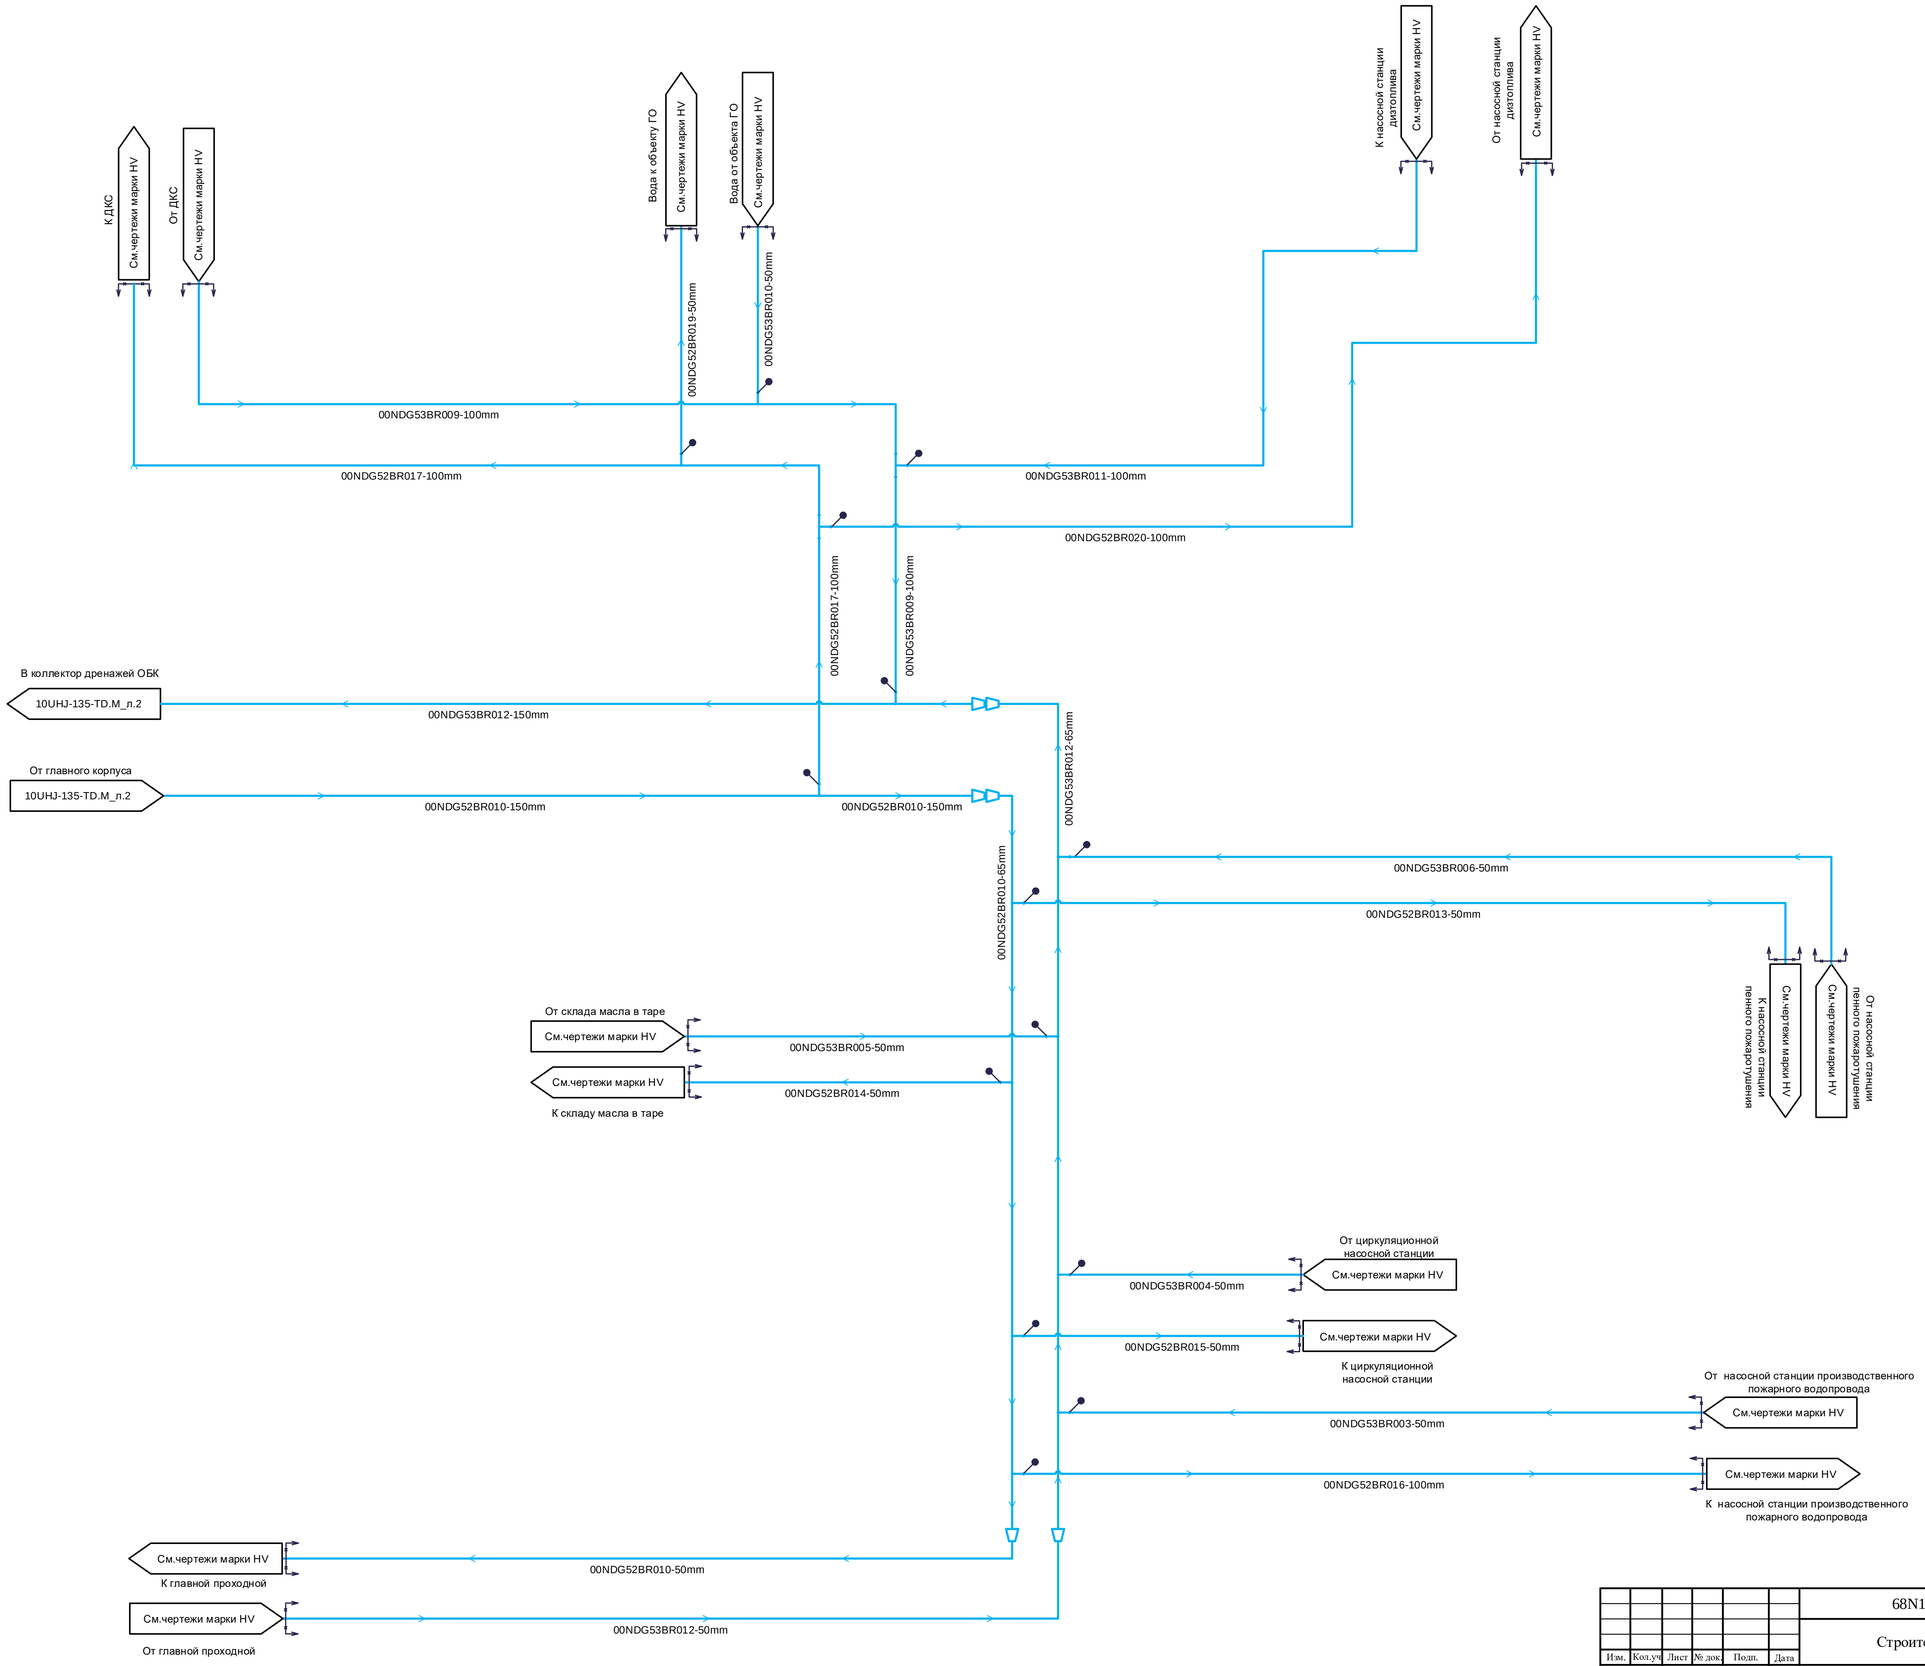

Изм.	Кол.уч	Лист	№ док.	Подп.	Дата	68N1 – 11UTZ – 681 – TD.M
						Строительство Якутской ГРЭС-2
Разработал		Полянская				Основная площадка. Эстакады. Собственные нужды на вспомогательные сооружения. PI-диаграмма
Проверил		Стацура				Стадия: Р; Лист: 2; Листов:
Н. контр.		Грядчина				PI- диаграмма собственных нужд на вспомогательные сооружения. Система NDG

АКЦИОНЕРНОЕ ОБЩЕСТВО ИНСТИТУТ ТЕПЛОЭЛЕКТРОПРОЕКТ Г. МОСКВА

Согласовано

Взам. инв. №

Подпись и дата

Инв. № подл.

Формат А1